




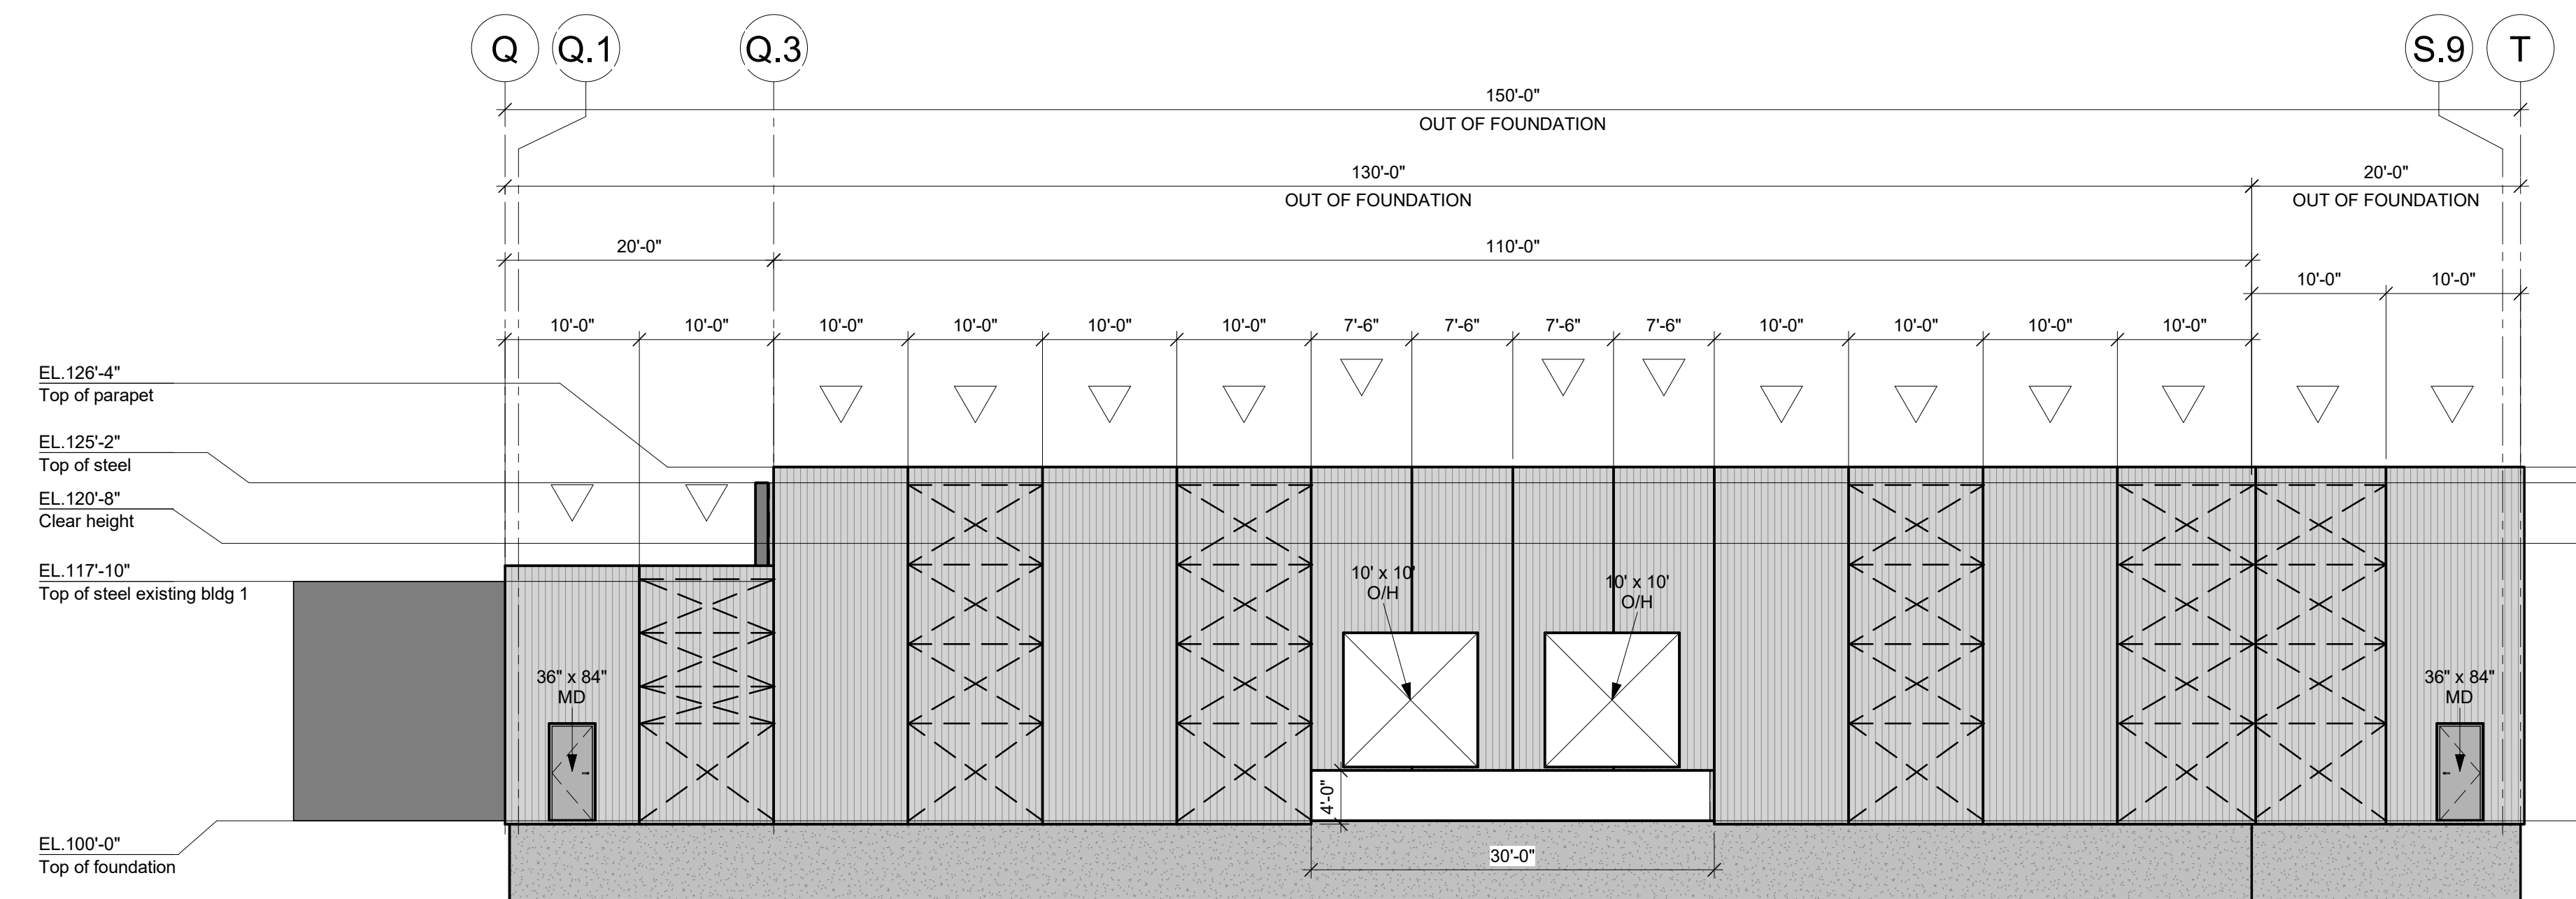


ELEVATION LINE 2 (SOUTH)
1" = 10'-0"

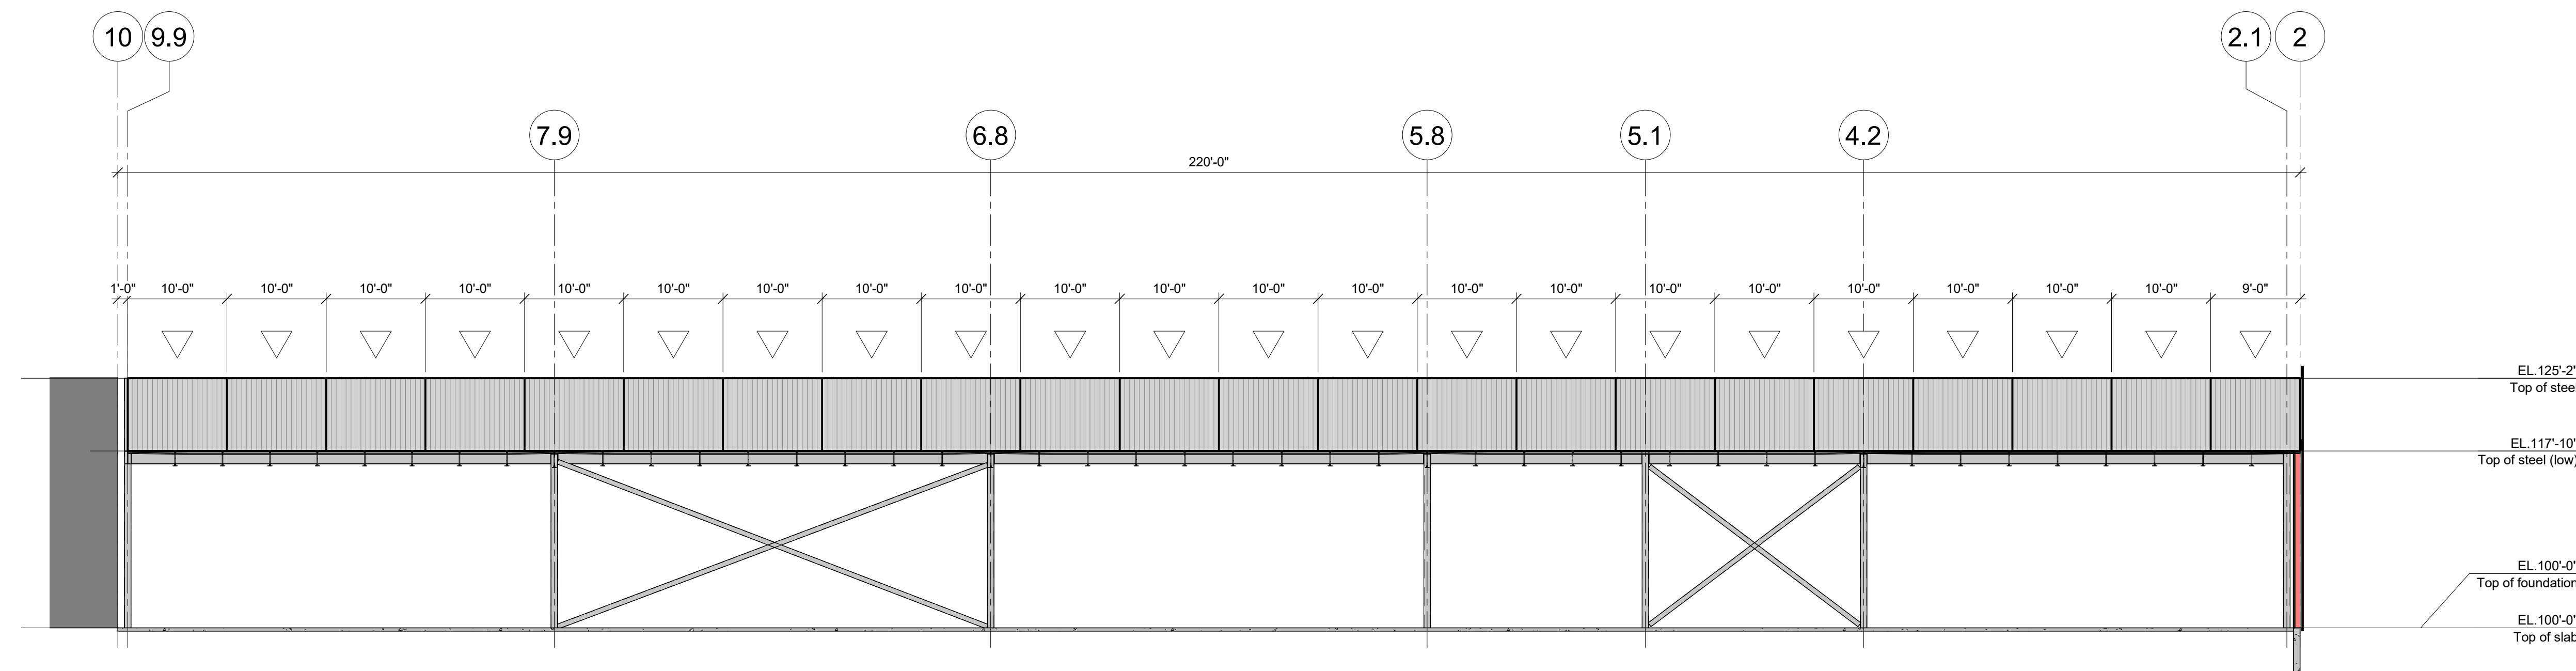

ELEVATION LINE Q.3 (HIGH & LOW PANELS)(WEST)
1" = 10'-0"

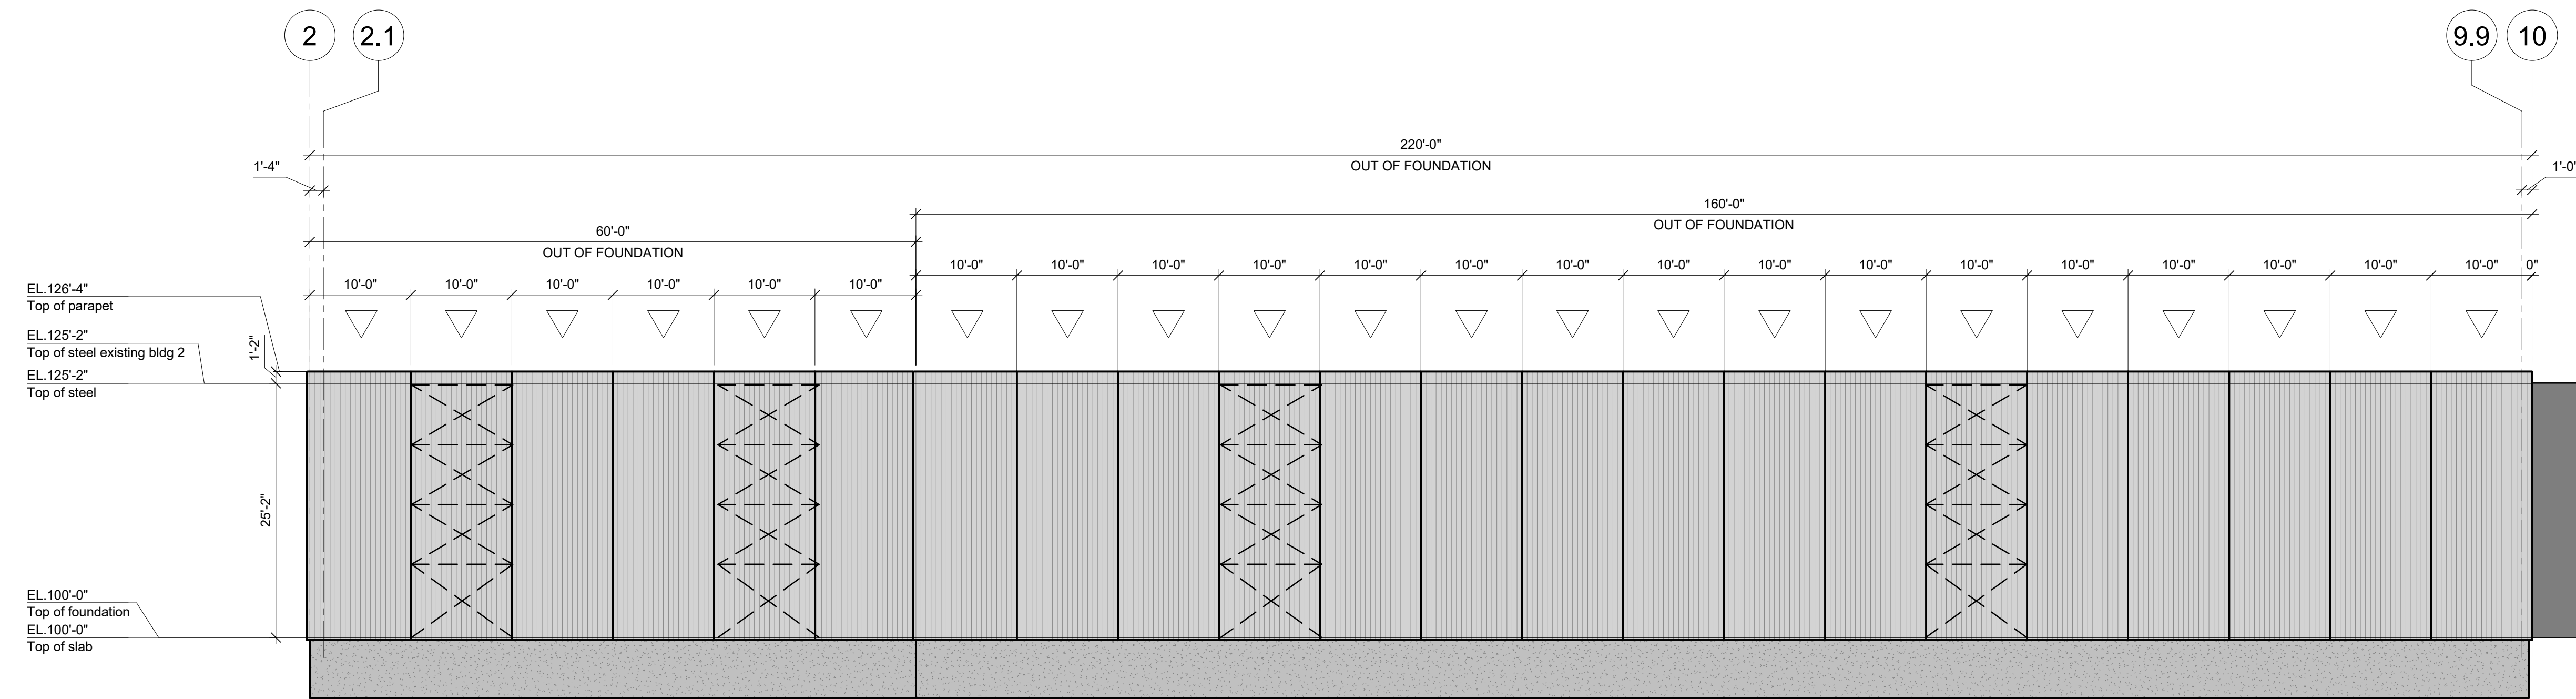

ELEVATION LINE S.6 & T (EAST)
1" = 10'-0"

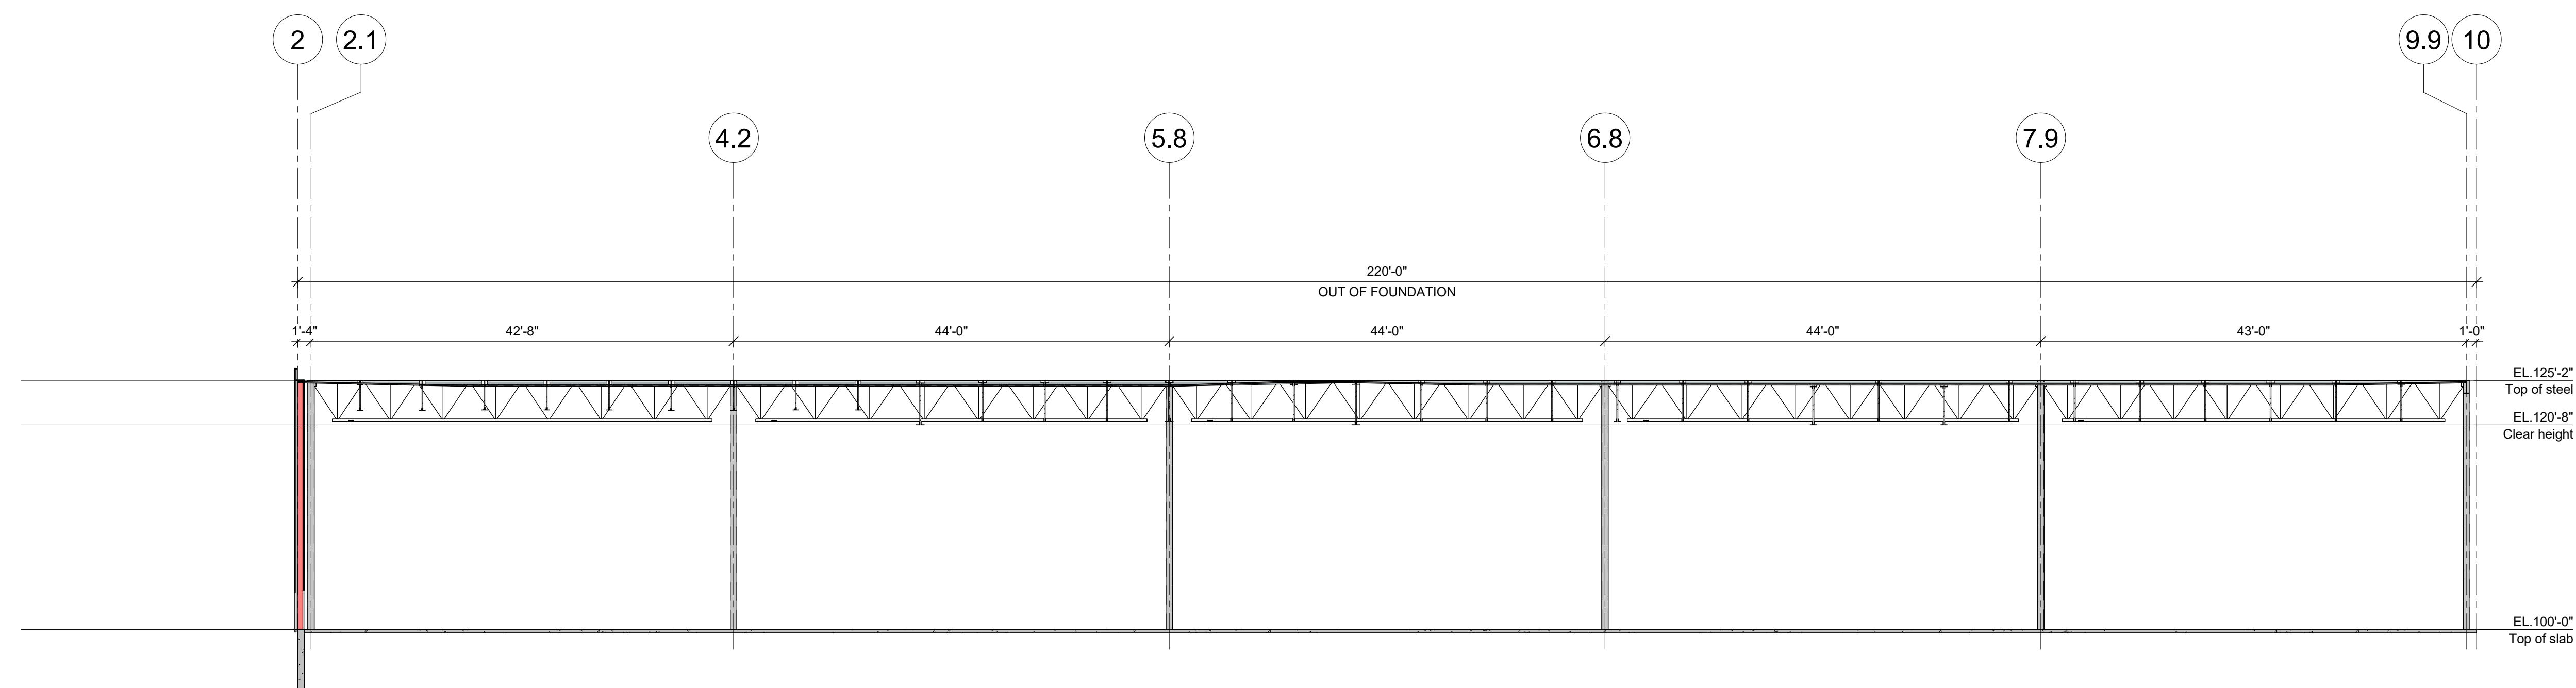

ELEVATION LINE R.7 (STRUCTURE) (EAST)
1" = 10'-0"