




DOOR SCHEDULE				
Identity	Qty.	Door 18 ga.	Remarks	
		Dimensions		
D1	2	36" x 84"	DOORS	
D2	2	10' x 10'	OPENINGS	

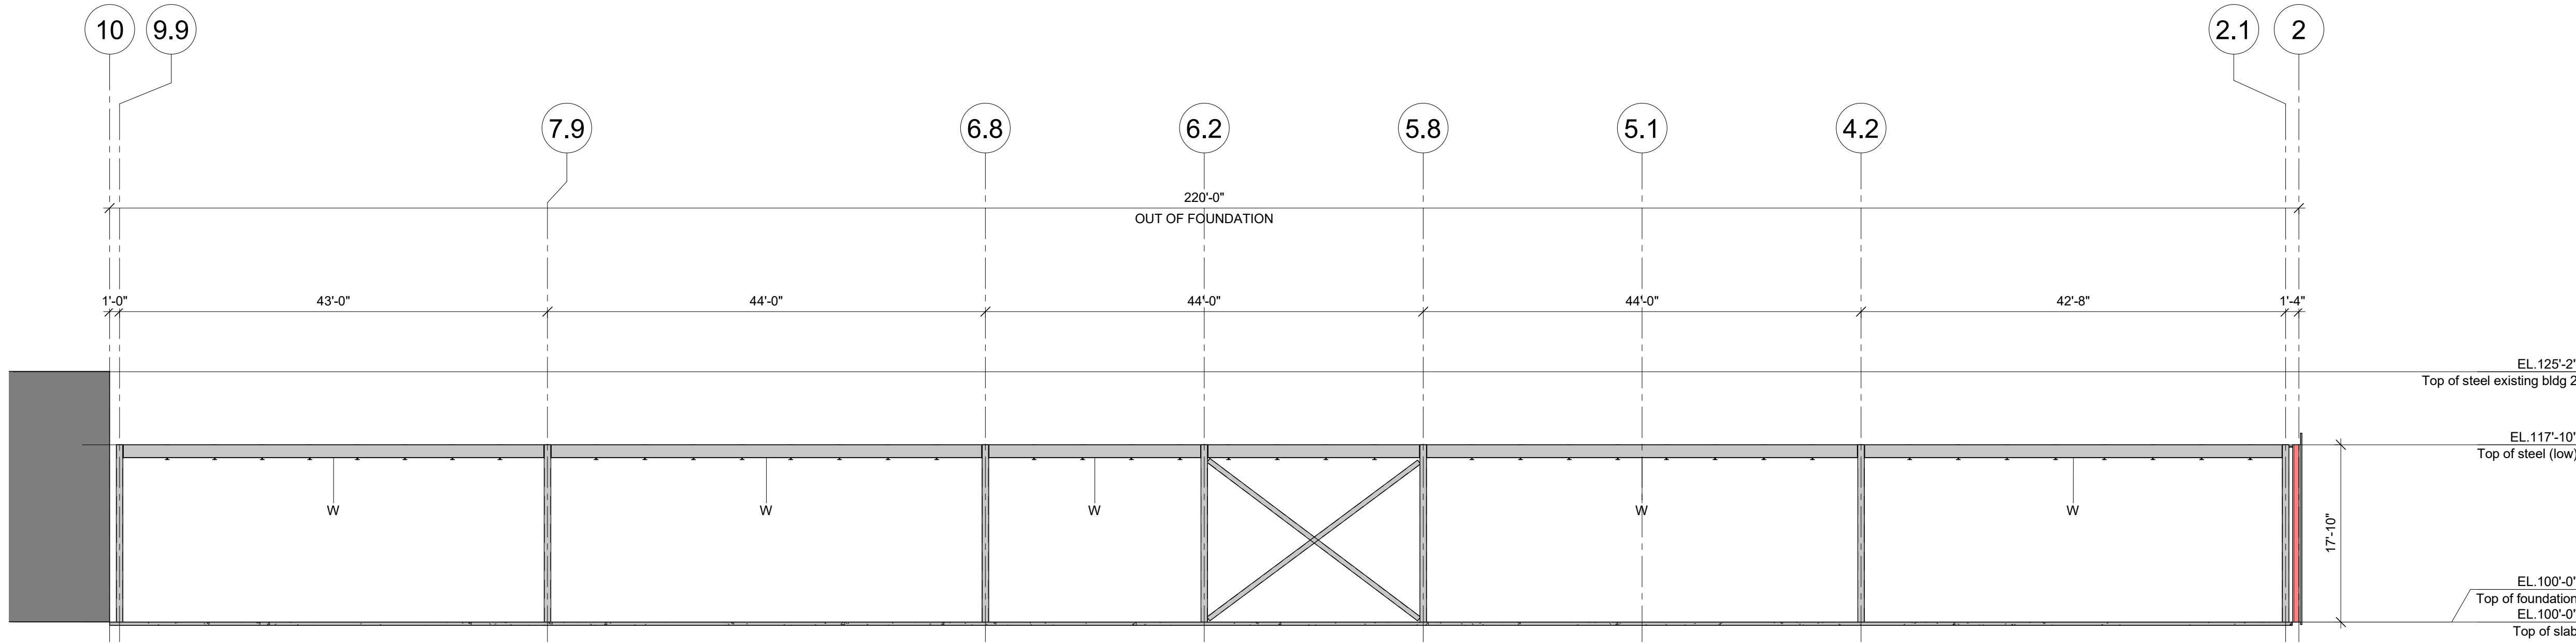

ELEVATION LINE Q (STRUCTURE)(WEST)
1" = 10'-0"

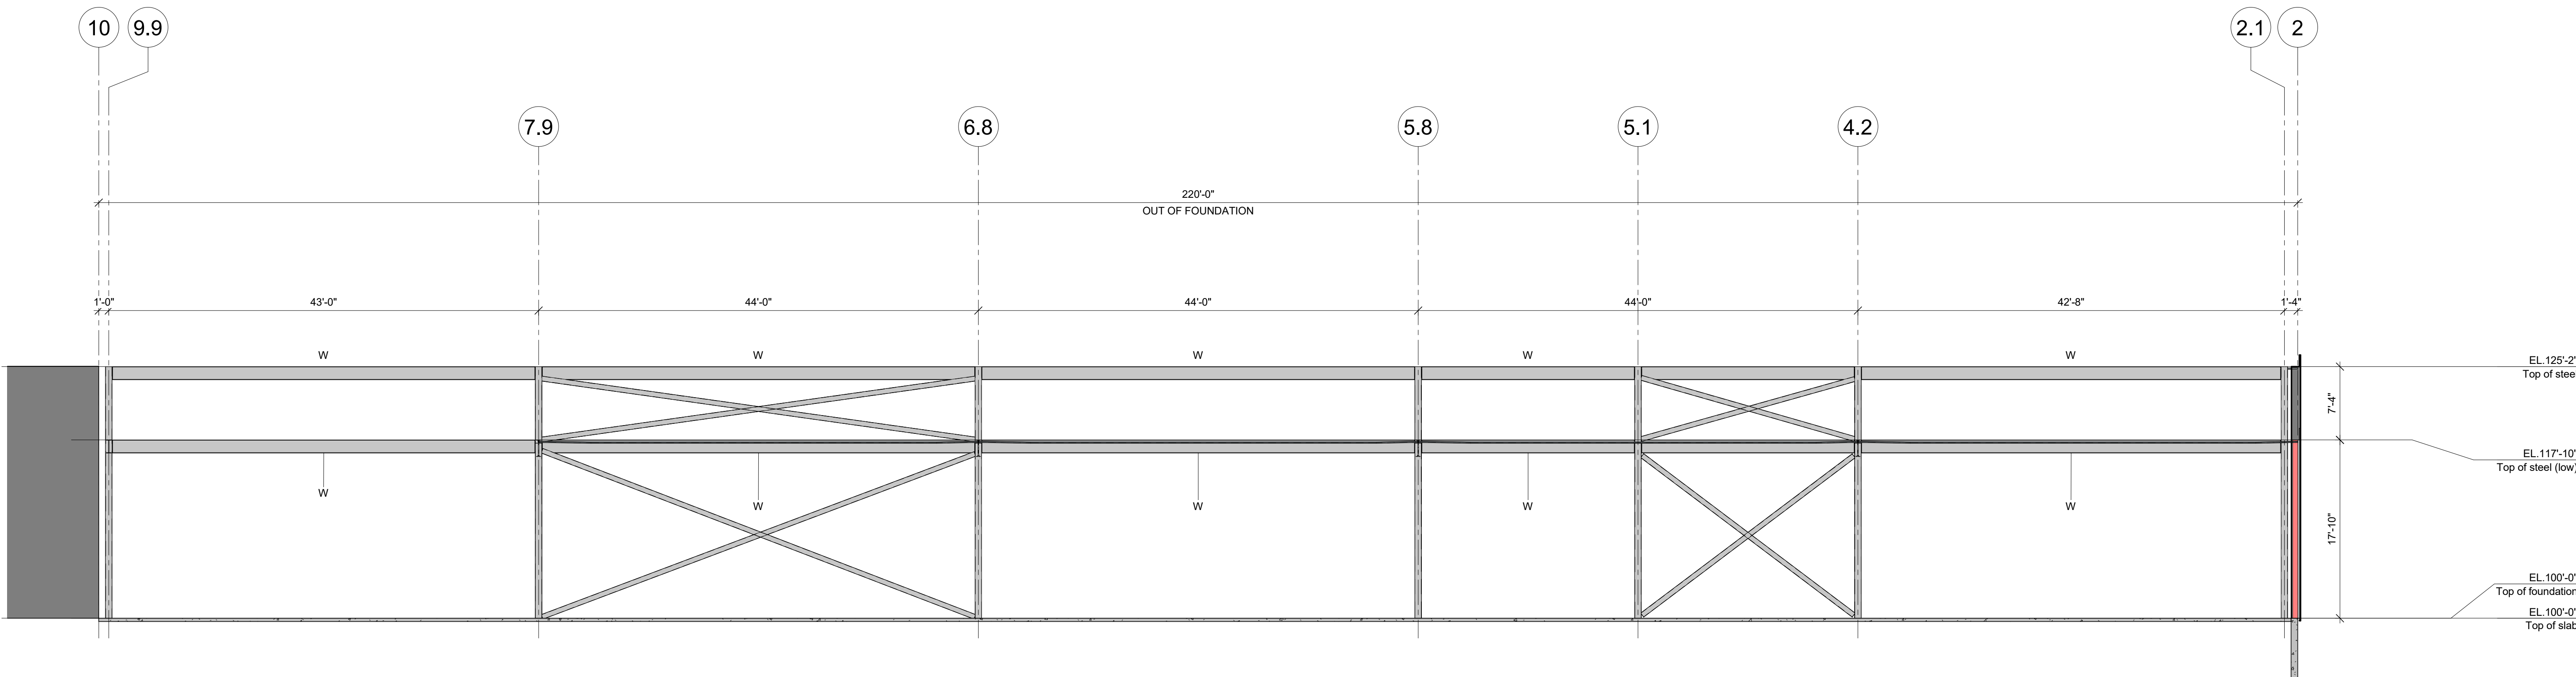

ELEVATION LINE Q.3 (STRUCTURE HIGH & LOW) (WEST)
1/8" = 1'-0"

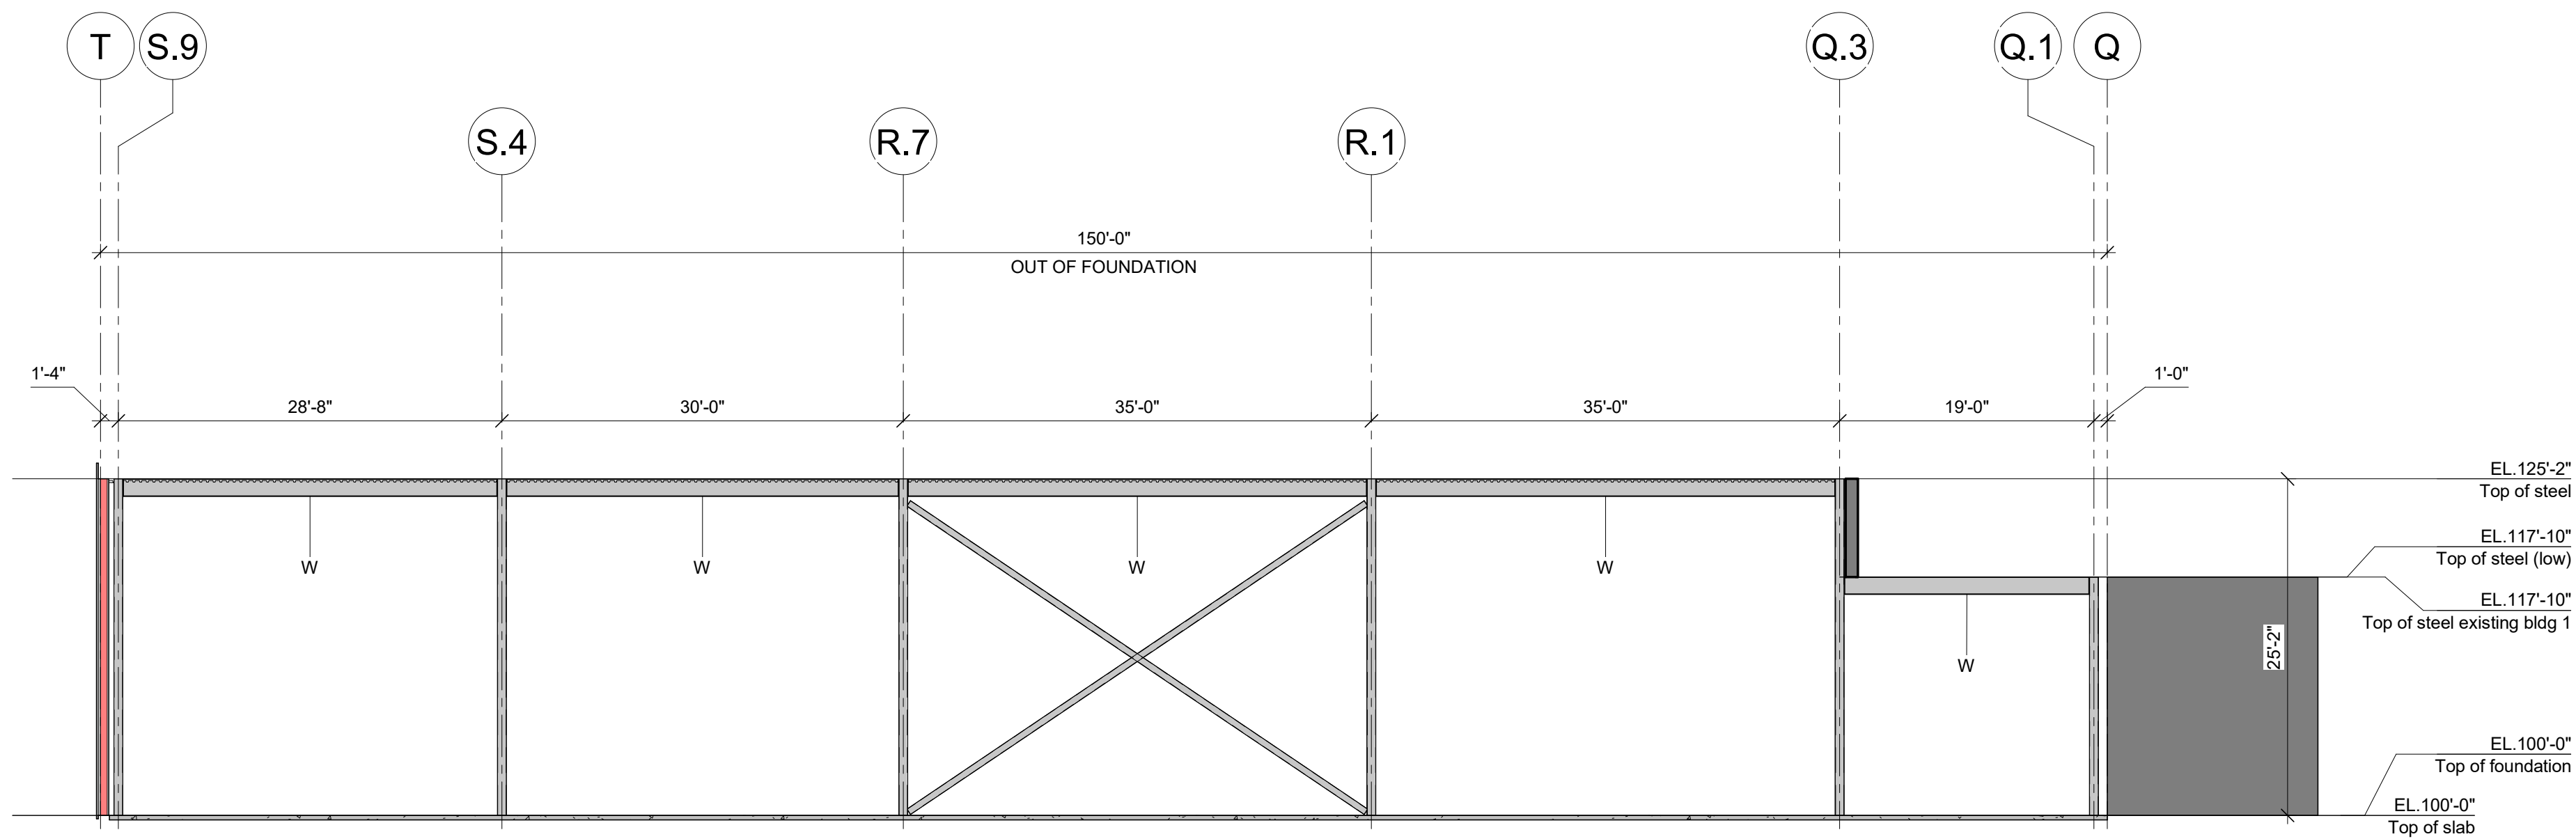

ELEVATION LINE 9.9 (STRUCTURE) (NORTH)
1" = 10'-0"

