




REMOVING THIS PANEL
WILL REQUIRE
MODIFICATIONS TO
SUPPORT THE EXISTING
JOISTS (BY OTHERS)

EXISTING
PANEL WALL TO
BE REMOVED


EXISTING BUILDING
(TOS 125'-2")

EXISTING BUILDING
(TOS 117'-10")

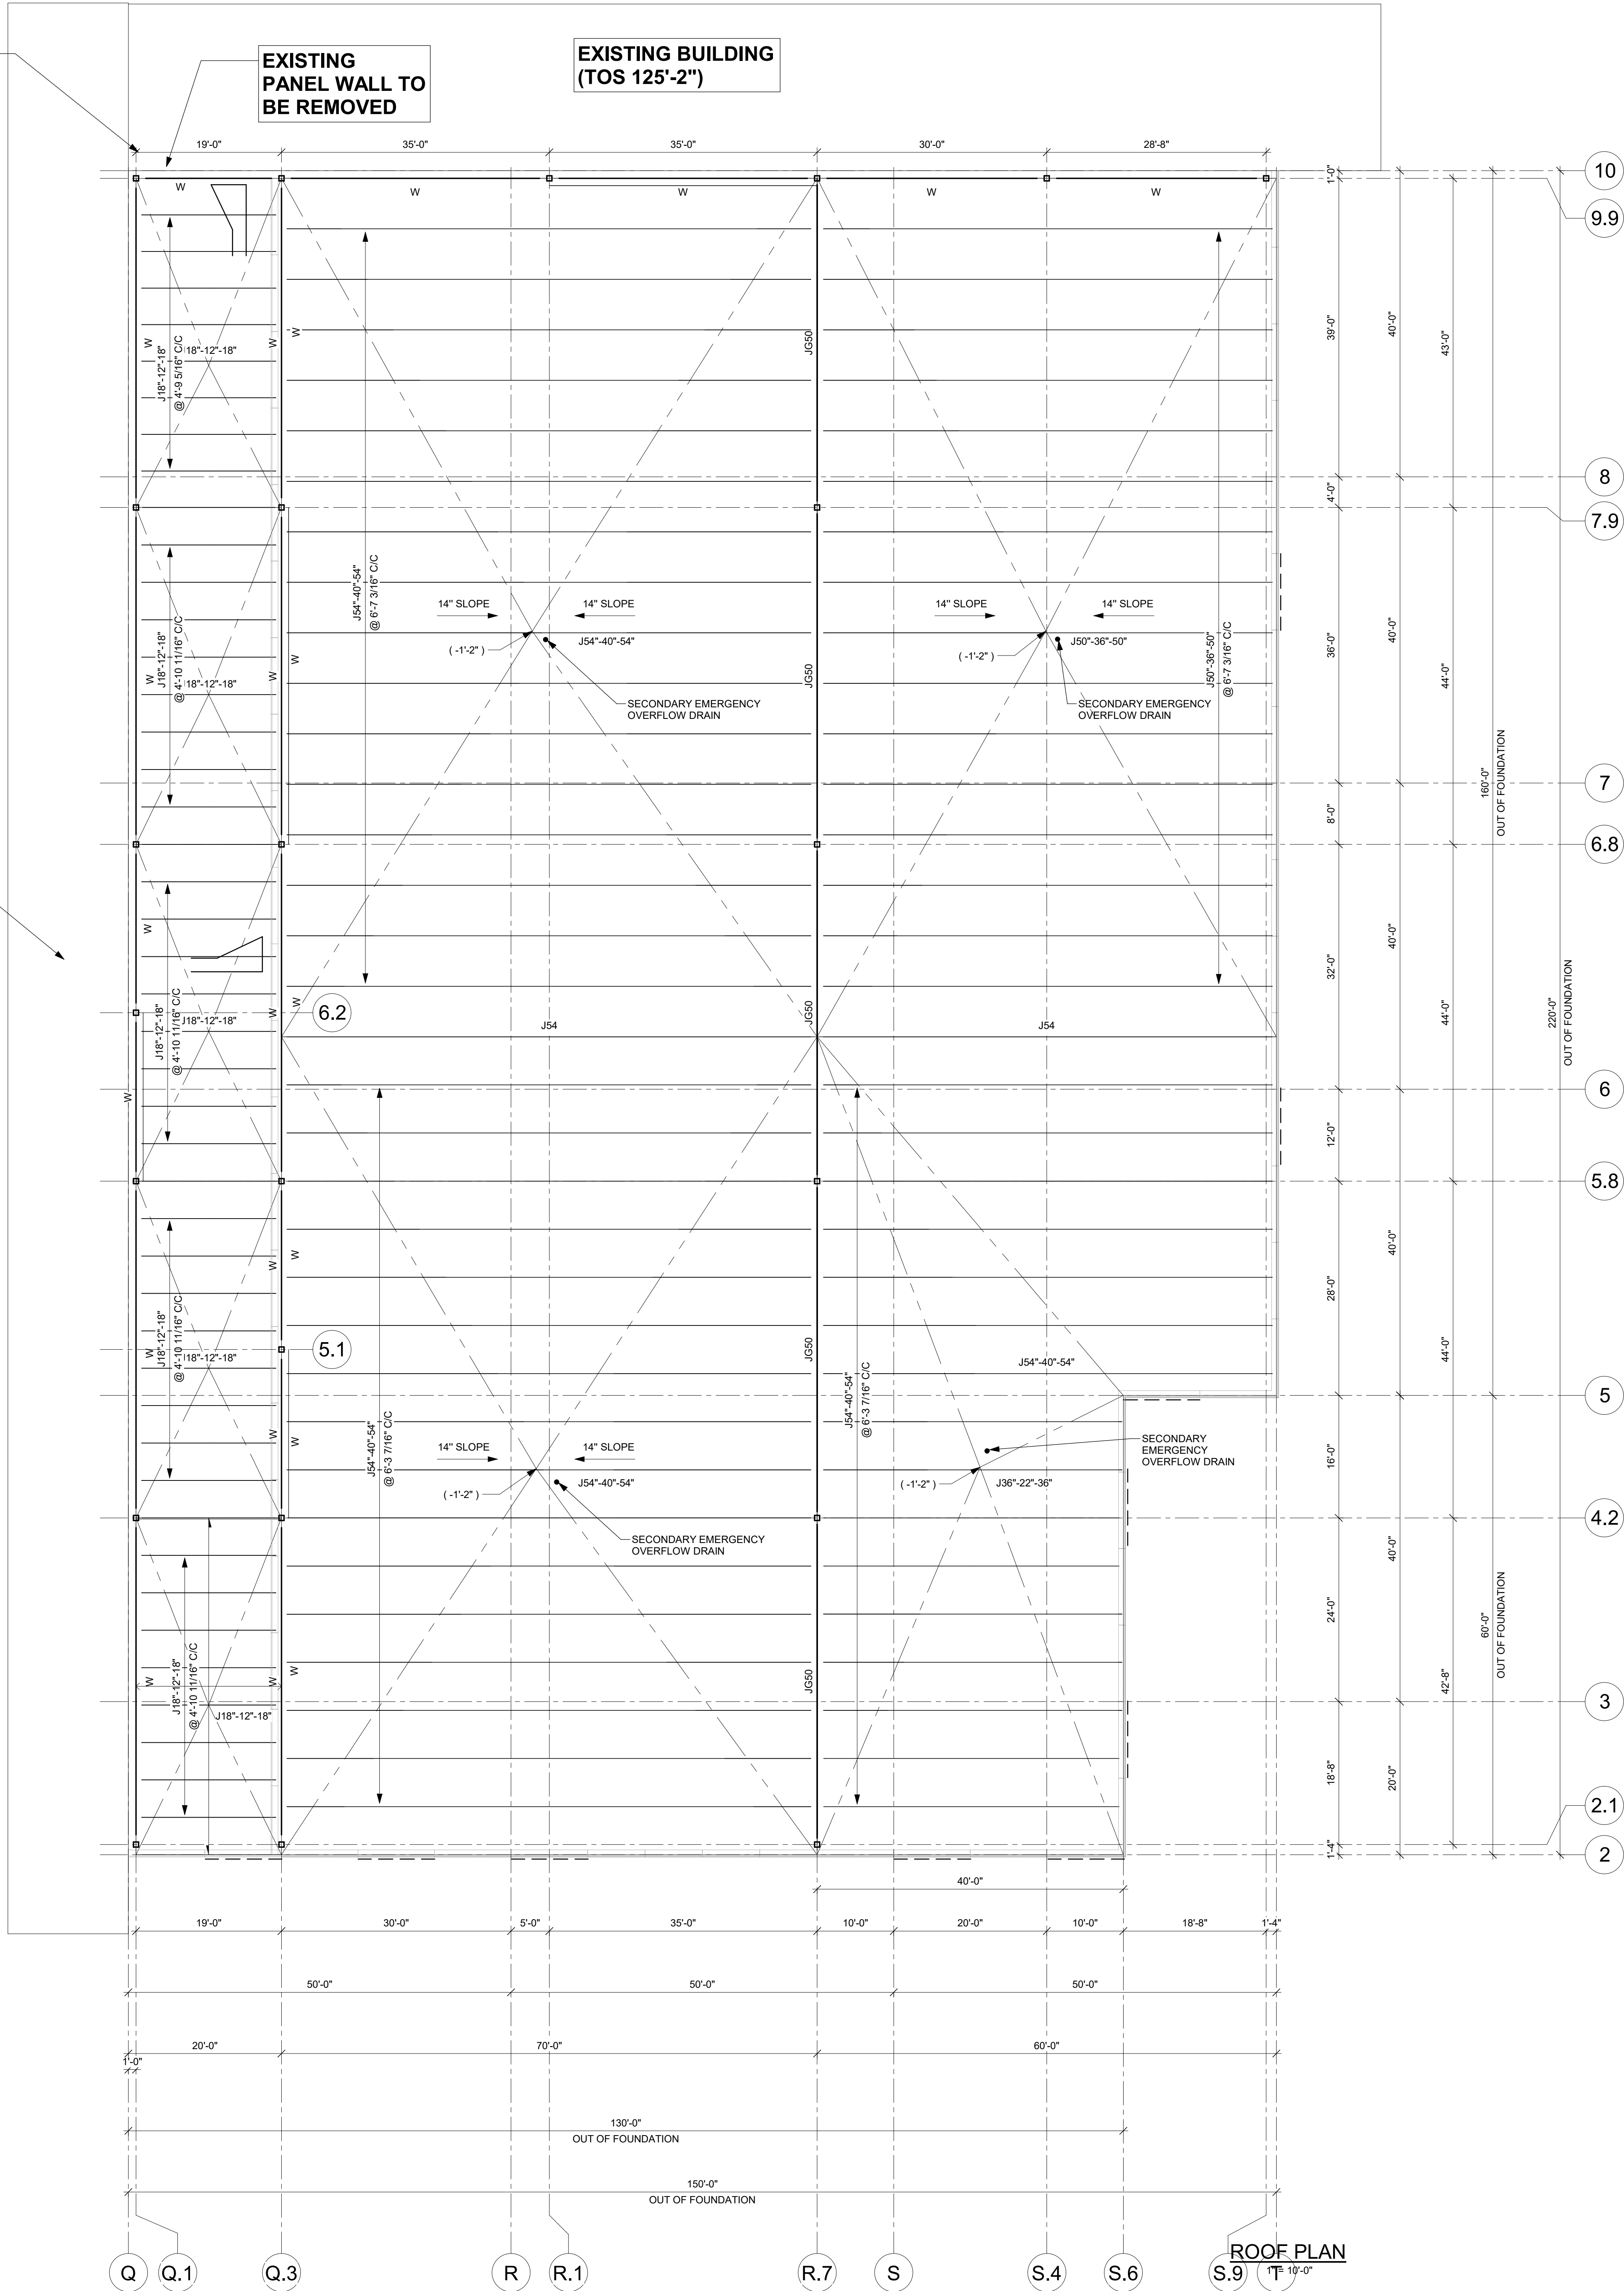

ROOF PLAN

GROSS UPLIFT DIAGRAM (UNFACTORED):

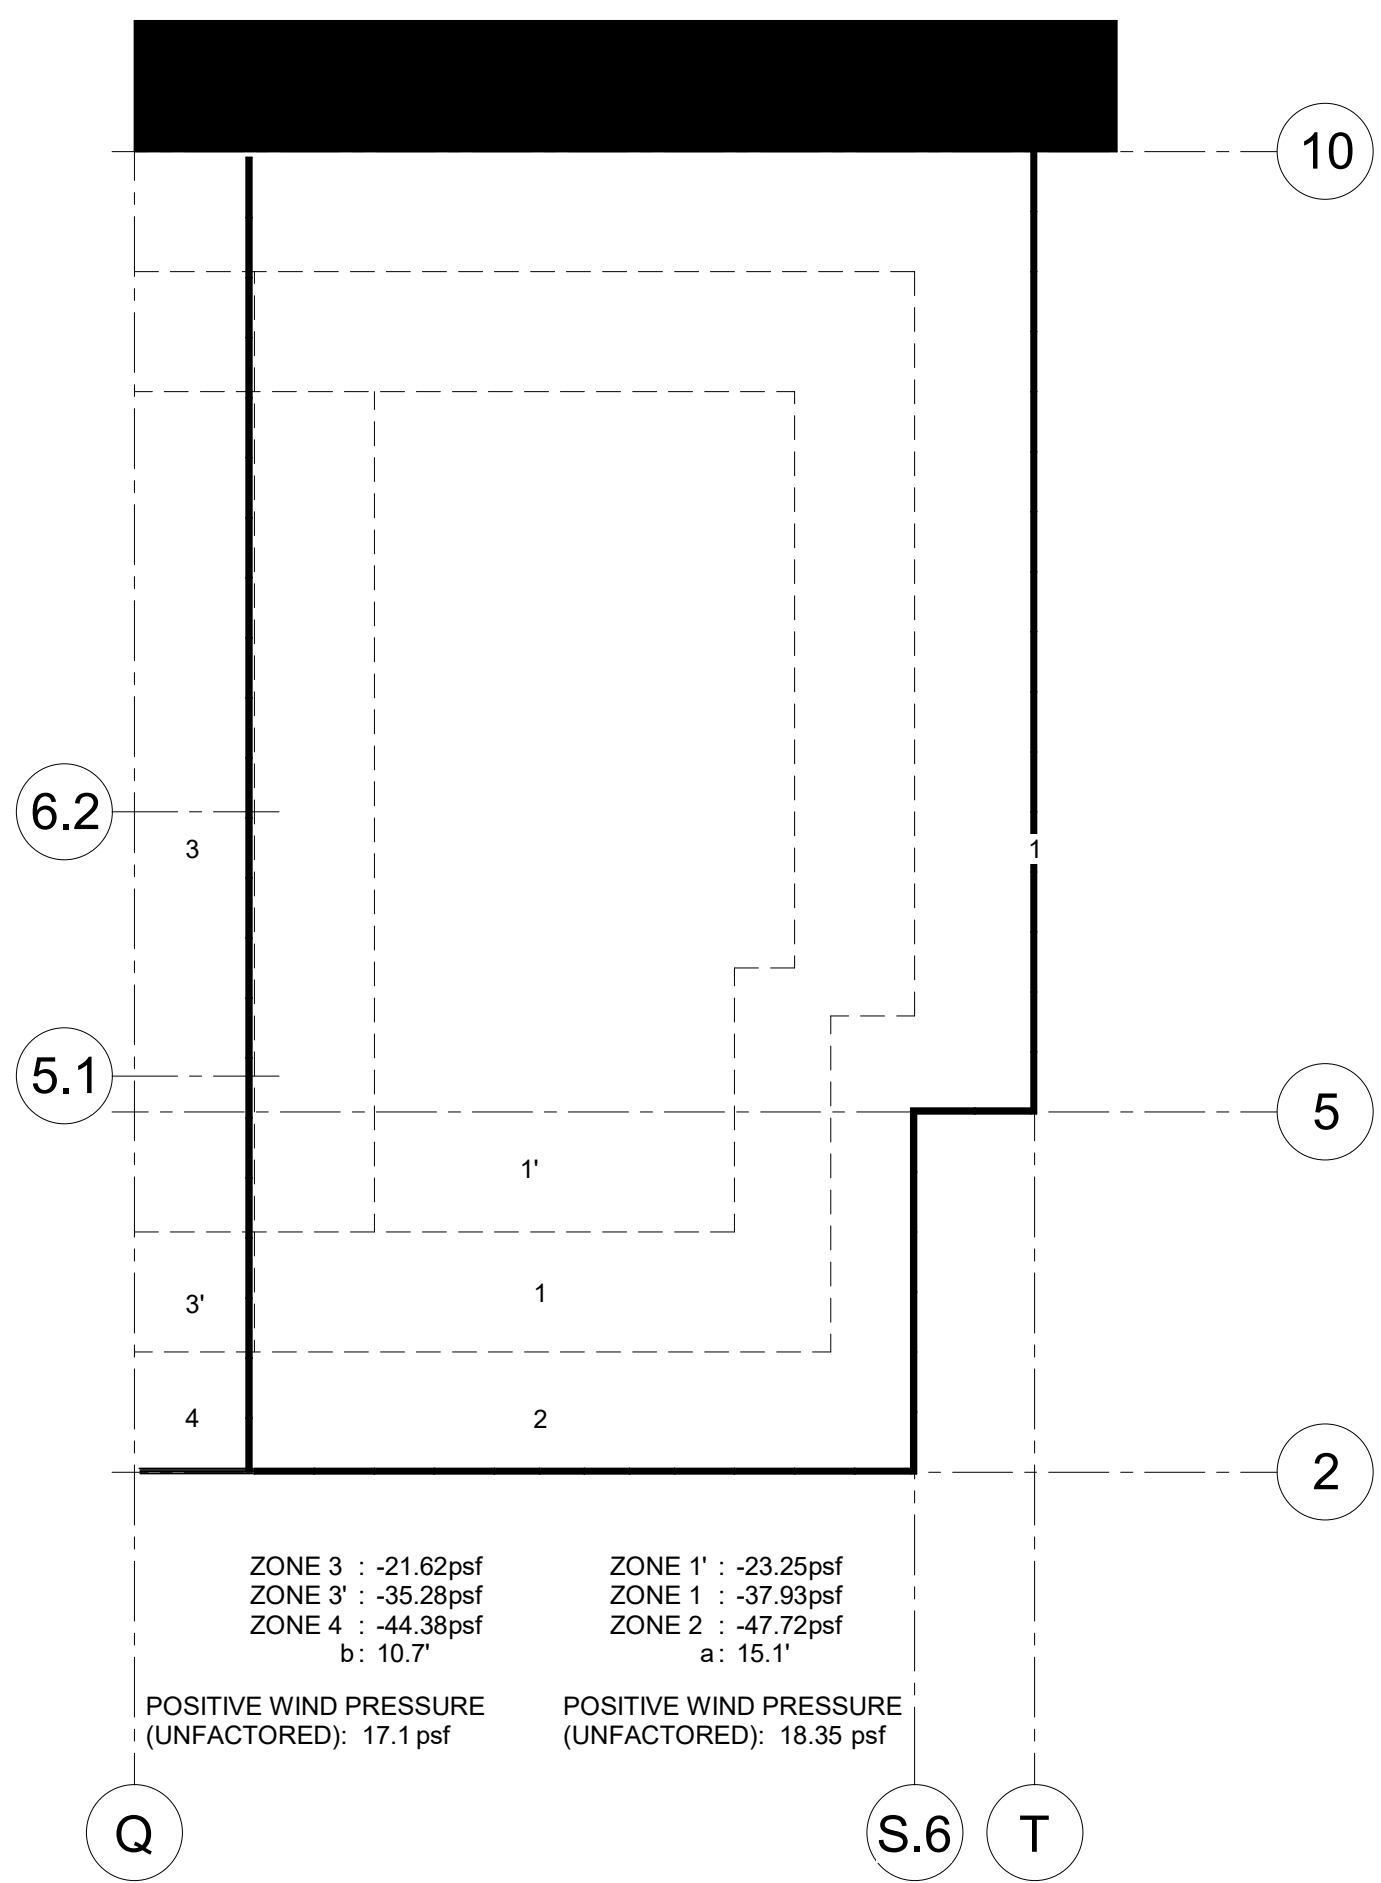

CONTRACTOR/RECTOR NOTE:

IT IS PROHIBITED TO MODIFY, COPY, REPRODUCE OR OTHERWISE
DISTRIBUTE THIS DRAWING OR ANY REPRESENTATION OF THIS
DRAWING, OR ANY MEDIA, INCLUDING ELECTRONIC, WITHOUT THE
PRIOR WRITTEN APPROVAL OF CANAM BUILDINGS US INC.

ROOF

TOP OF PLASTER RWL : 98'-0"
TOP OF PLASTER : 99'-0"
TOP OF SLAB : 100'-0"
TOP OF FOUNDATION : 100'-0"
CLEAR HEIGHT : 120'-0"
TOP OF STEEL : see sketch
PARAPET HEIGHT : 1'-2"
TOP OF PARAPET : 126'-4"

LOADS

D.L. : 18 psf
Coll. : 5 psf
Ground snow load : 80 psf
Roof live load : 0 psf
Roof snow load Ph : 56 psf
Wind speed (exposure) : 100mph (C)
Velocity pressure qz : 29.42 psf

EARTHQUAKE LOADS ASSUME

Ss : 0.32
Si : 0.078
SEISMIC DESIGN CATEGORY: B
U : 1
SITE CLASS : D

LOADINGS:

- Roof dead load excluding collateral load : psf
- Collateral load : psf (includes lighting and/or mechanical and sprinklers of 4 inches in diameter and less)
- Roof snow load : psf
- Basic wind speed : mph (wind exposure category type B)
- Roof live load : psf
- Ground snow load : psf
- Risk Category : II

- Applicable Code : IBC 2015 and local code for State of Maine
- Assumed soil site class: D

NOTES:

1. When the Chapter 17 of the IBC code is deemed to apply, Canam assumes that the owner or the owner's authorized agent, will employ one or more approved agencies to provide special inspections and tests during construction. The approved agency will submit all inspections and tests to Canam, to allow for the issuance of the certificate of Compliance.
2. If, however, the seismic site class is determined to be E or F according to the geotechnical report, the preliminary structural concept (location and geometry of bracing, etc.) must be validated and coordinated by a Canam's engineer.

PRELIMINARY

NOT TO BE USED FOR CONSTRUCTION

REVISION DATE DESCRIPTION USER VER

PROJECT MANAGER
-

DRAFTING
-

DRAWN S.L. DESIGNED PROJECT ENGINEER SCALE: AS INDICATED

CHECKED CONSULTING ENGINEERS ARCHITECTS DATE (yyyy/mm/dd) 2028/02/24

CUSTOMER: J.S. MCCARTHY CO.

CANAM

28 Birch Street, Milford, Massachusetts, 01757, US

Phone : (508) 571-3350

Toll Free : (866) 466-8769

www.canam.com

PROFESSIONAL SEAL

PROJECT

ROLL WAREHOUSE ADDITION

15 DARIN DR. AUGUSTA, MAINE

04330

DRAWING TITLE

PRELIMINARY SKETCH - ROOF PLAN

CONTRACT NUMBER P2026-031

DRAWING NUMBER EsMx401

DIVISION

REVISION

Initials