




DOOR SCHEDULE			
Identity	Qty.	Dimensions	Remarks
D1	2	36" x 84"	DOORS
D2	2	10' x 10'	OPENINGS

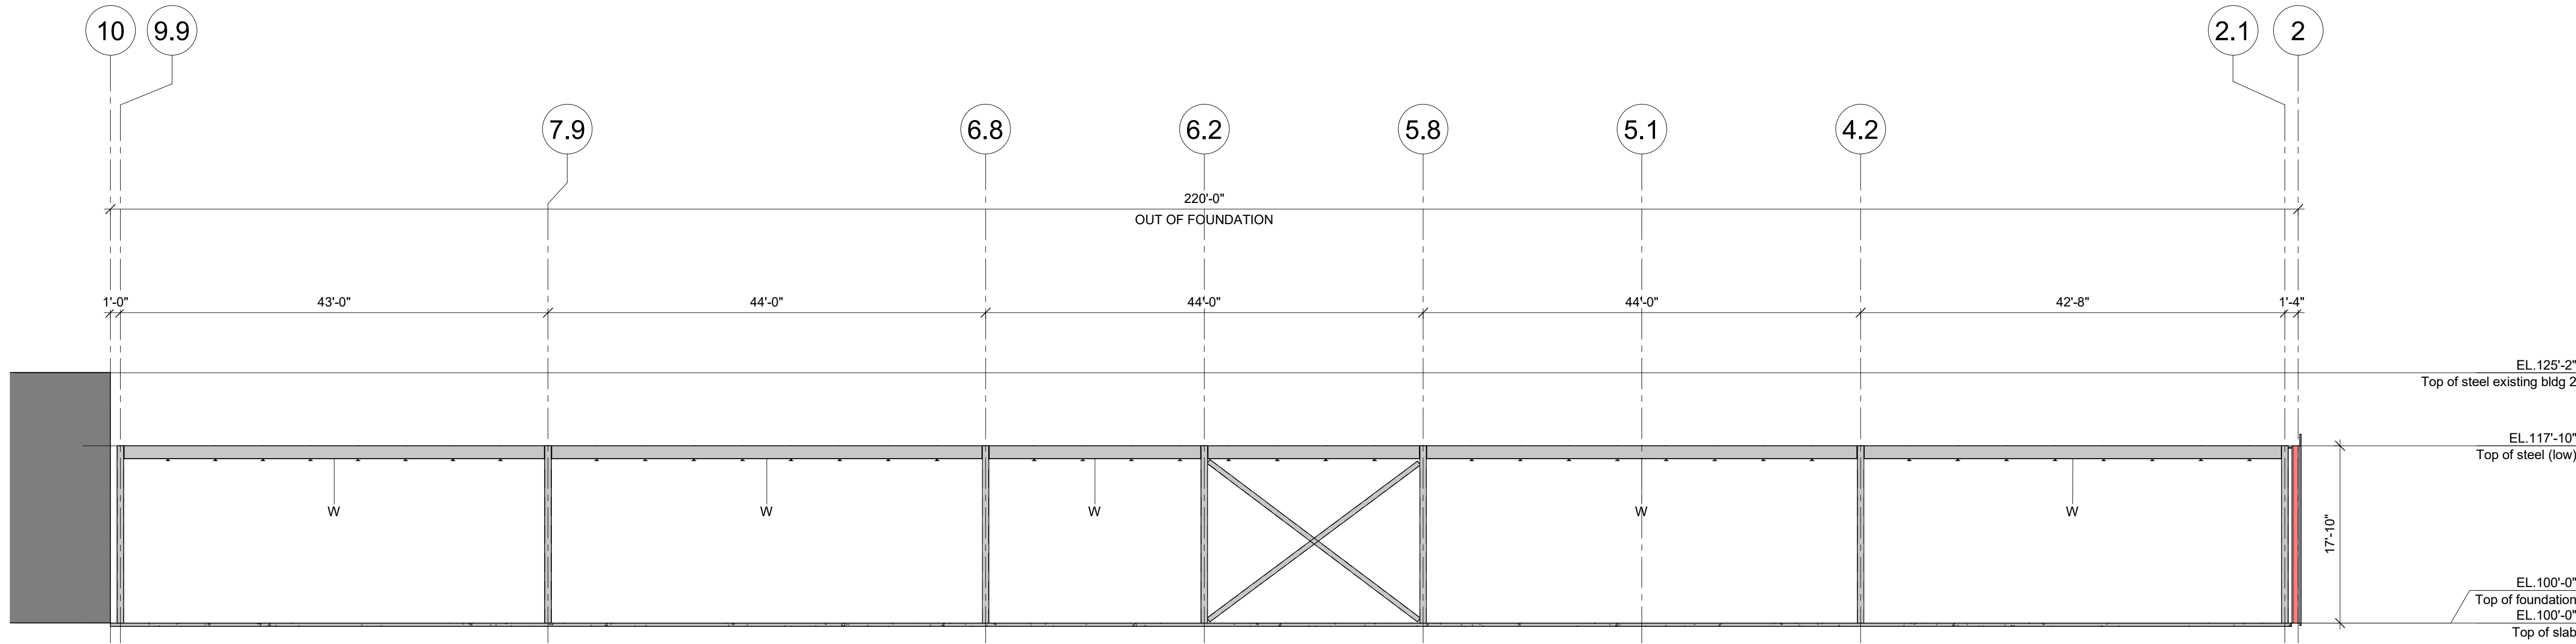


ELEVATION LINE Q (STRUCTURE)(WEST)
1" = 10'-0"

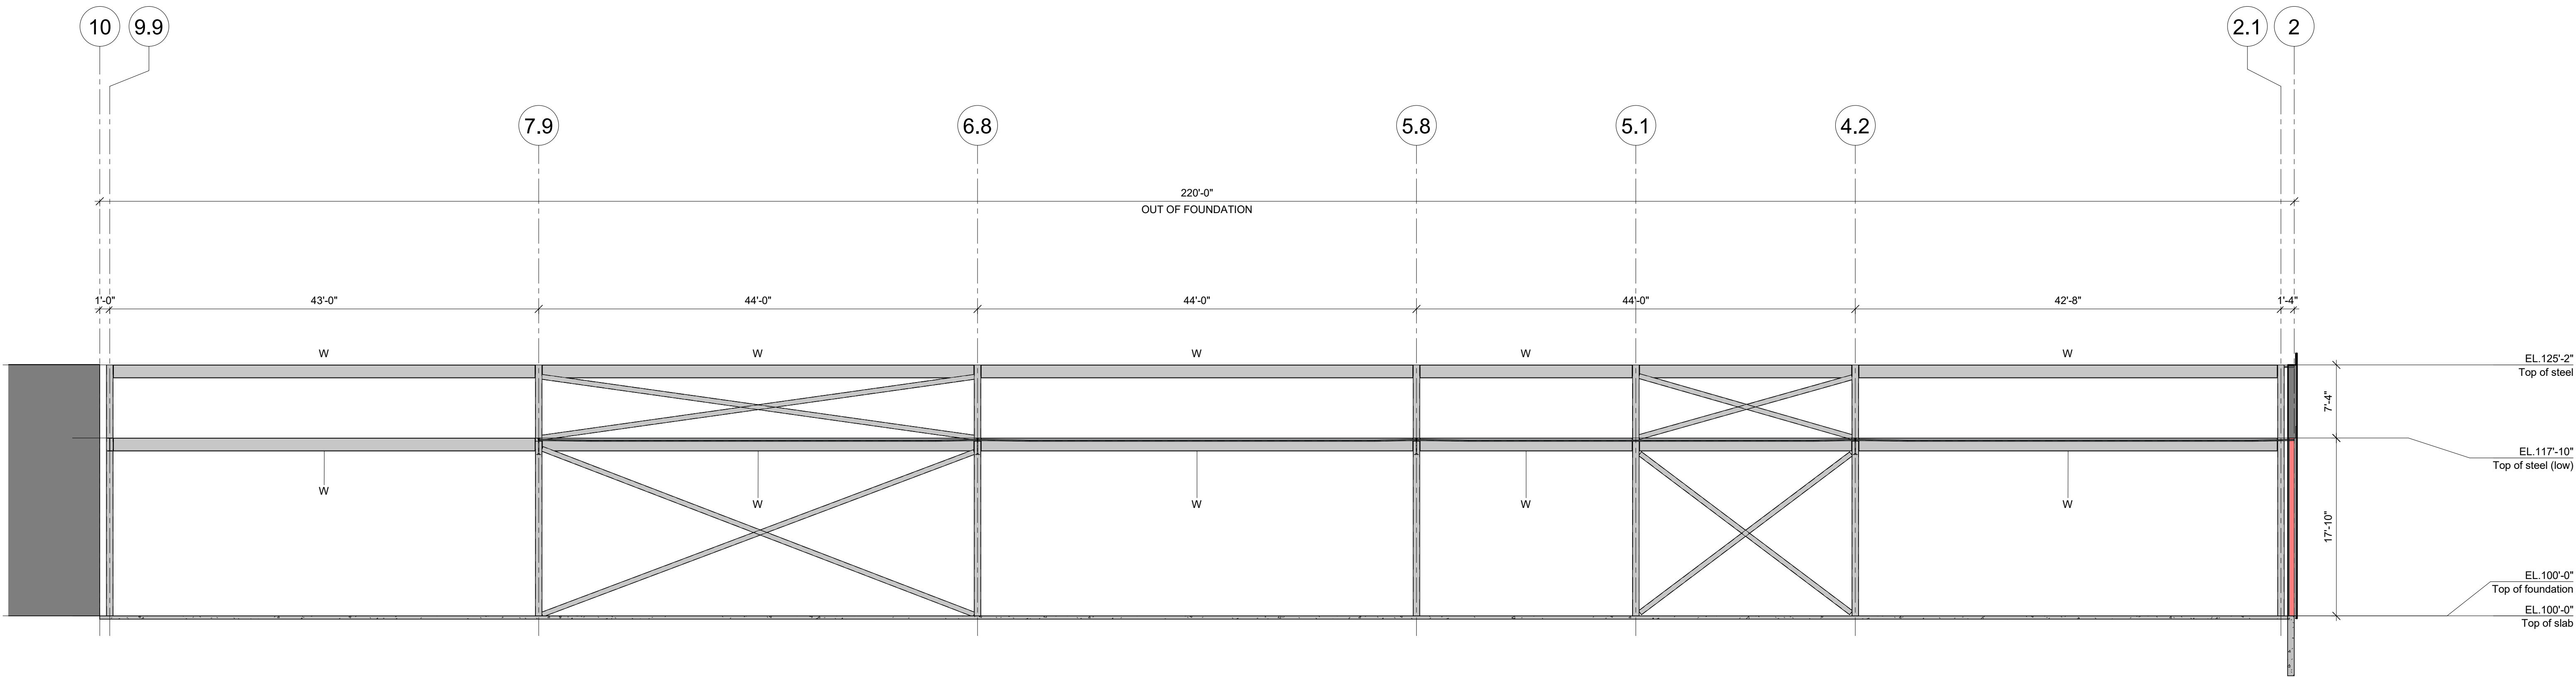

ELEVATION LINE Q.3 (STRUCTURE HIGH & LOW) (WEST)
1/8" = 1'-0"

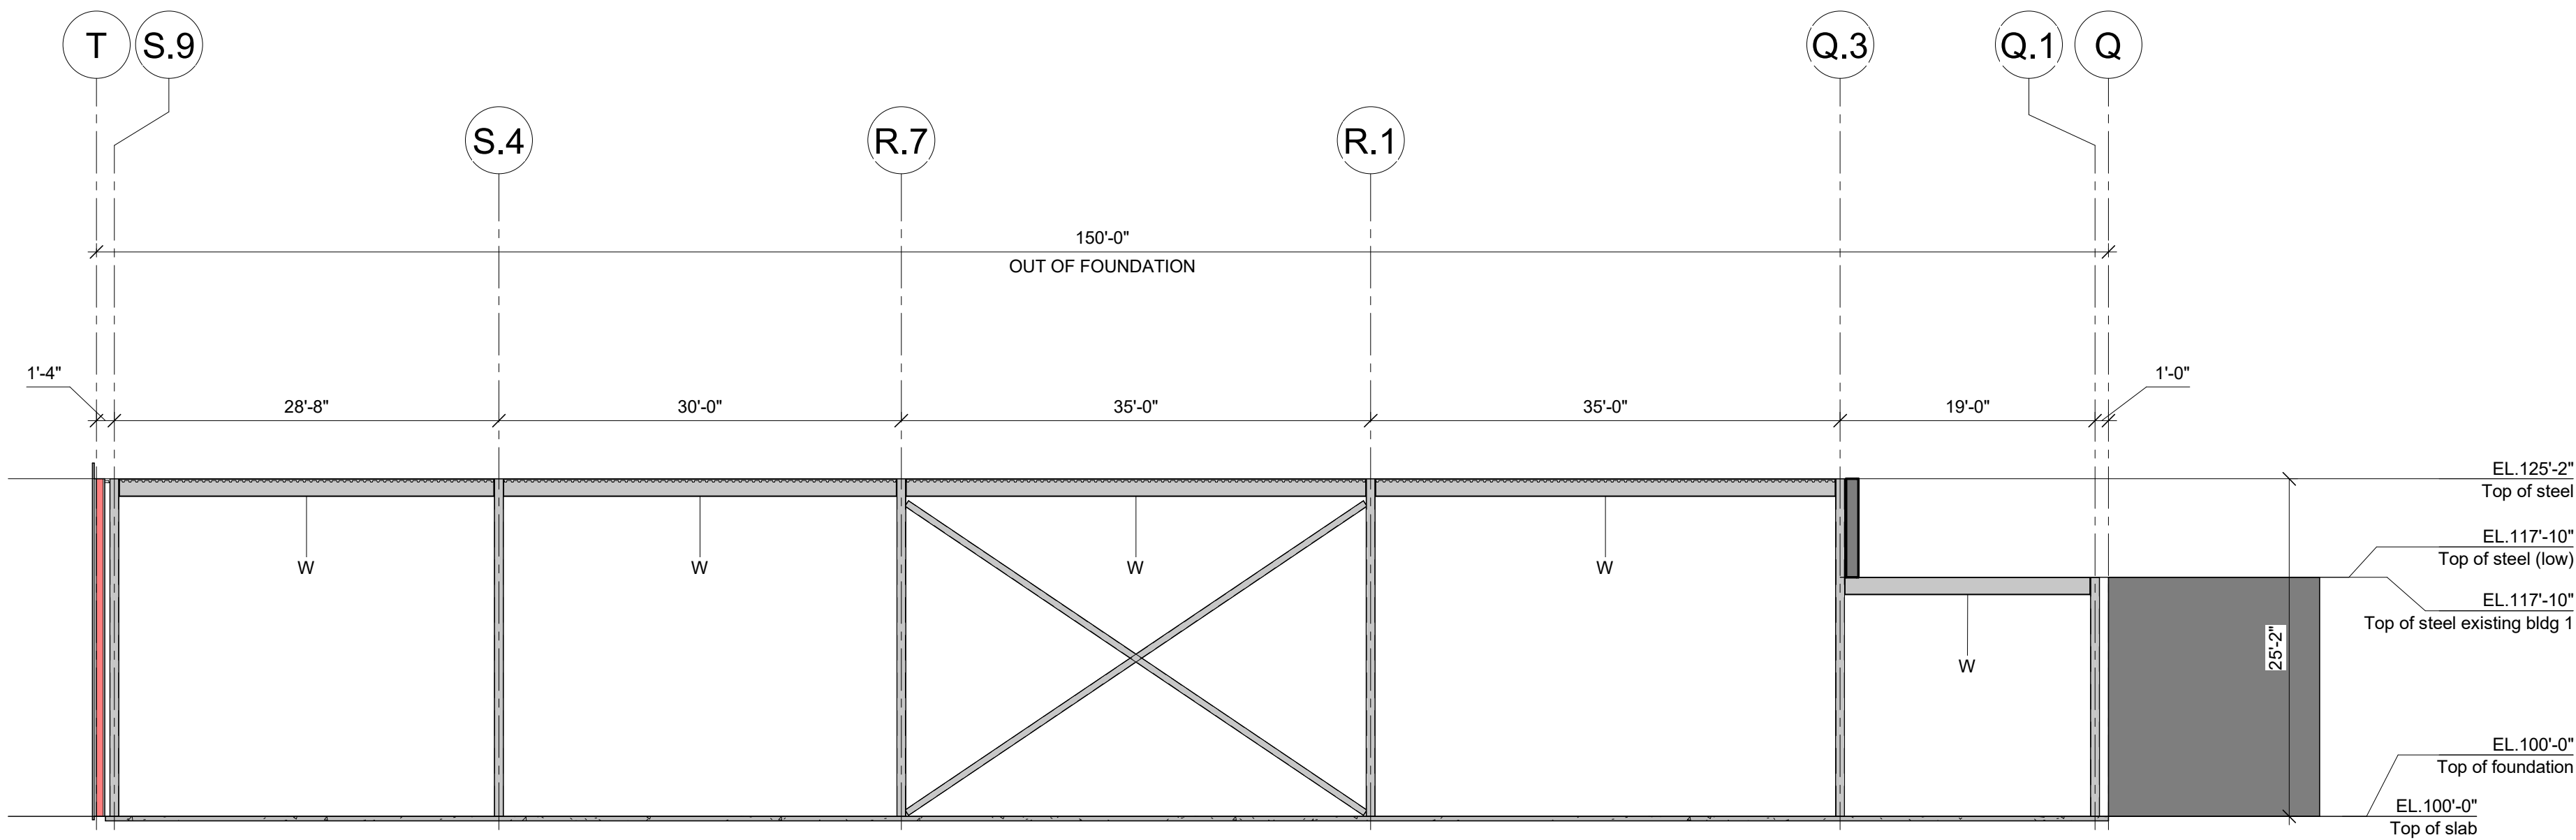

ELEVATION LINE 9.9 (STRUCTURE) (NORTH)
1" = 10'-0"

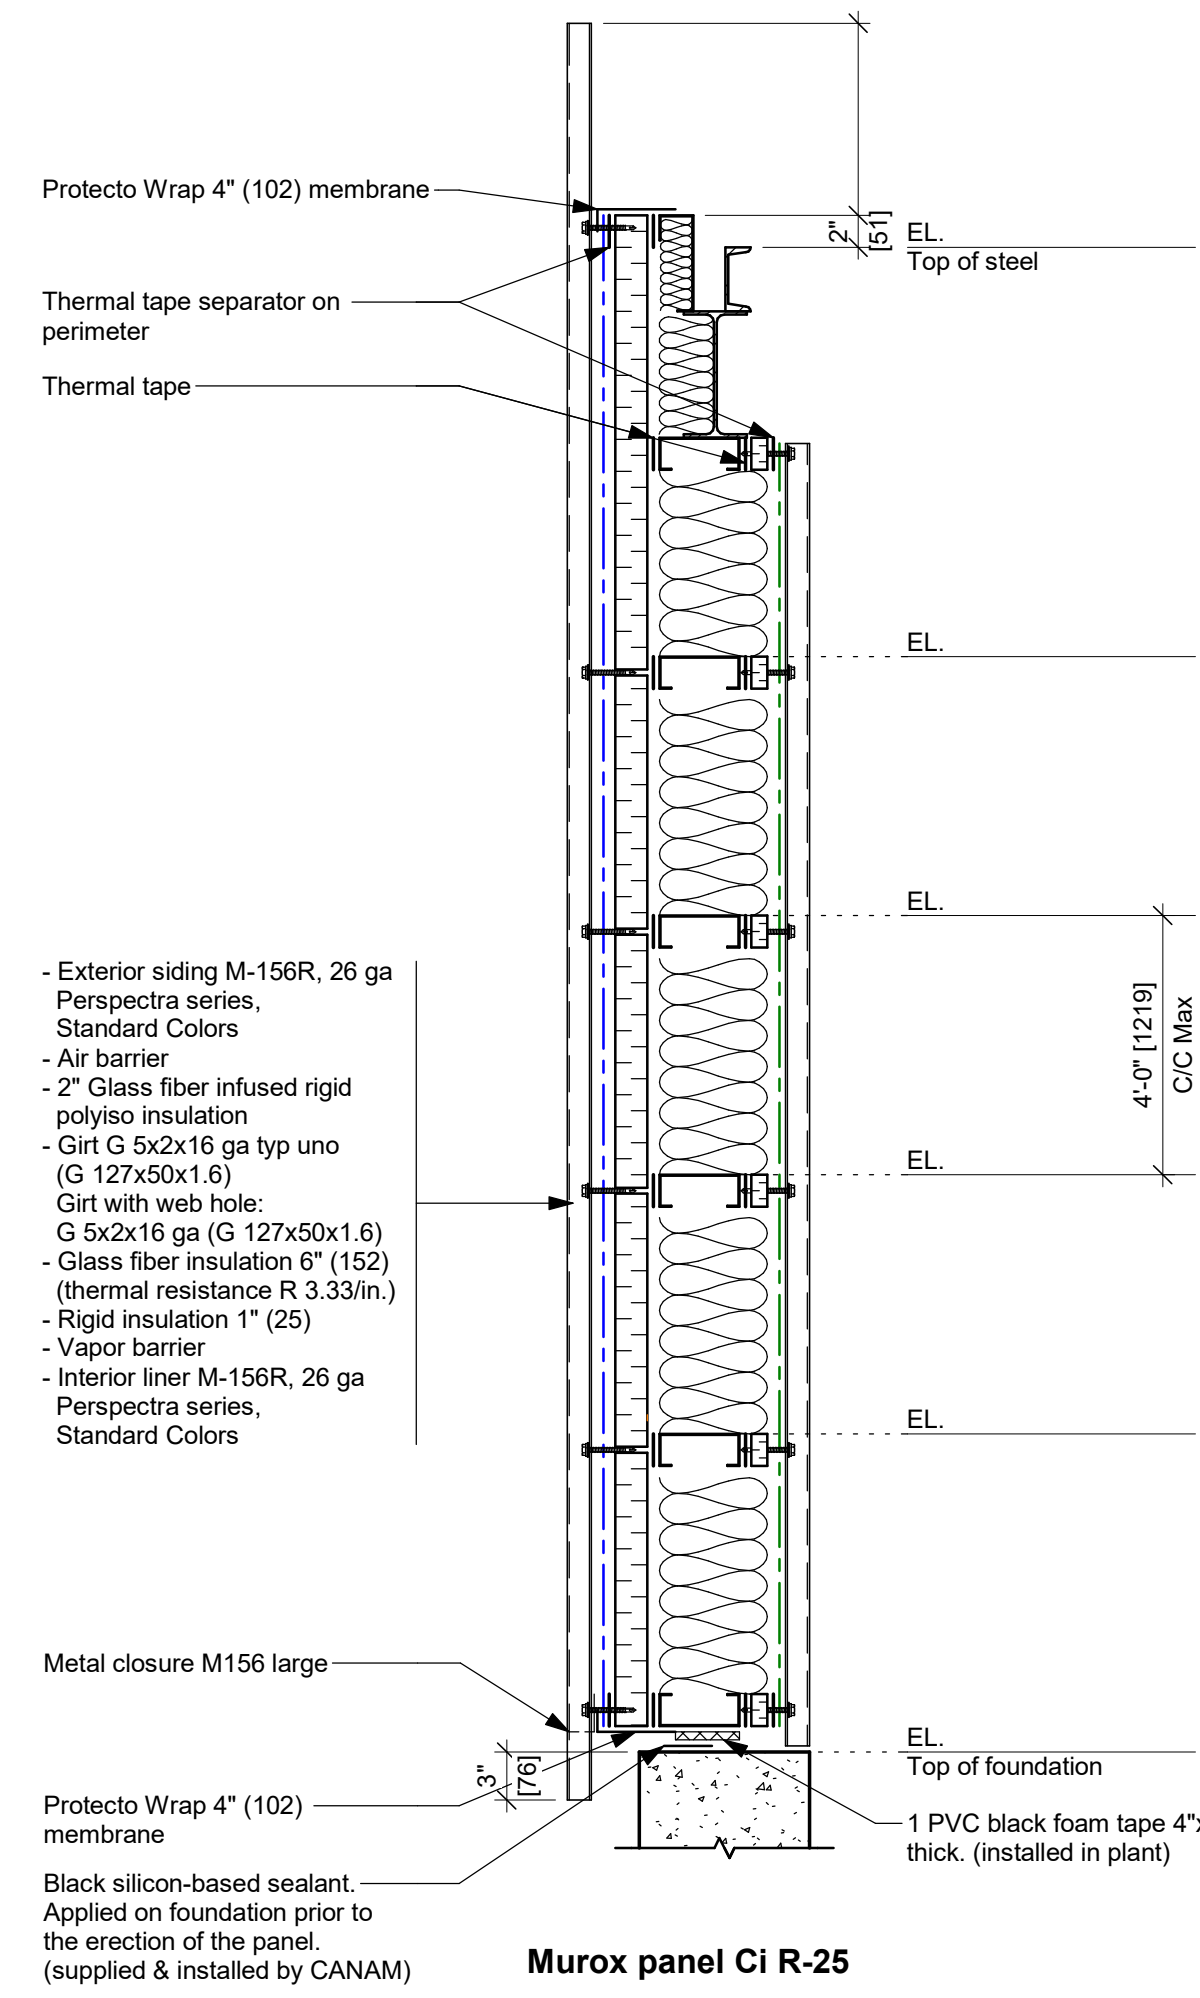


Murox panel CI R-25

PRELIMINARY

NOT TO BE USED FOR CONSTRUCTION

REVISION	DATE	DESCRIPTION	DESS	VER
PROJECT MANAGER				
-				
-				
-				
DRAFTING				
DRAWN		DESIGNED	PROJECT ENGINEER	SCALE
INITIAL				AS INDICATED
CHECKED	CONSULTING ENGINEERS / ARCHITECTS			DATE (yyyy/mm/dd)
				2028/02/24
CUSTOMER: J.S. MCCARTHY CO.				

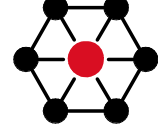	CANAM
28 Birch Street, Milford, Massachusetts, 01757, US Phone : (504) 571-3050 Toll Free : (866) 466-8769 www.canam.com	

PROFESSIONAL SEAL			
PROJECT			
ROLL WAREHOUSE ADDITION 15 DARIN DR. AUGUSTA, MAINE 04330			
DRAWING TITLE			
PRELIMINARY SKETCH - ELEVATION, WALL SECTION AND SCHEDULES			
CONTRACT NUMBER P2026-031	DRAWING NUMBER EsMx502	DIVISION	REVISION
			