


**REMOVING THIS PANEL
WILL REQUIRE
MODIFICATIONS TO
SUPPORT THE EXISTING
JOISTS (BY OTHERS)**

EXISTING
PANEL WALL TO
BE REMOVED


**EXISTING BUILDING
(TOS 125'-2")**

**EXISTING BUILDING
(TOS 117'-10")**

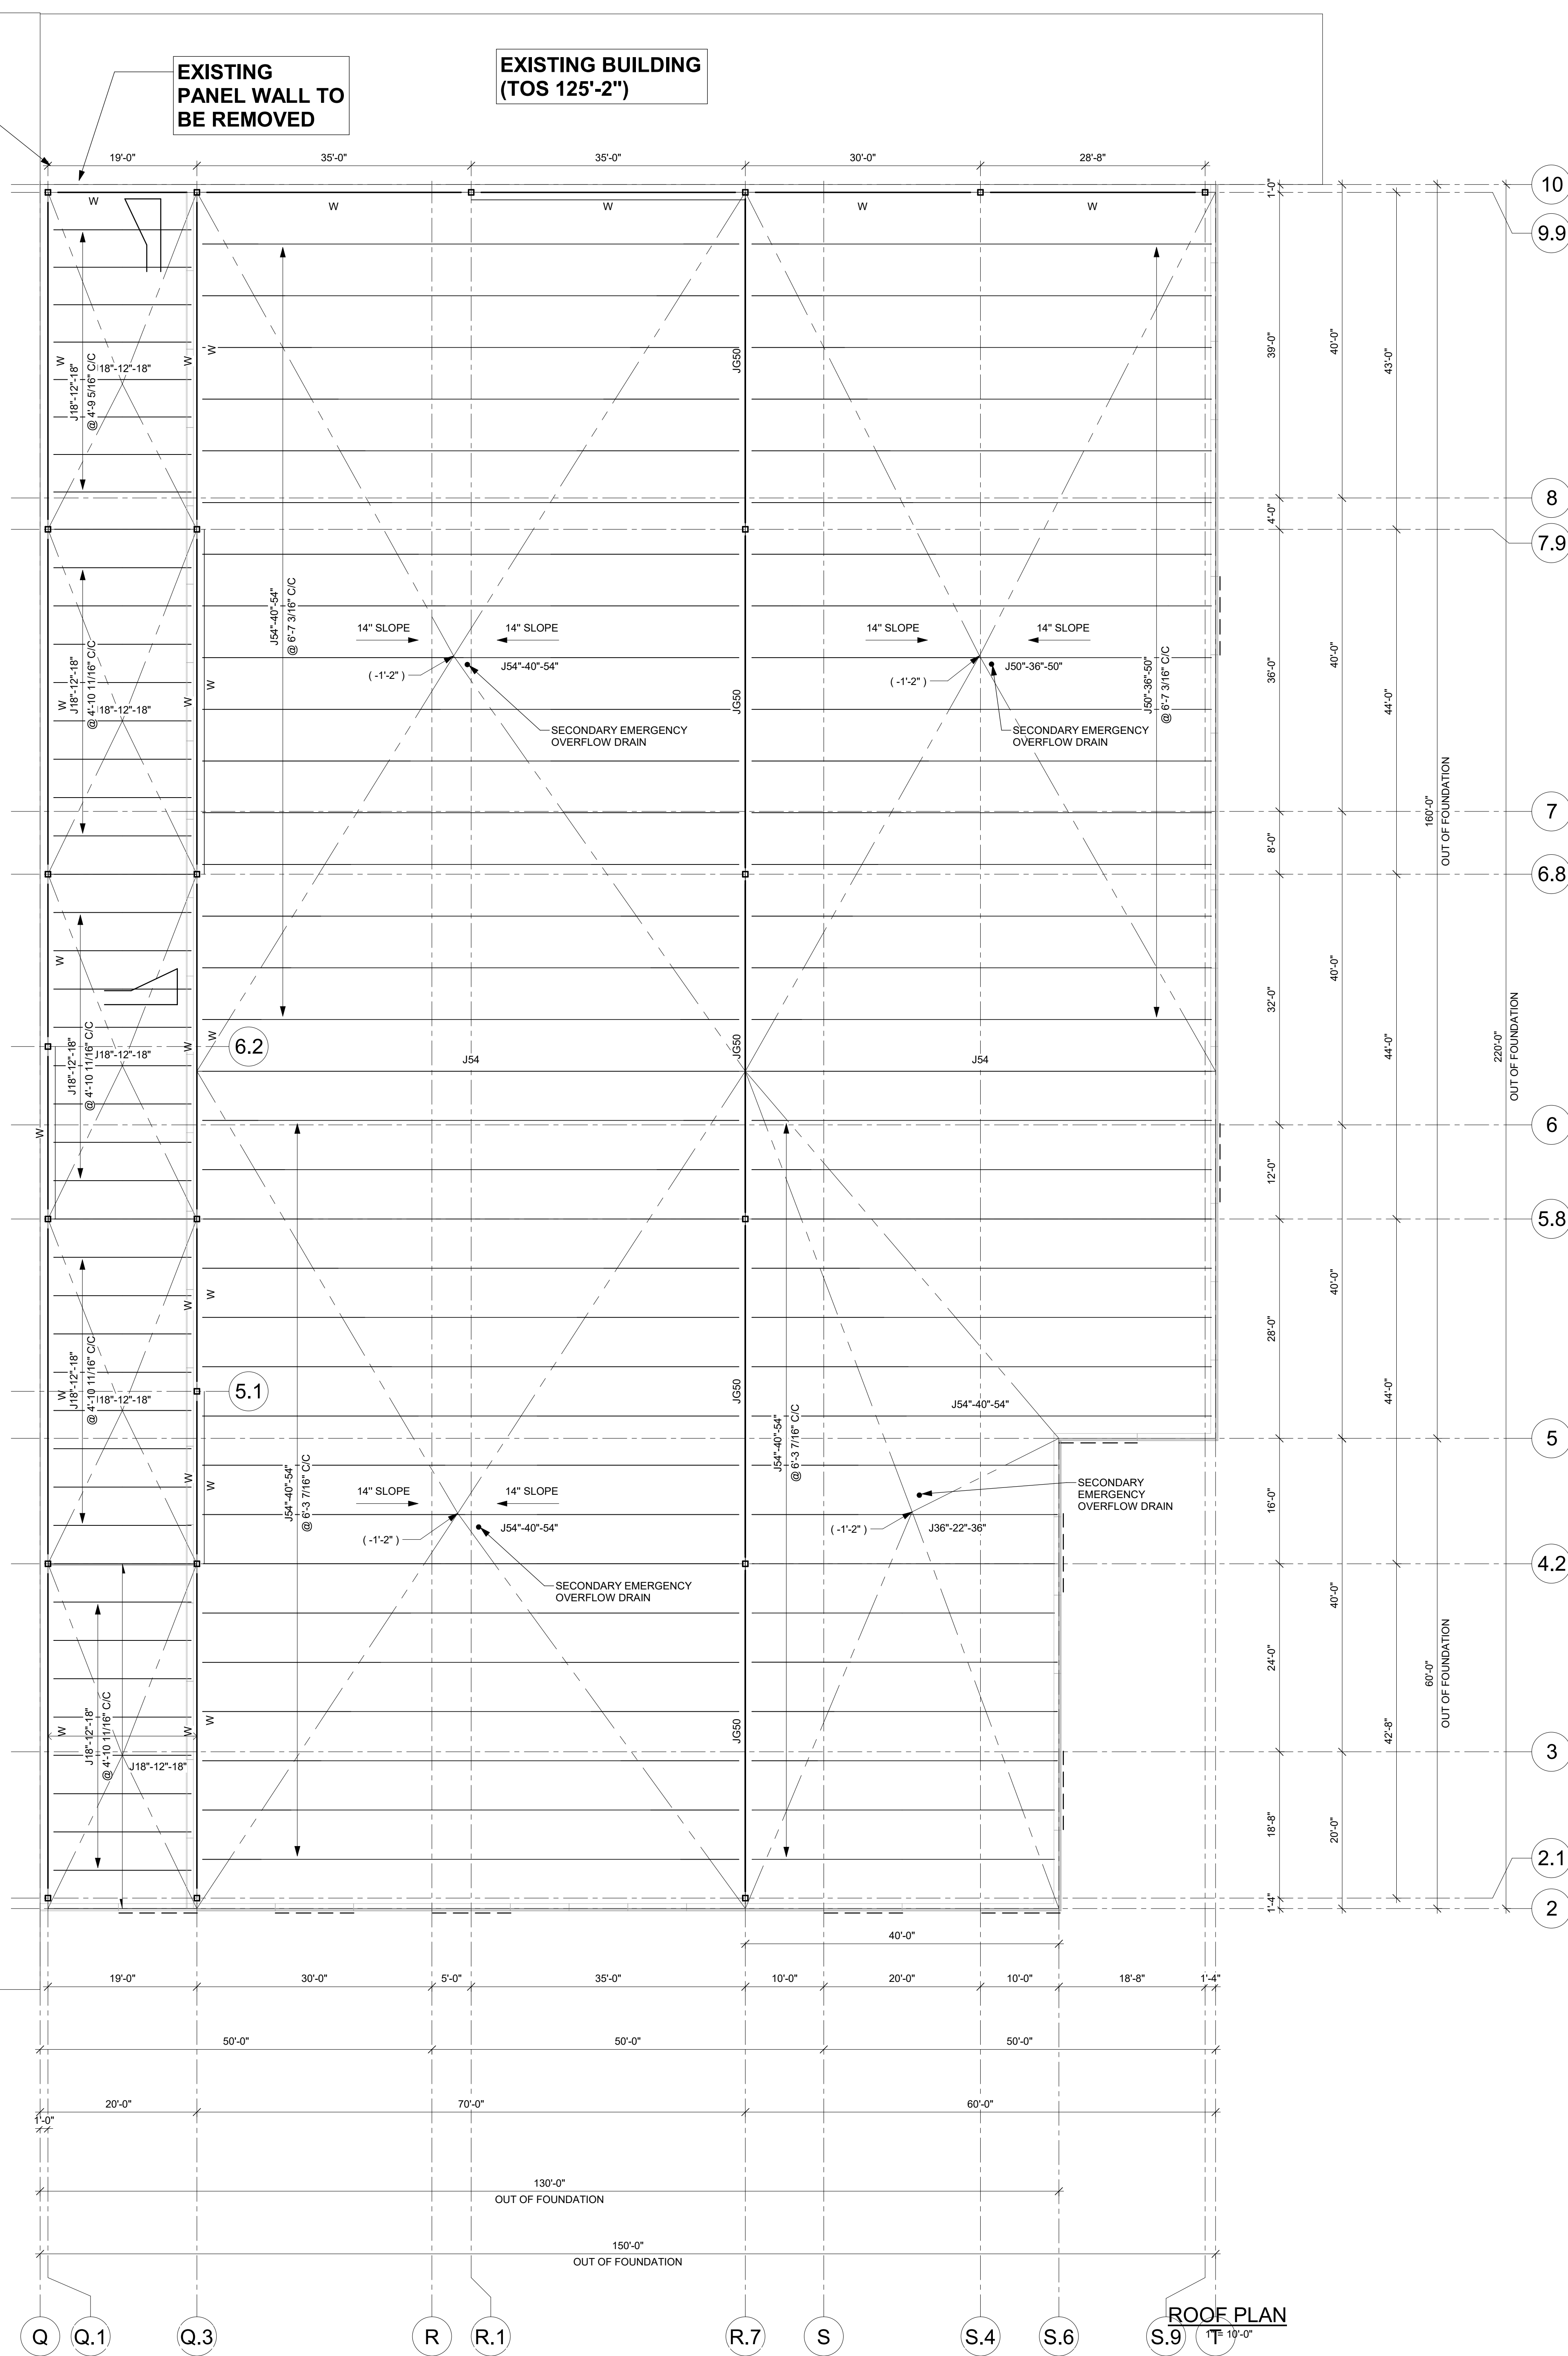


ROOF PLAN

GROSS UPLIFT DIAGRAM (UNFACTORED)

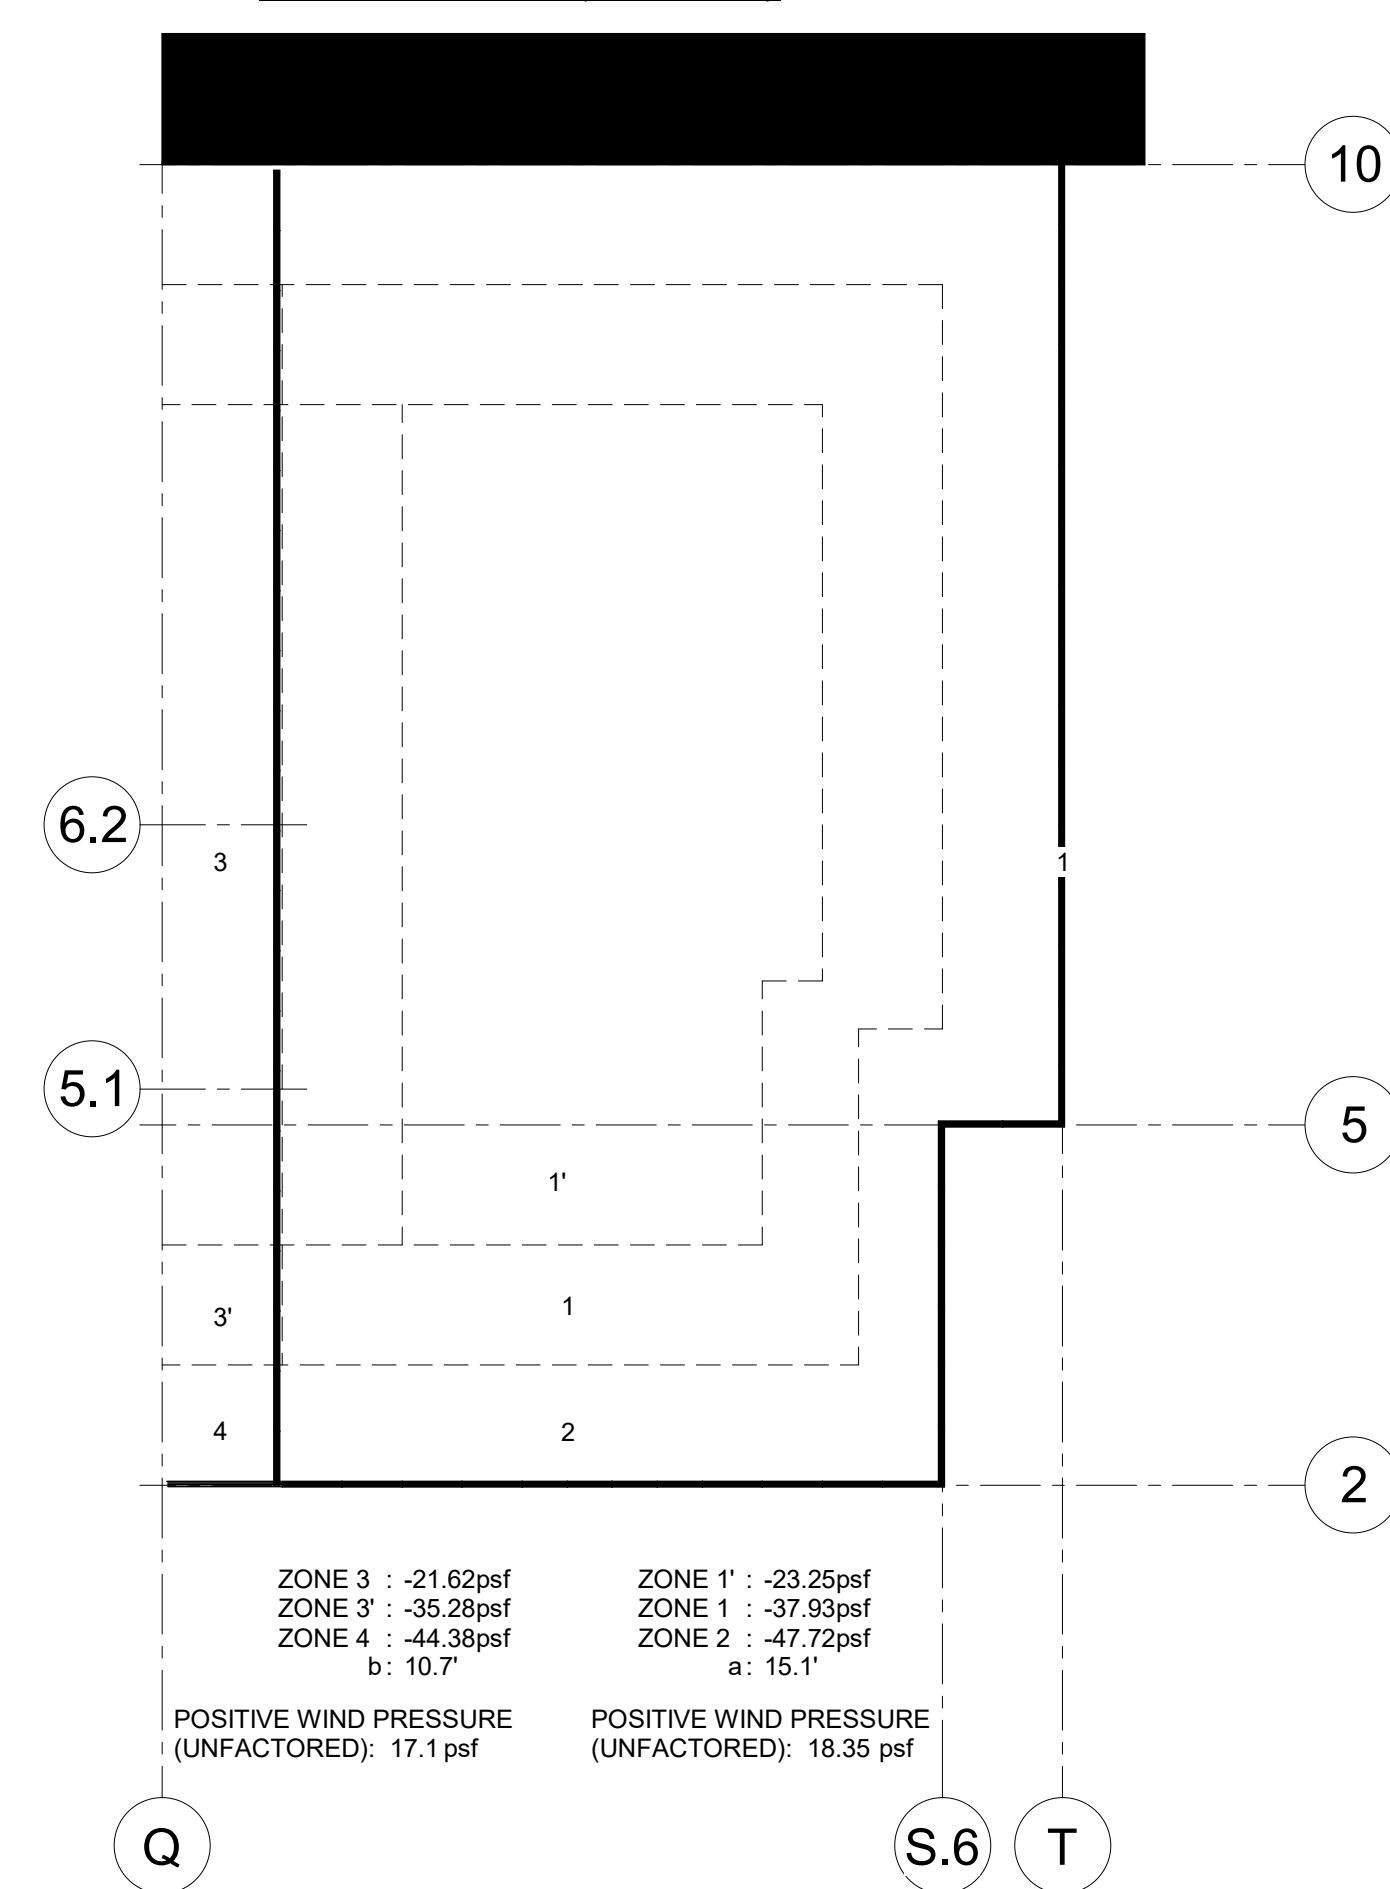

SNOW LOAD ACCUMULATION

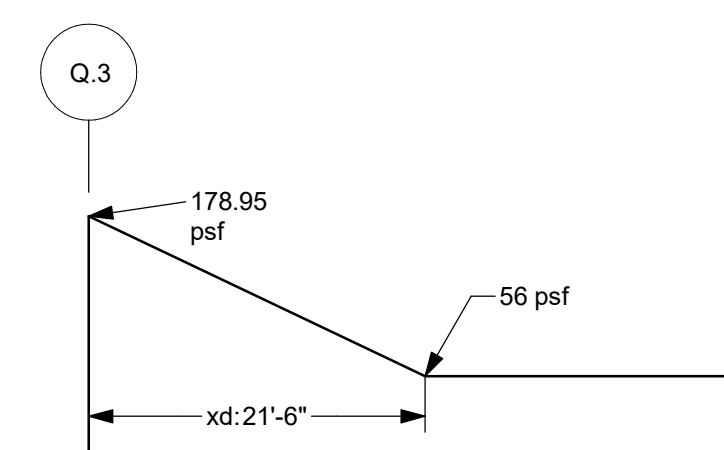

SNOW LOAD ACCUMULATION

