




Scale

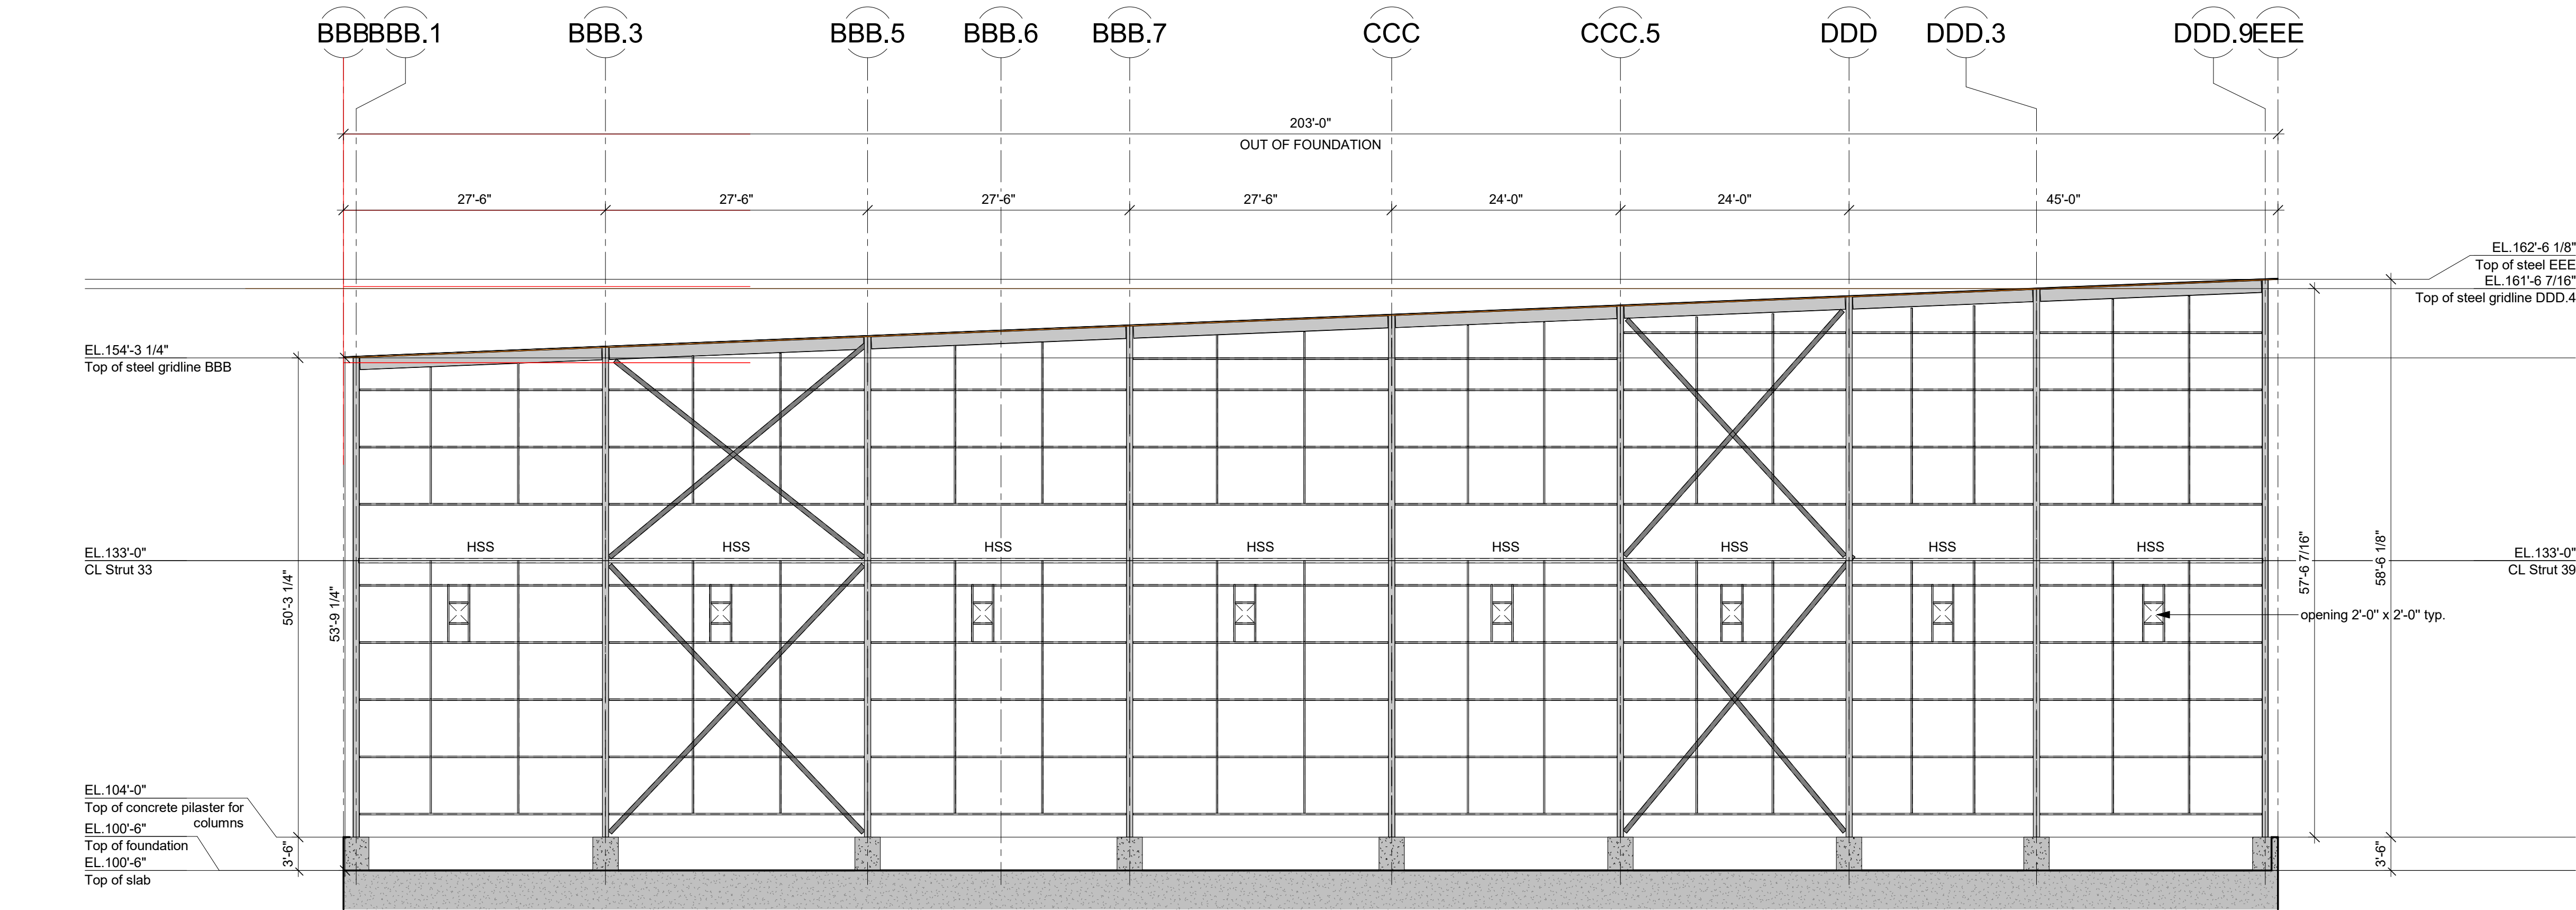


ELEVATION LINE 902 (SOUTH)
3/32" = 1'-0"

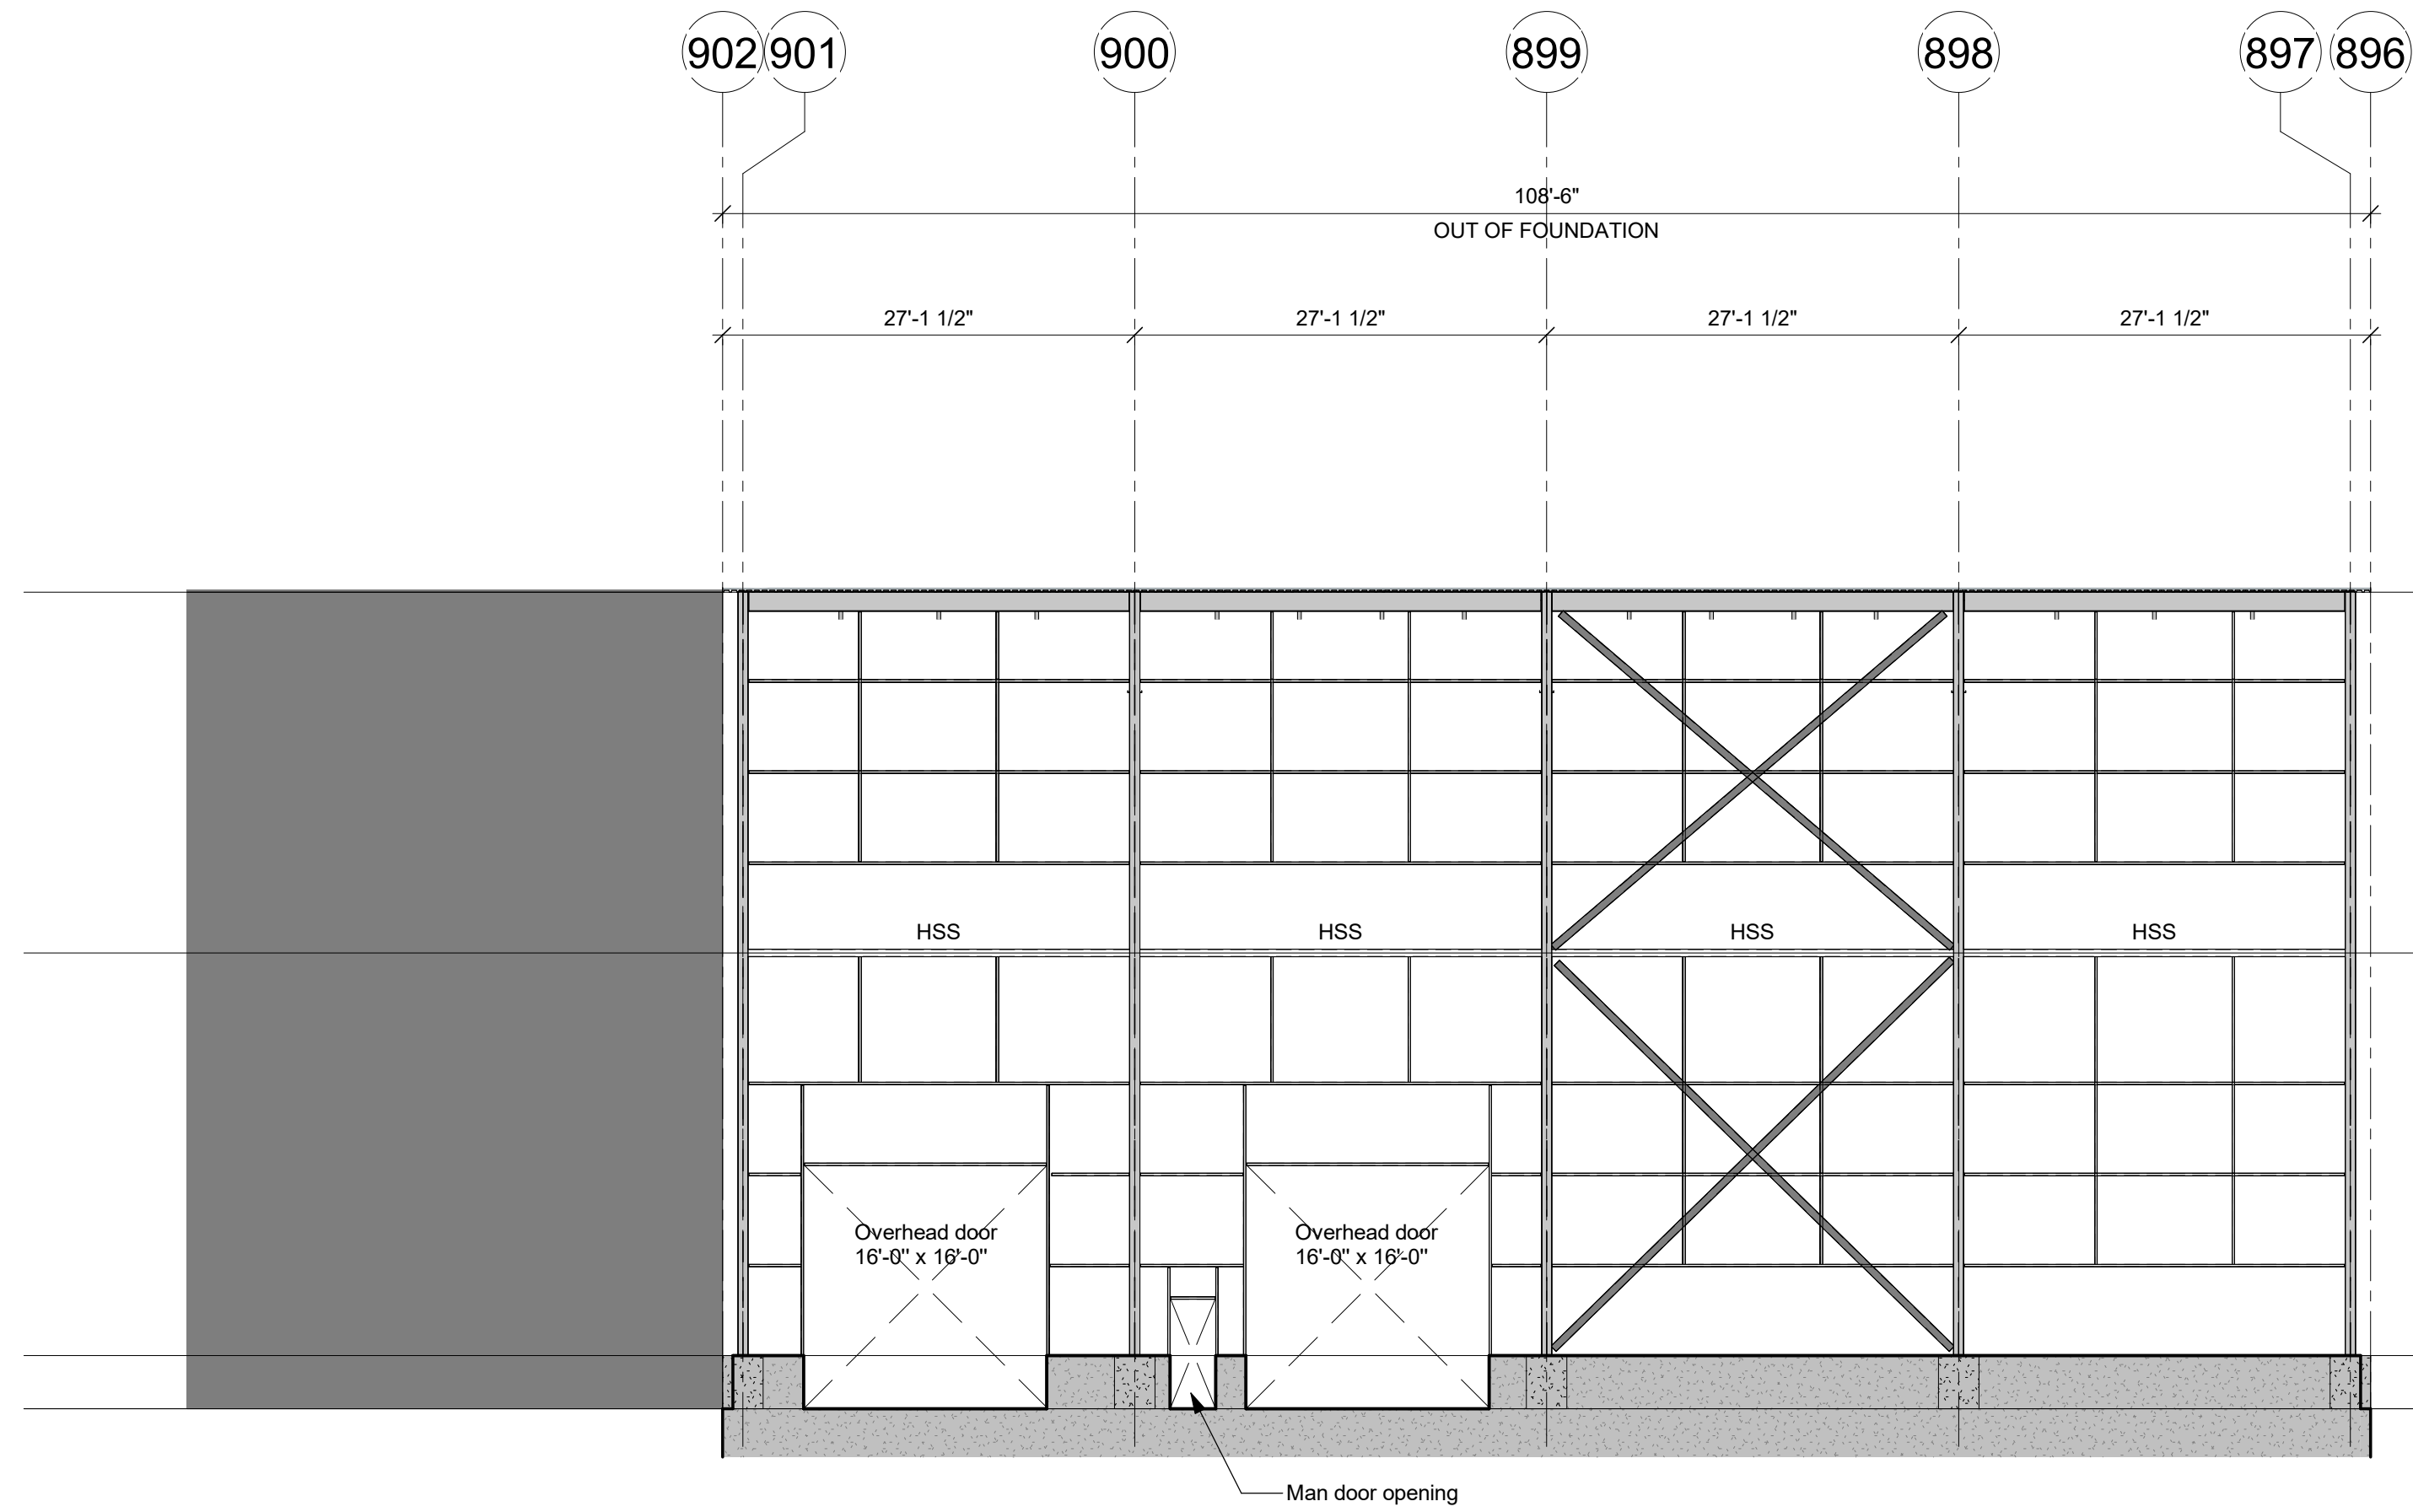

ELEVATION LINE BBB (WEST)
3/32" = 1'-0"

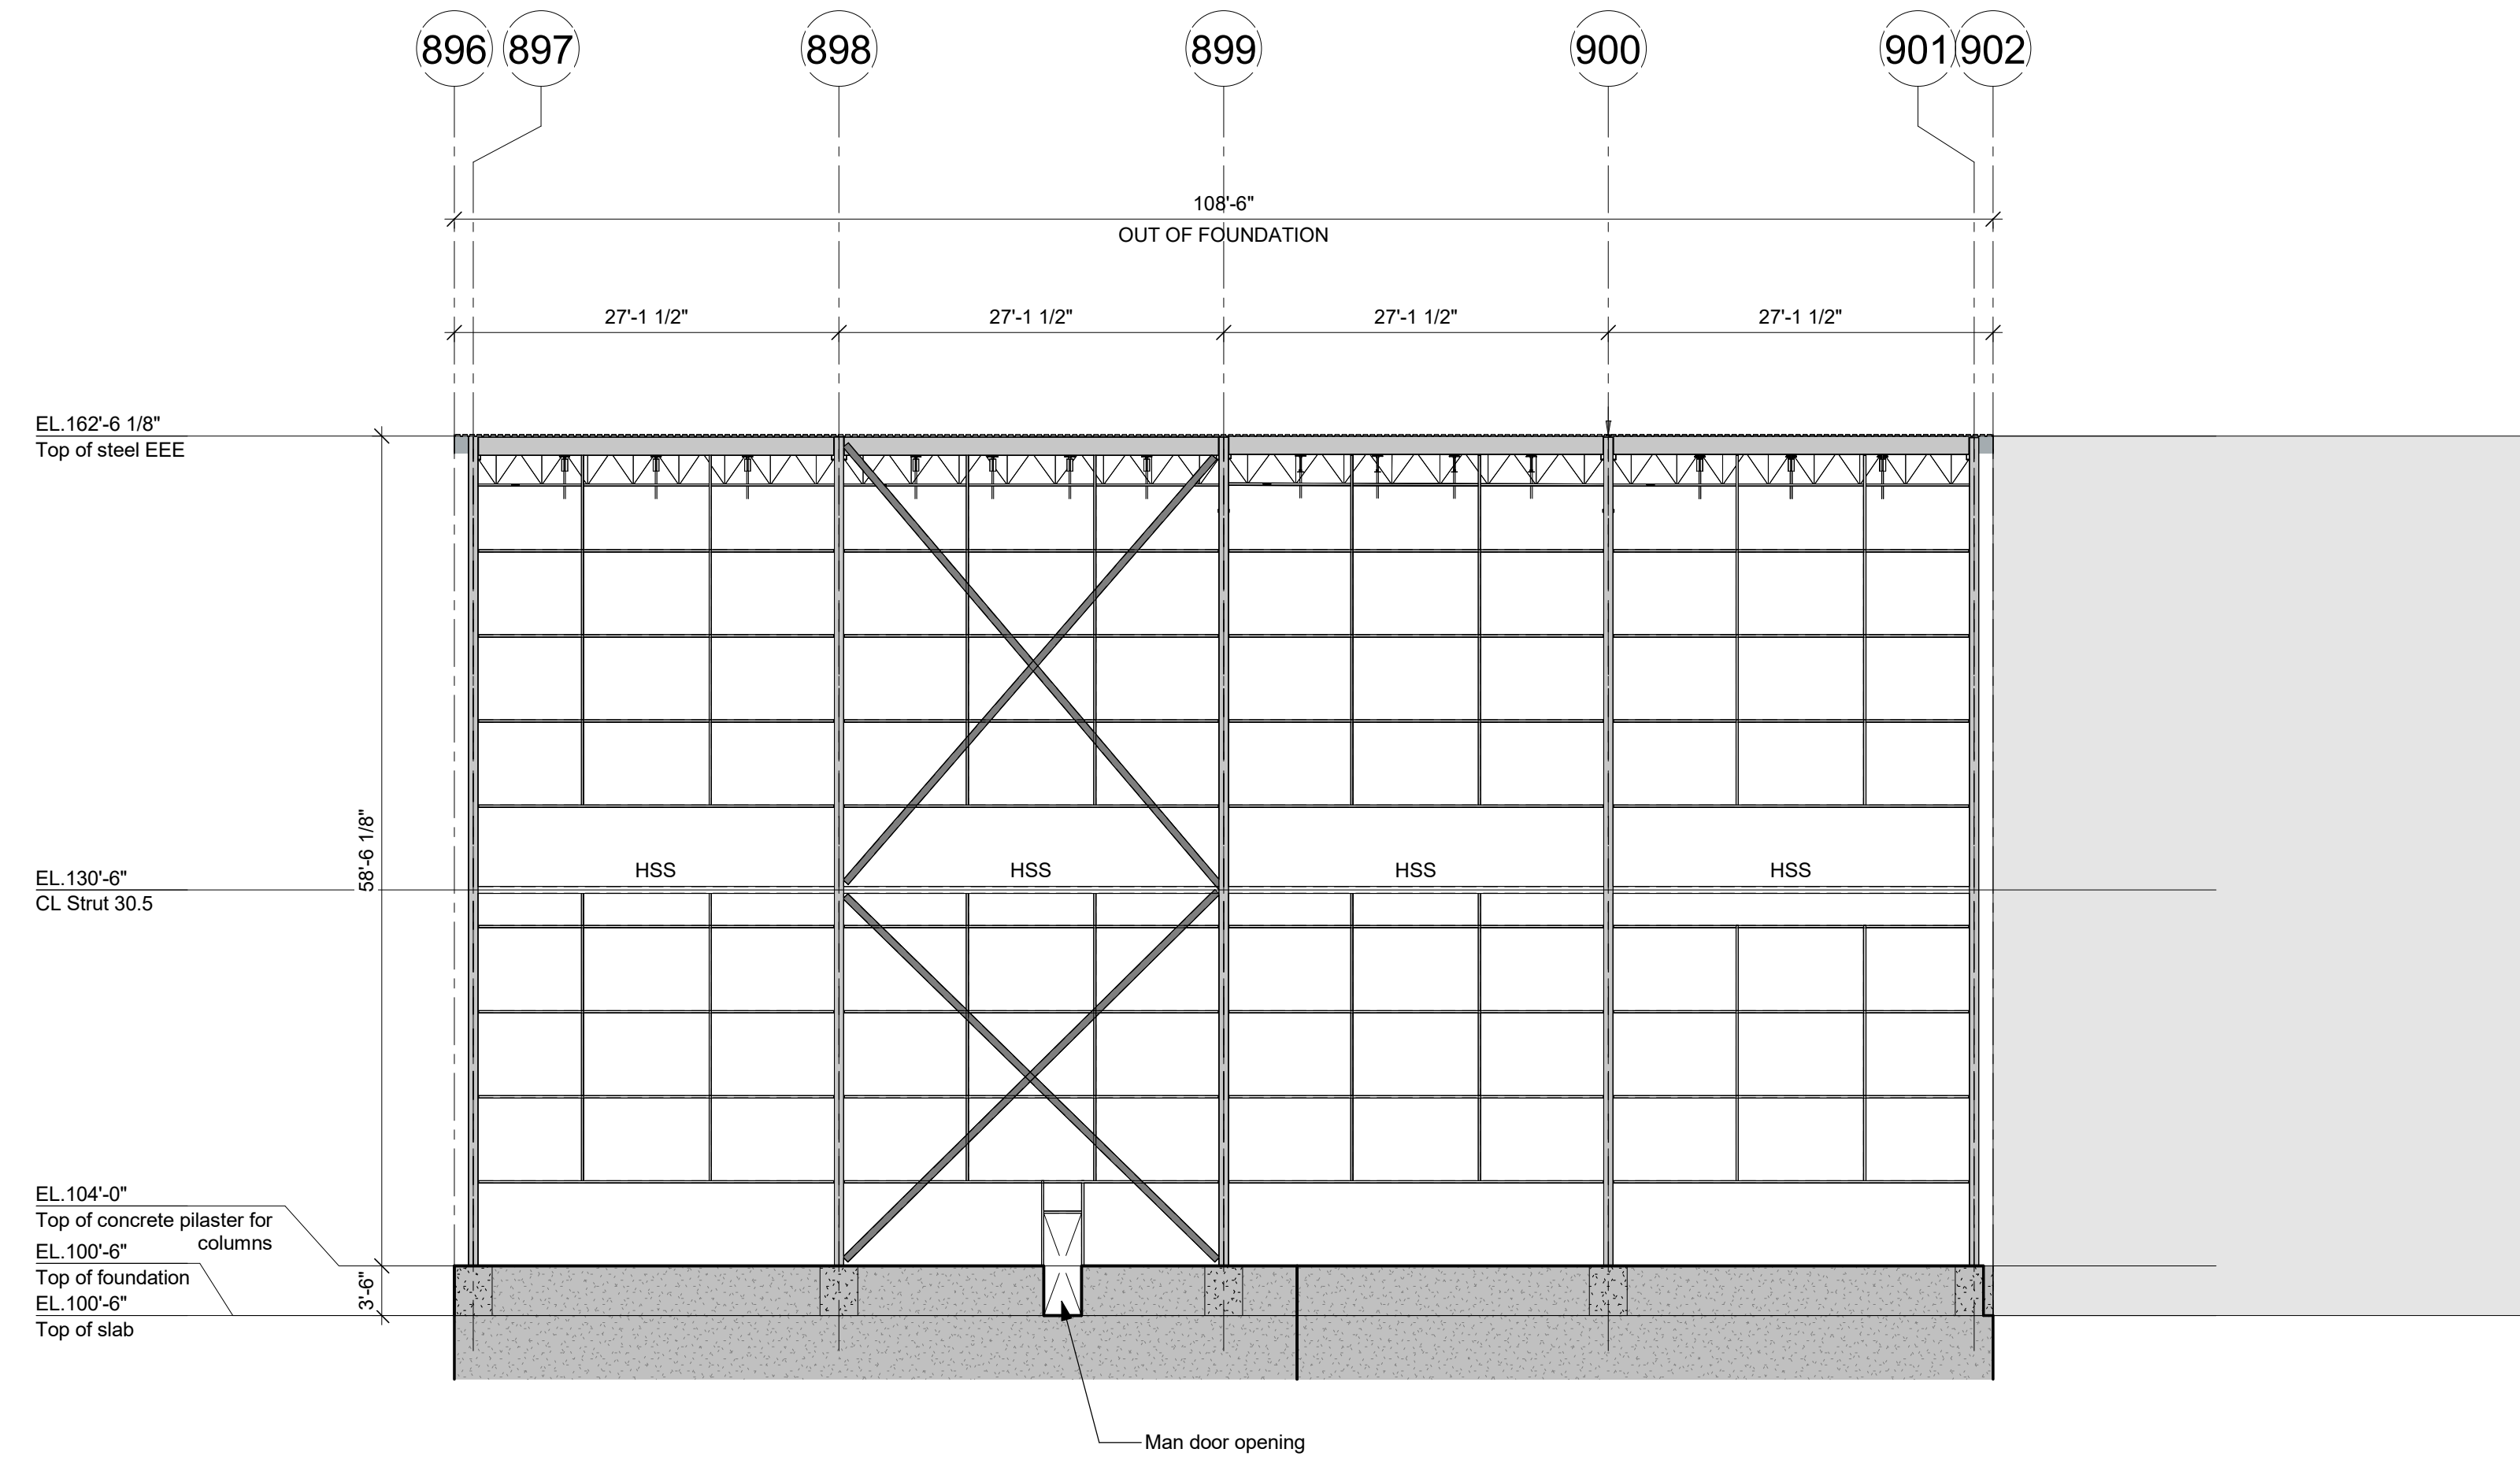

ELEVATION LINE EEE (EAST)
3/32" = 1'-0"

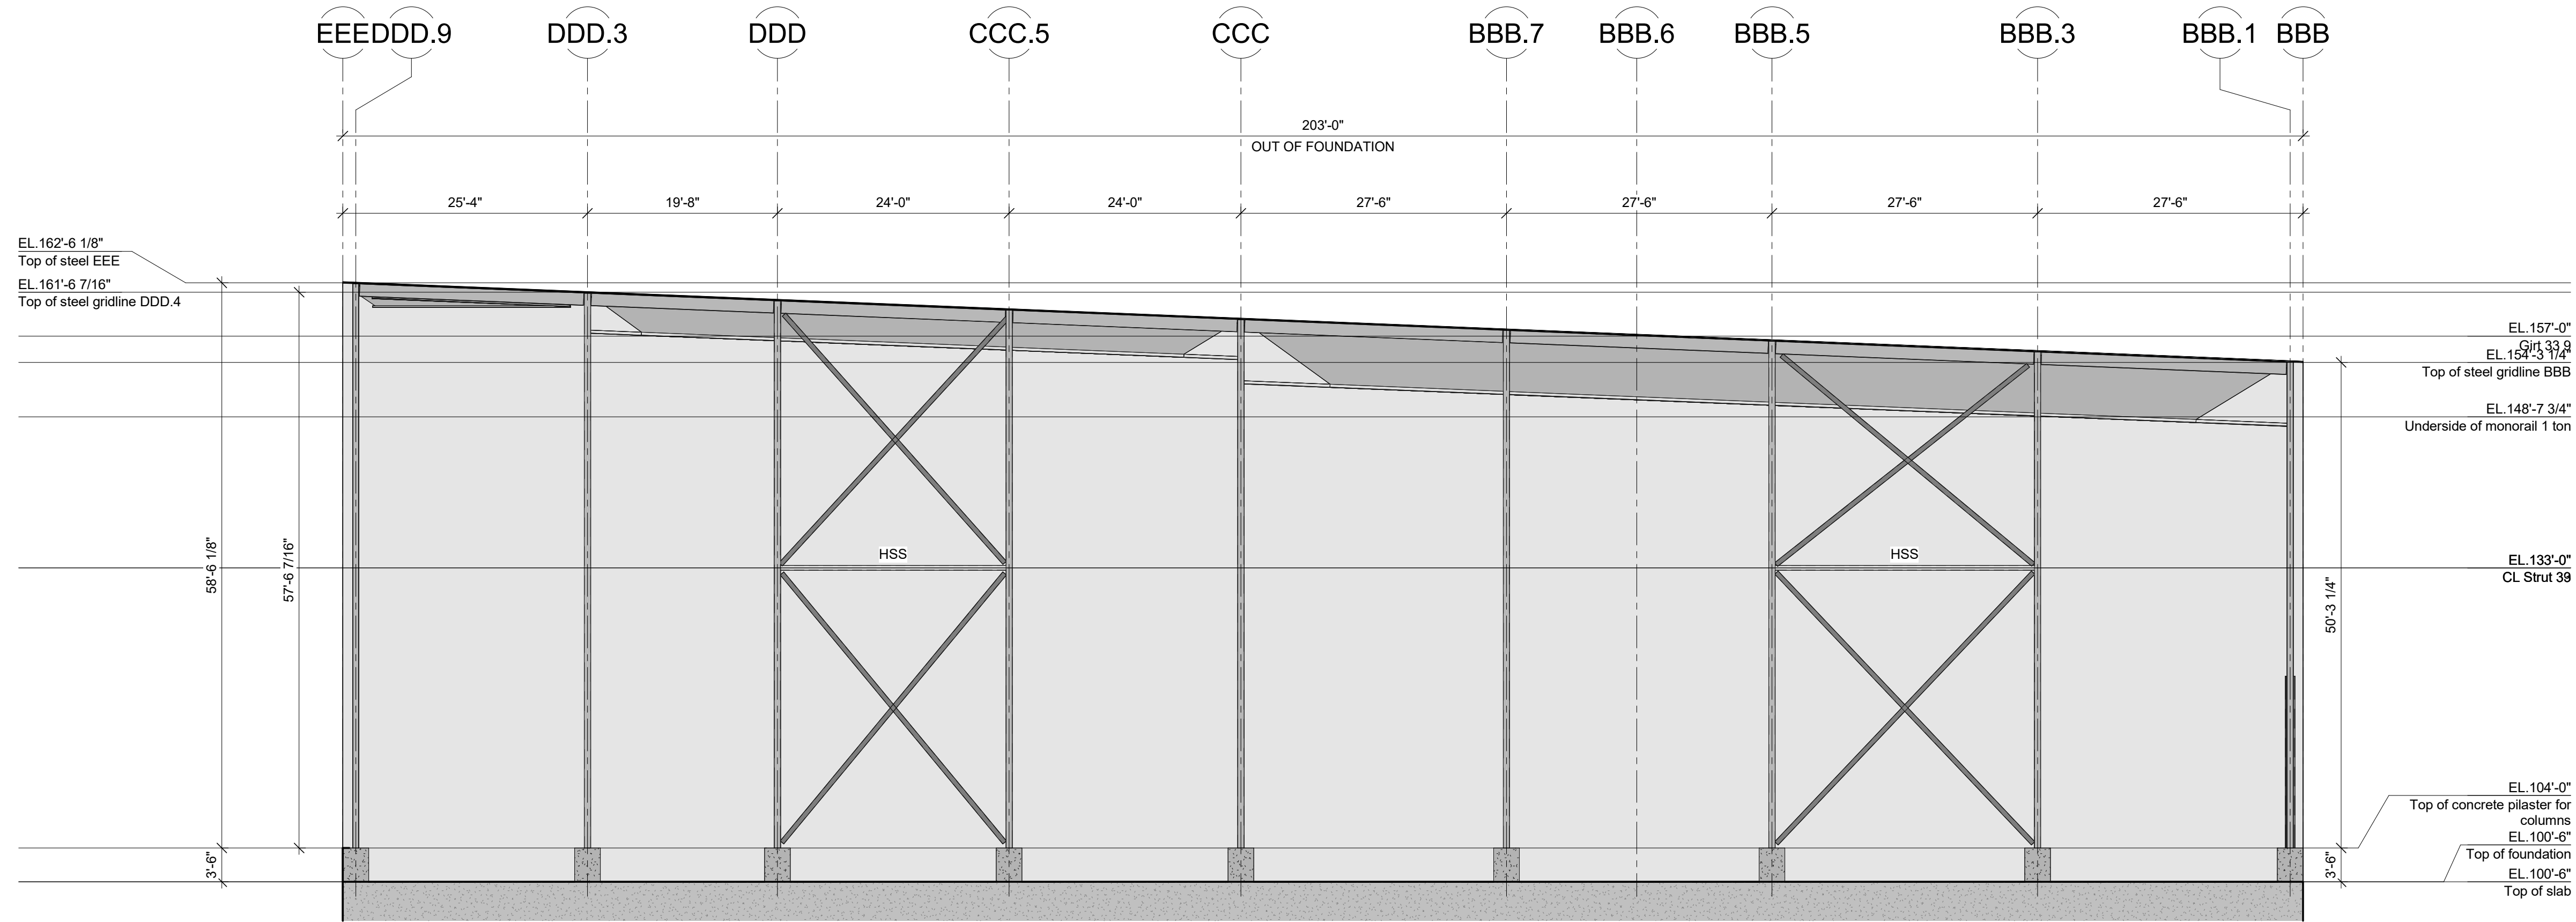

ELEVATION LINE 907 & 910 (NORTH)
3/32" = 1'-0"

CONTRACTOR/RECTOR NOTE:
IT IS PROHIBITED TO MODIFY, COPY, REPRODUCE OR OTHERWISE
DISTRIBUTE THIS DRAWING OR ANY REPRESENTATION OF THIS
DRAWING, OR ANY MEDIA, INCLUDING ELECTRONIC, WITHOUT THE
PRIOR WRITTEN APPROVAL OF CANAM GROUP INC.

PRELIMINARY

NOT TO BE USED FOR CONSTRUCTION

REVISION	DATE	DESCRIPTION	ISS	VER
PROJECT MANAGER				

DRAFTING			
DRAWN	DESIGNED	PROJECT ENGINEER	SCALE
Donald Piché			3/32" = 1'-0"
CHECKED	CONSULTING ENGINEERS ARCHITECTS		DATE (yyyy/mm/dd)
			2025-02-10

CUSTOMER: Fws Industrial Project Ltd

CANAM
11505, 1re Avenue, bureau 500, Saint-Georges Beauce
Québec, Canada, G5V 7X3
Phone : (418) 228-8031
Toll free : (877) 499-6049
www.canam.com

PROFESSIONAL SEAL

PROJECT
Strong Pine- Hanson Lake Phase 3
Hanson Lake, SK

DRAWING TITLE
PRELIMINARY SKETCH - ELEVATIONS

CONTRACT NUMBER	DRAWING NUMBER	DIVISION	REVISION
P2029-034	EsMx501		

Initials

