
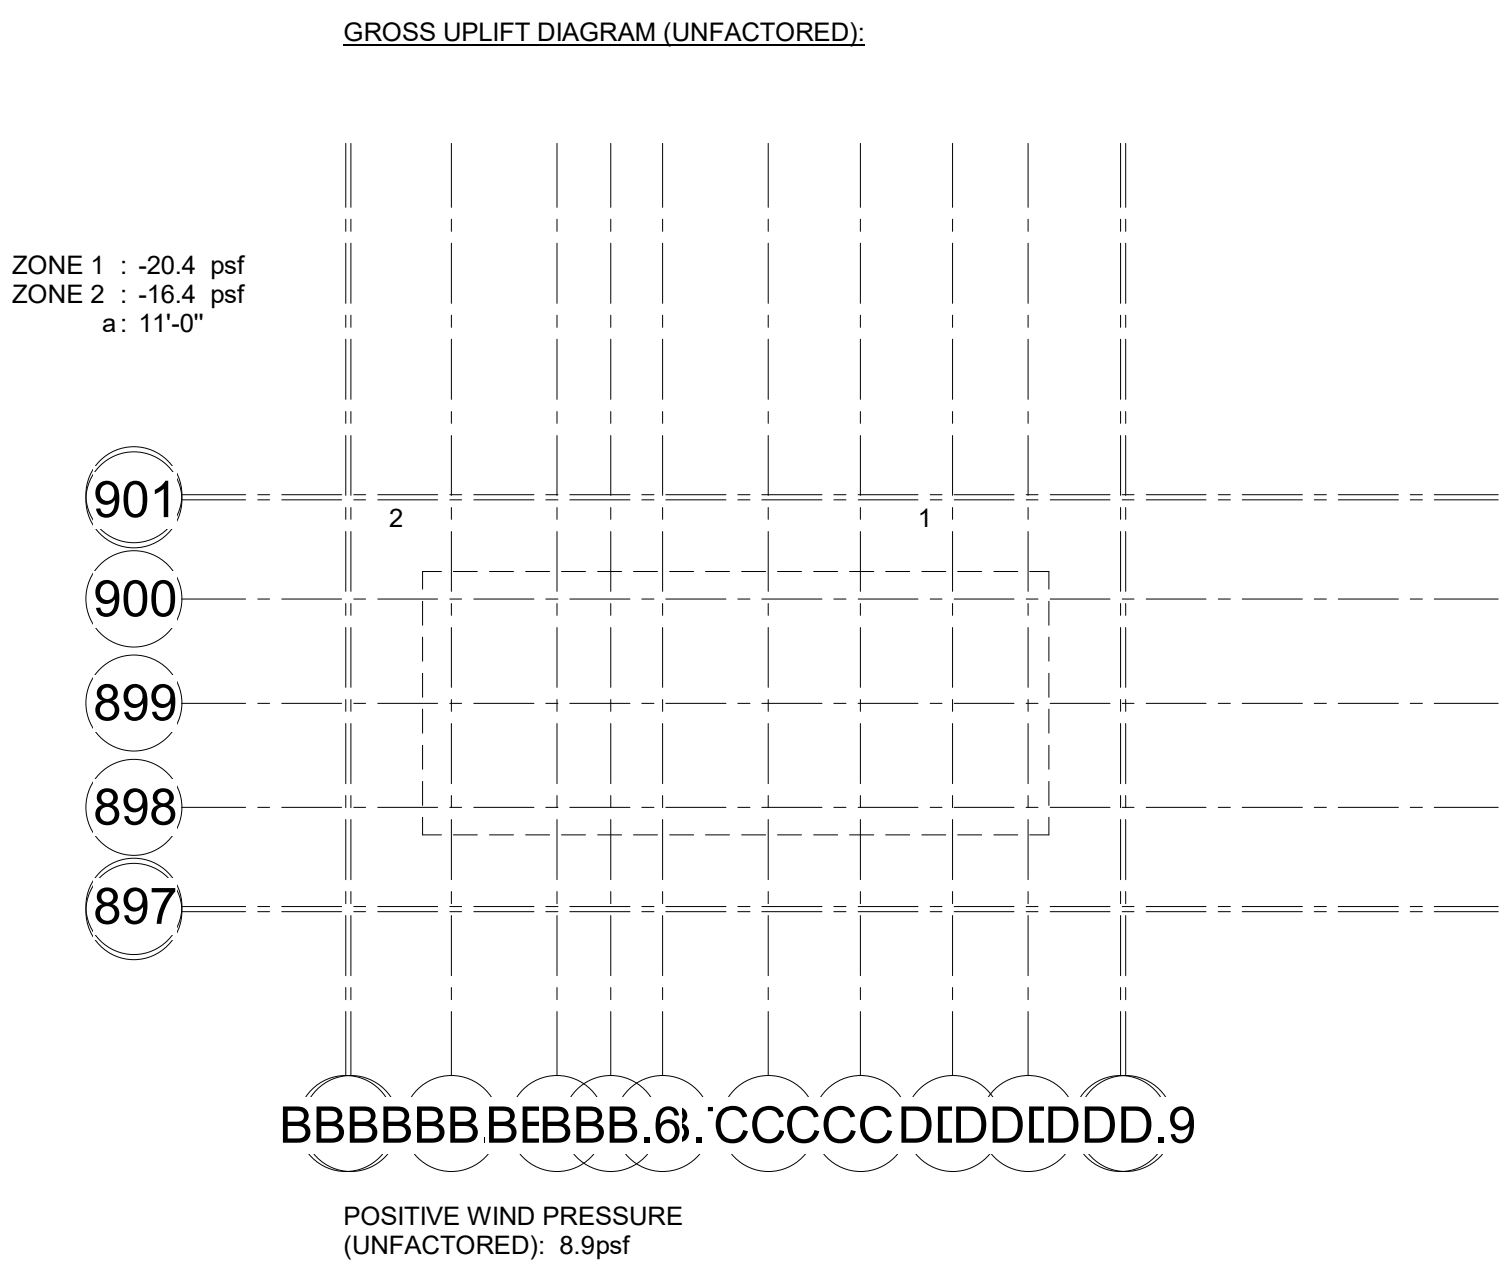


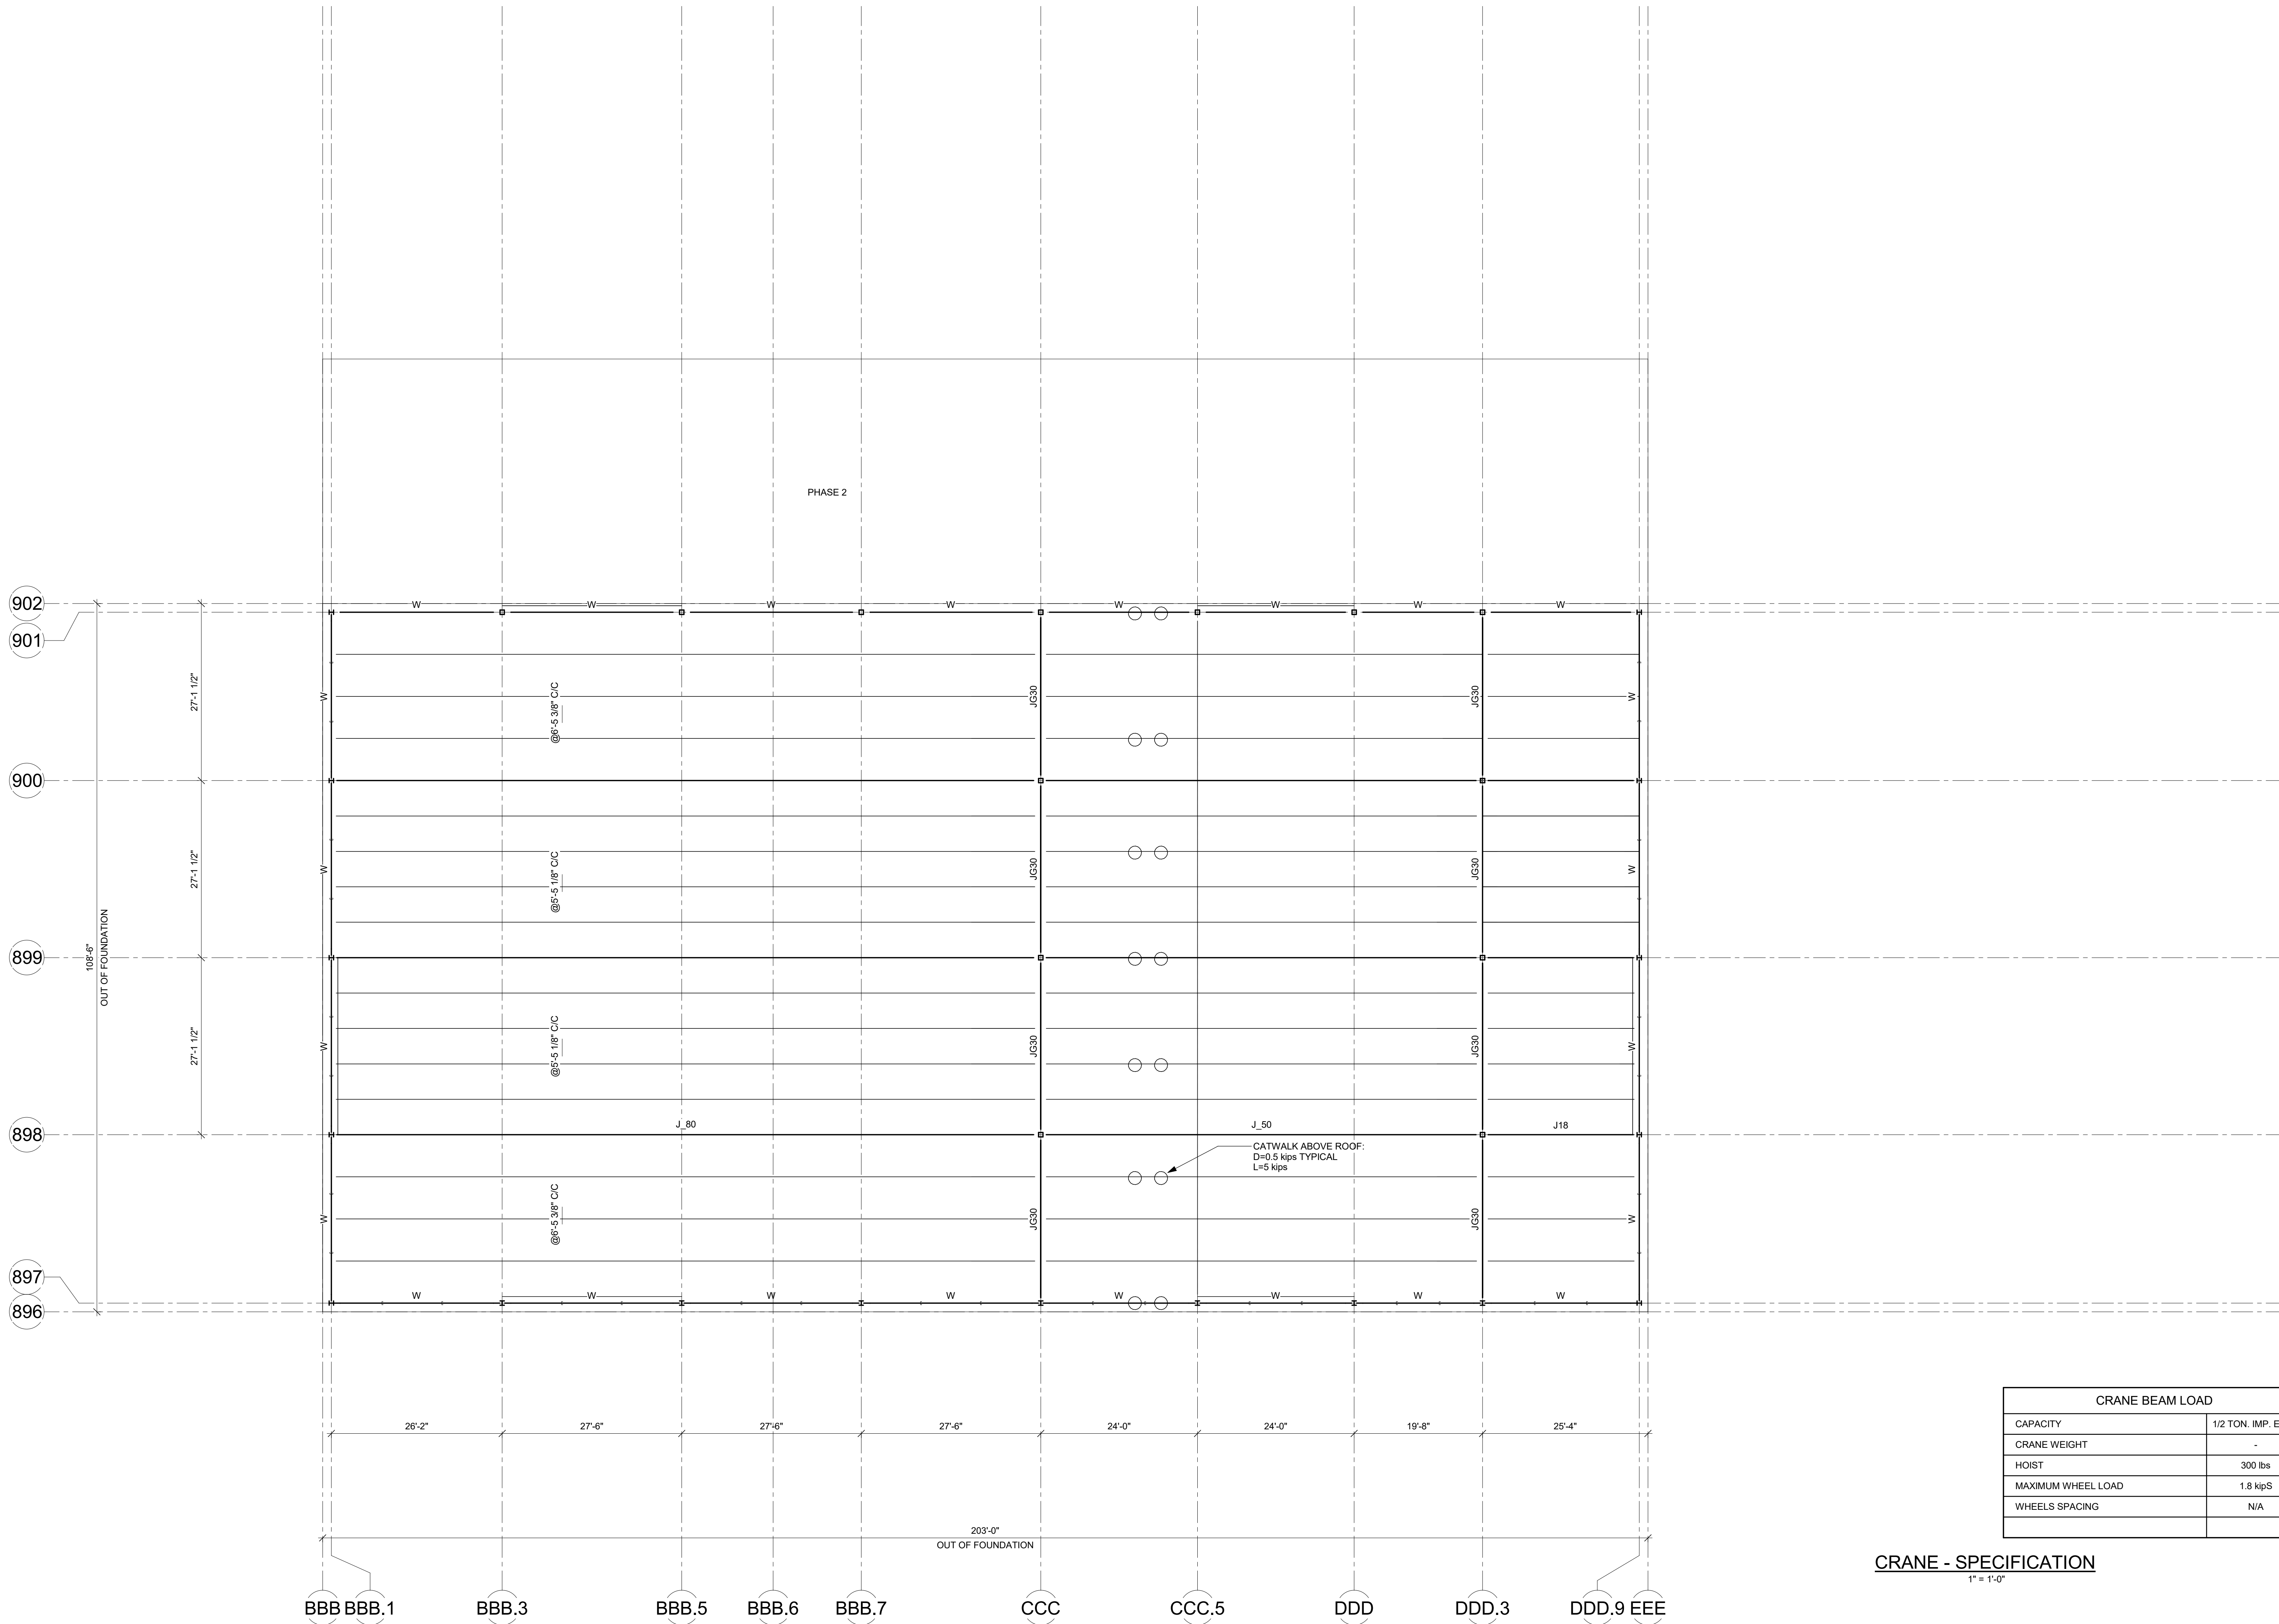

CRANE BEAM LOAD	
CAPACITY	1/2 TON, IMP. EACH
CRANE WEIGHT	-
HOIST	300 lbs
MAXIMUM WHEEL LOAD	1.8 kipS
WHEELS SPACING	N/A

CRANE - SPECIFICATION
1" = 1'-0"

ROOF PLAN
3/32" = 1'-0"