



DOOR SCHEDULE			
Identity	Qty.	Door 18 ga. Dimensions	Remarks
D1	2	36" x 84"	
D2	3	18'-2" x 23'	

Supplier's standard hardware:
- Hinges : Stanley F80179 4.5" x 4"
- Exit device : Von Duprin 22 x 689 with outside trim 230L
- Permanent cylinder : Schlage 2000IC 626
- Door closure : LCN 1381 689
- Head and jamb seal : Unique 1650
- Bottom seal : Unique D54
- Threshold : See the remarks in "Door schedule"


SUPPLIER'S STD HARDWARE
1/2" = 1'-0"

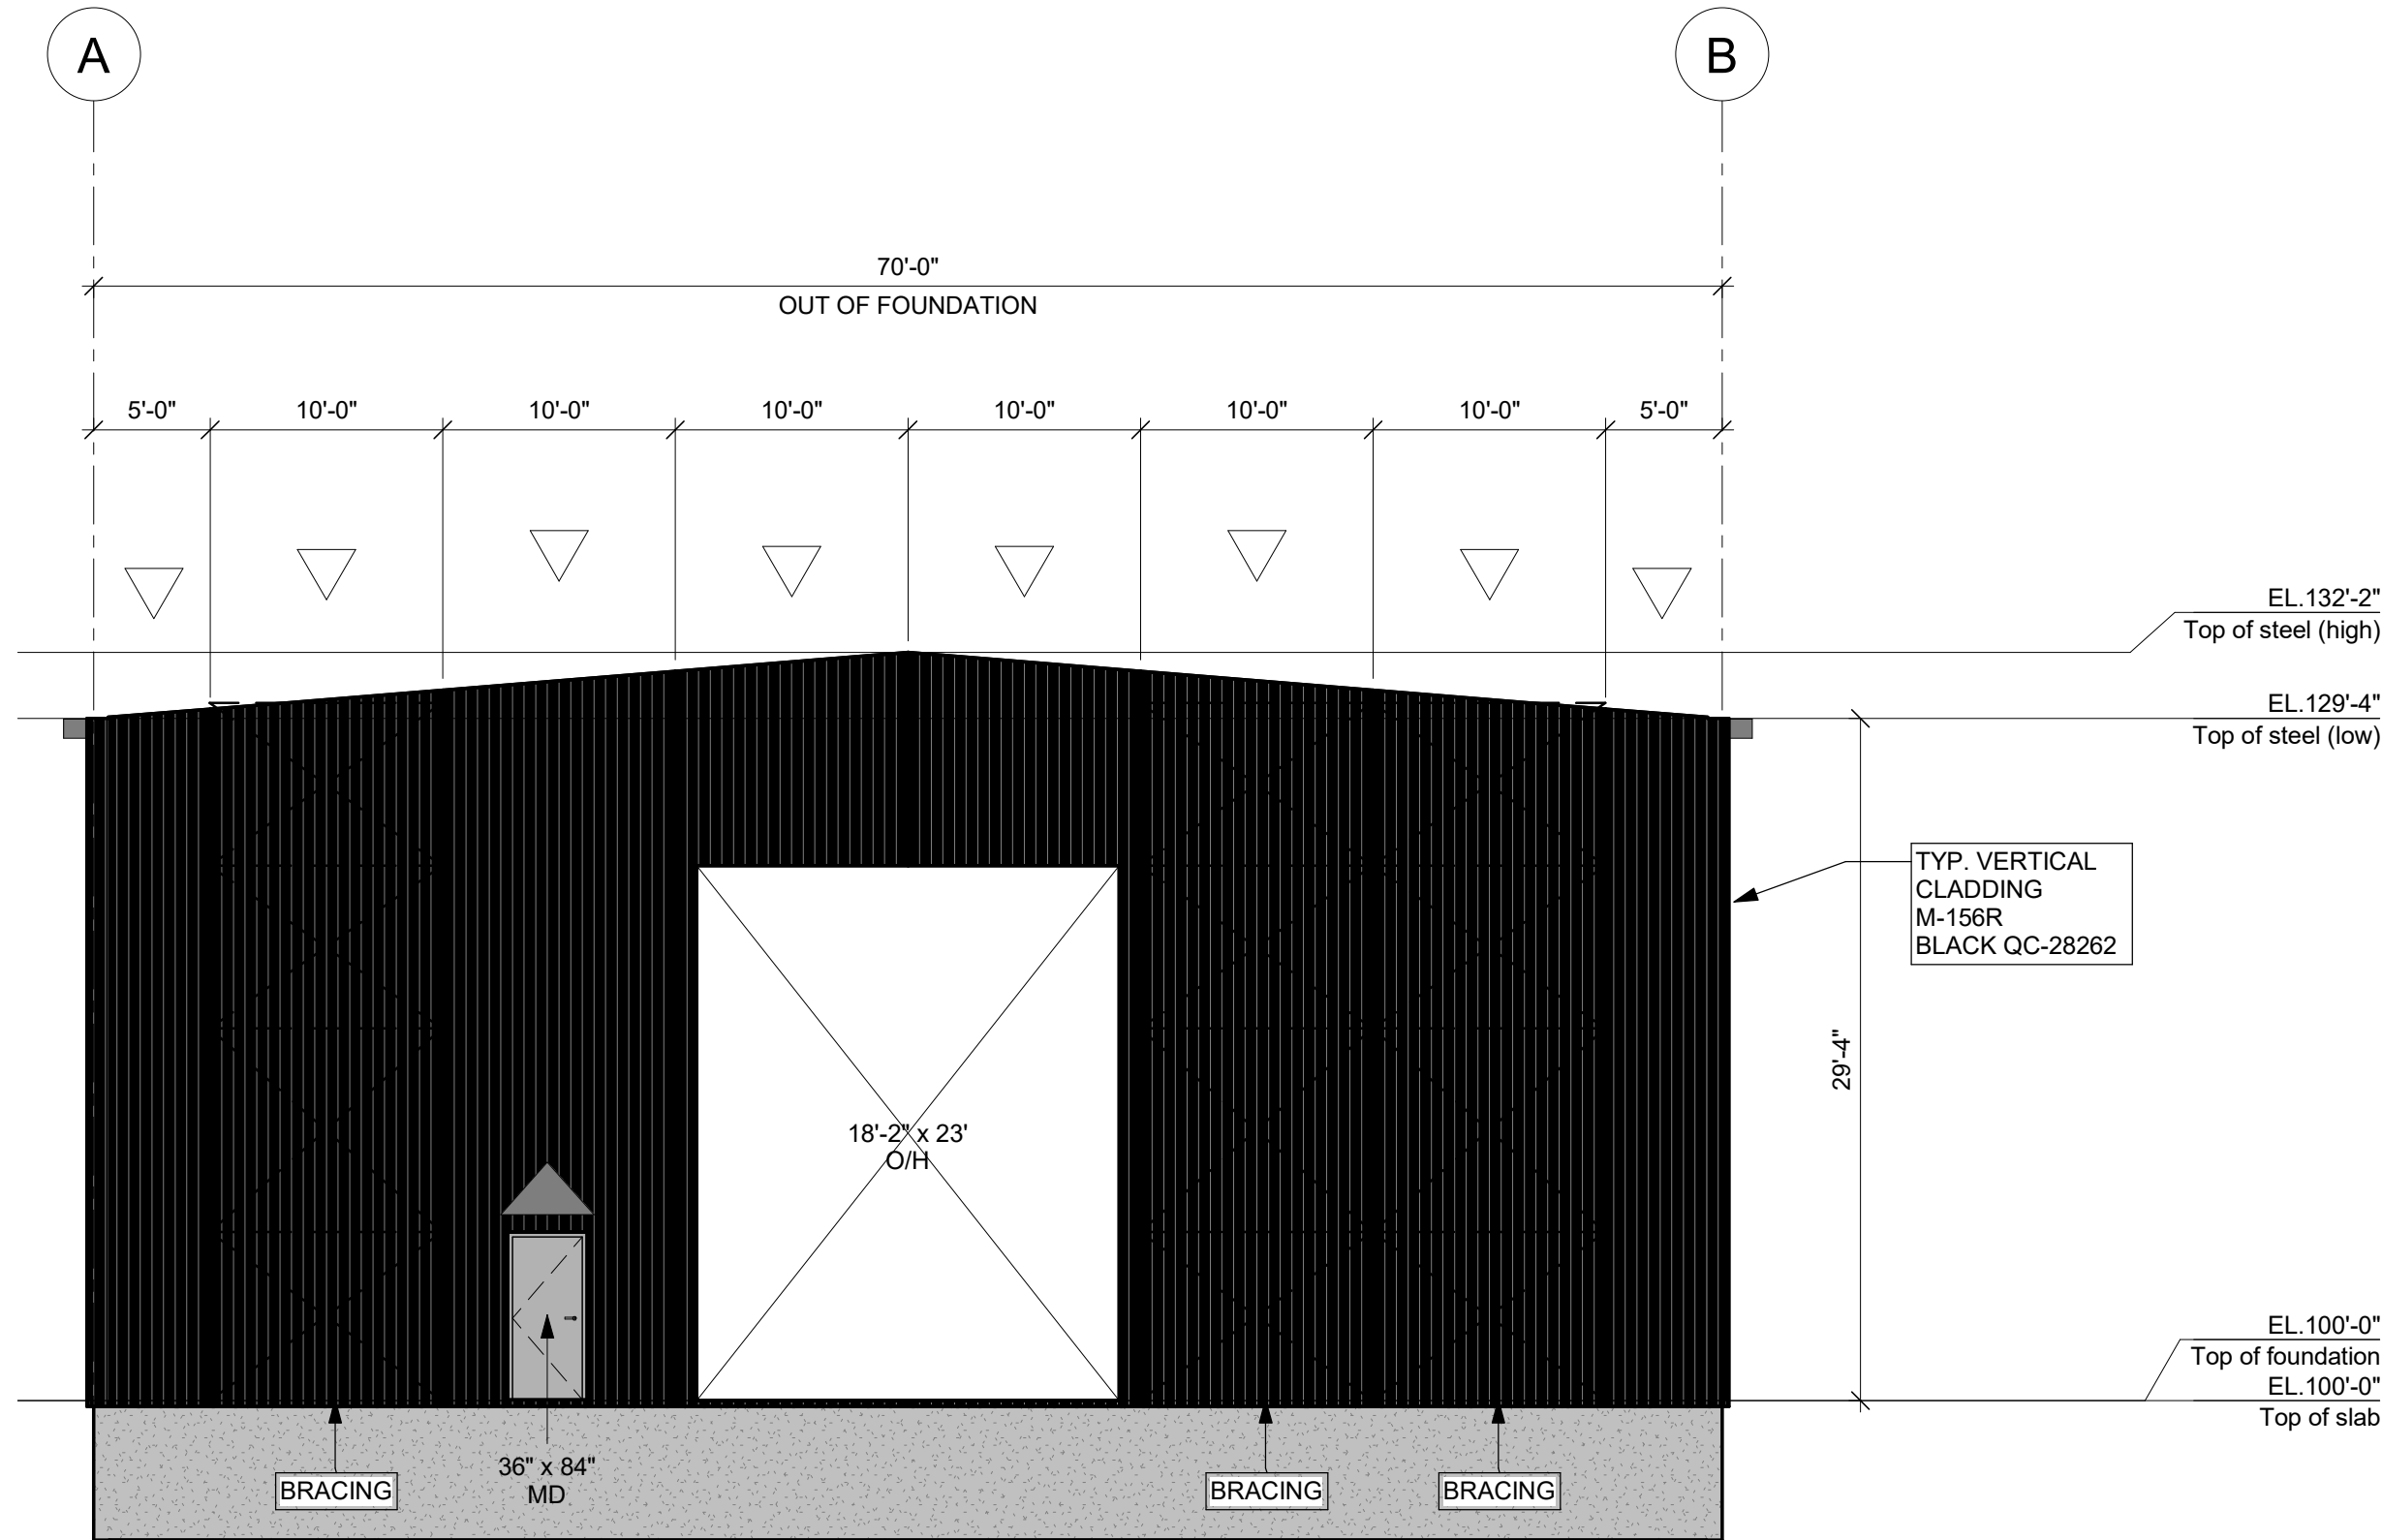


ELEVATION LINE 3 (WEST)
1/8" = 1'-0"

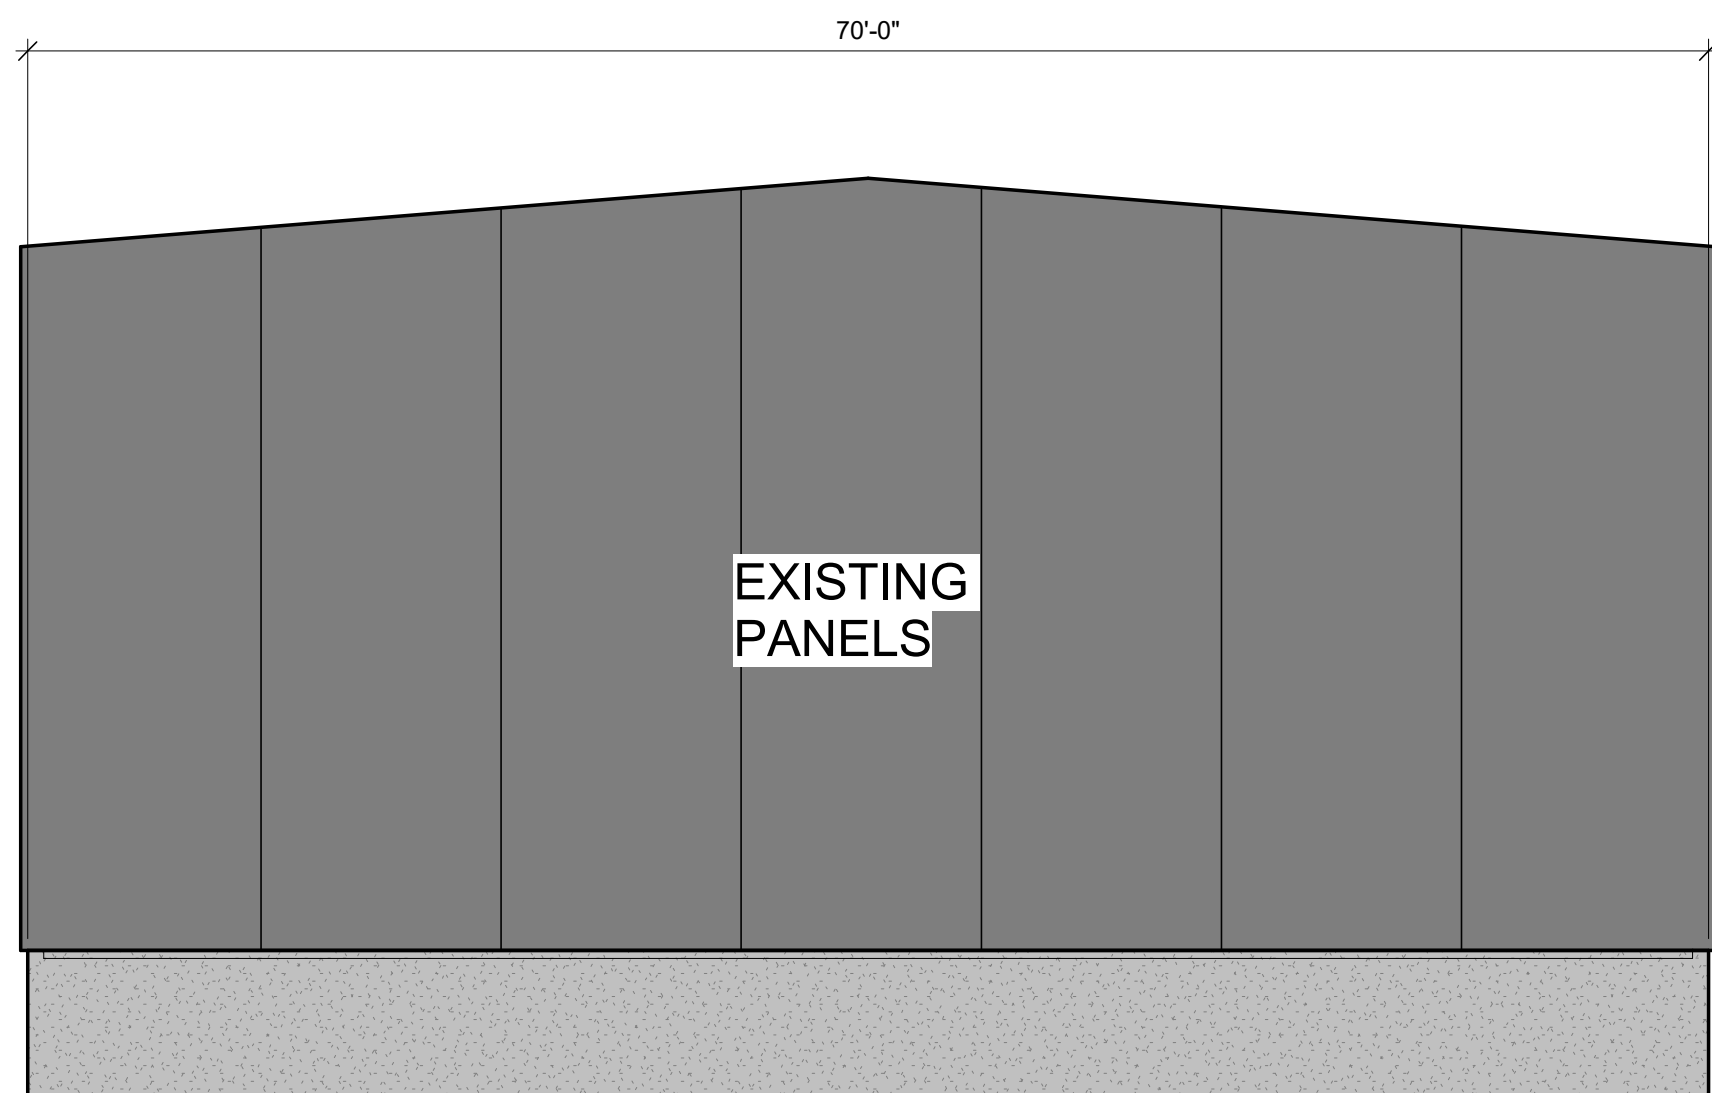


ELEVATION LINE 2 (EAST)(EXISTING)
1/8" = 1'-0"

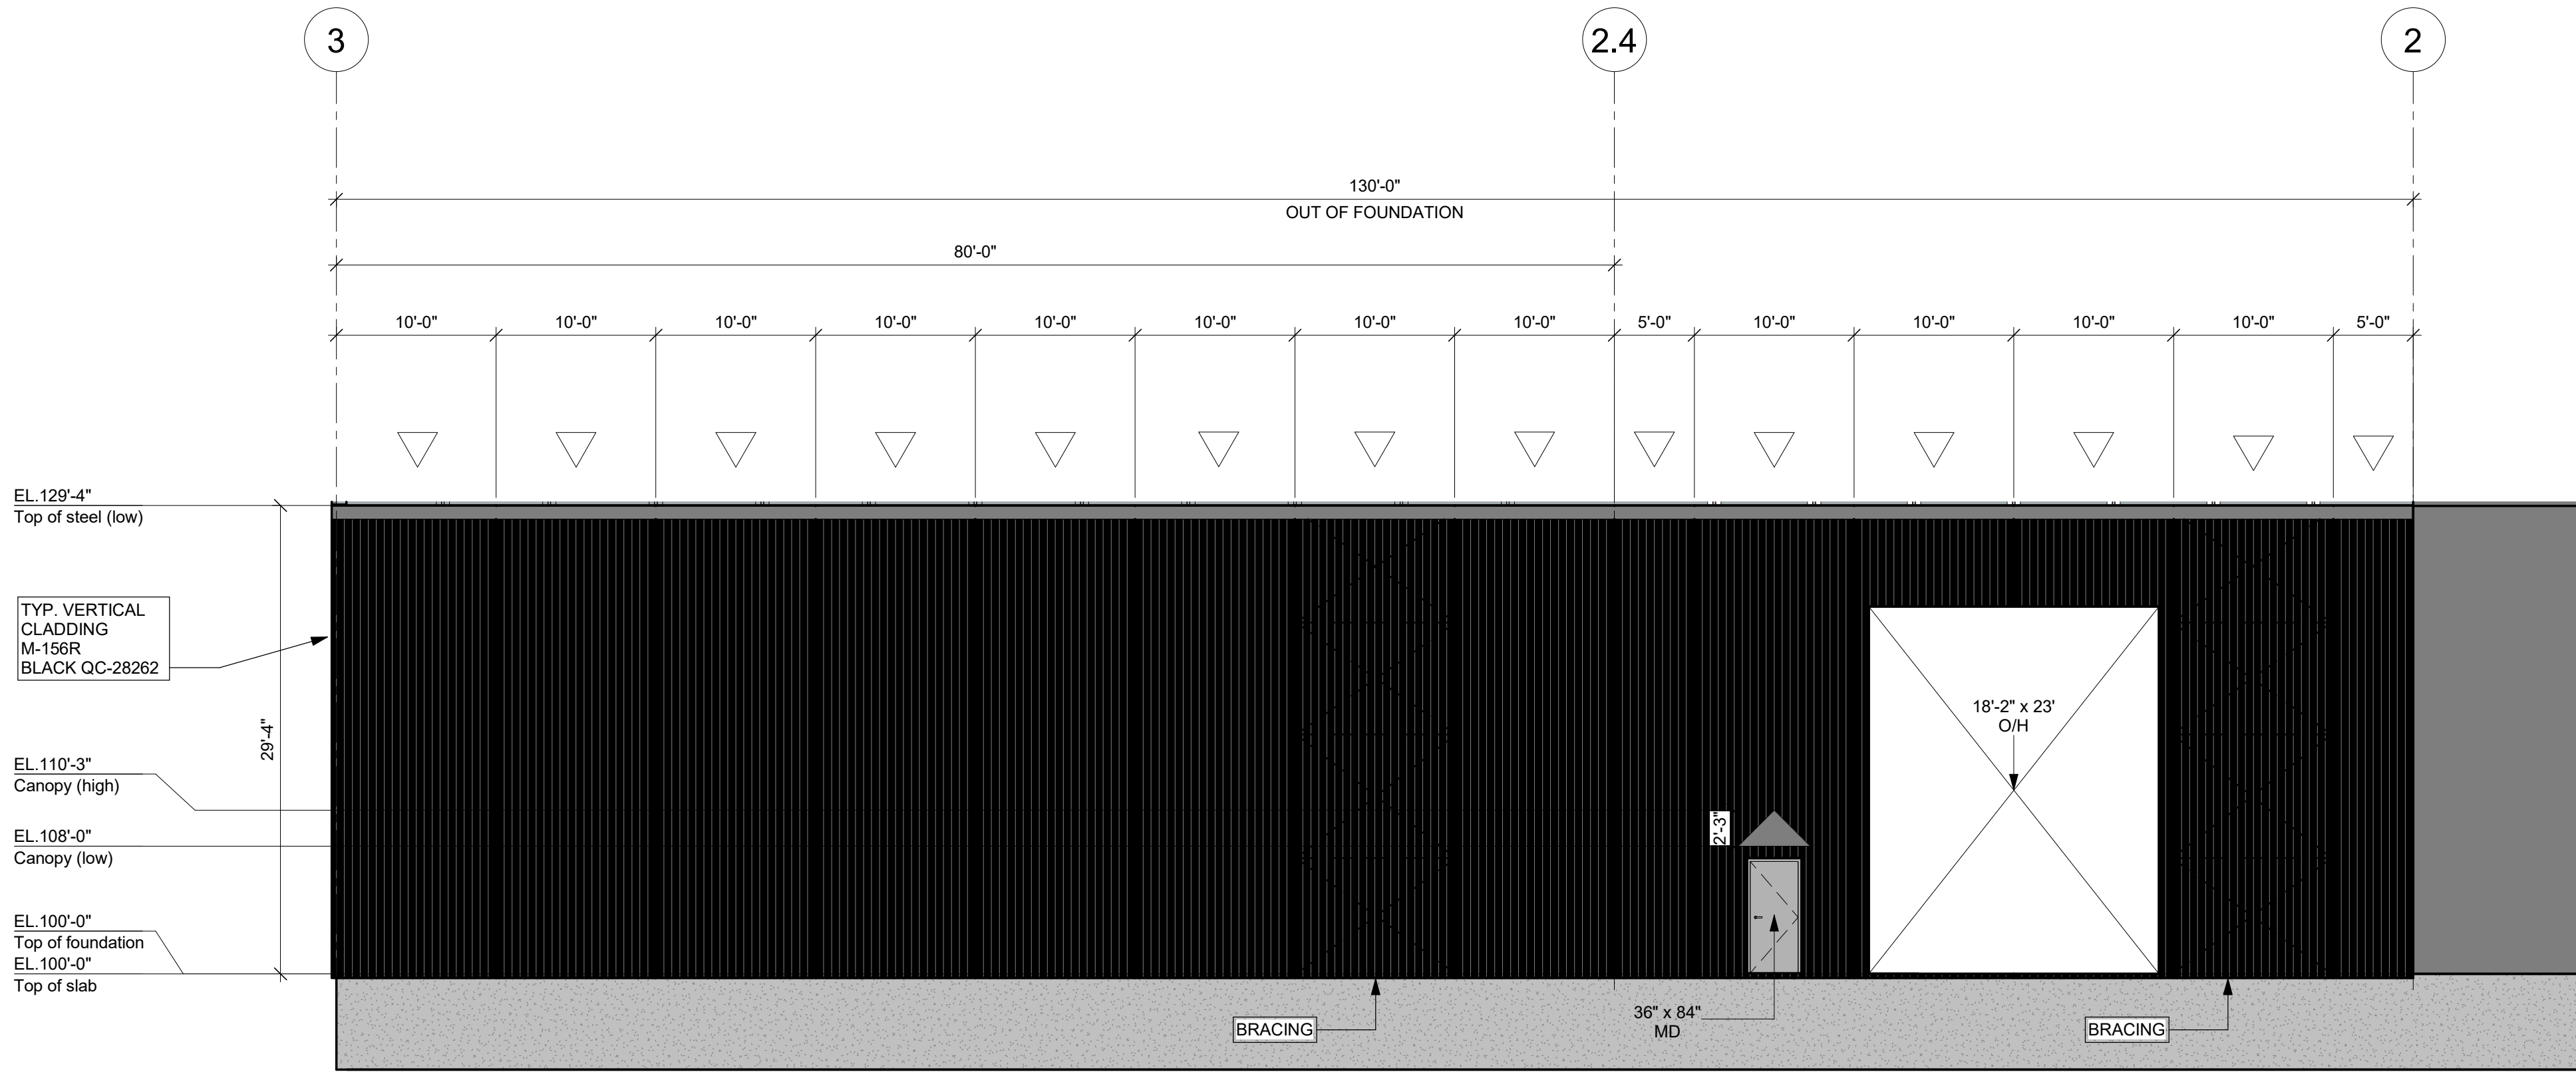

ELEVATION LINE B (SOUTH)
1/8" = 1'-0"

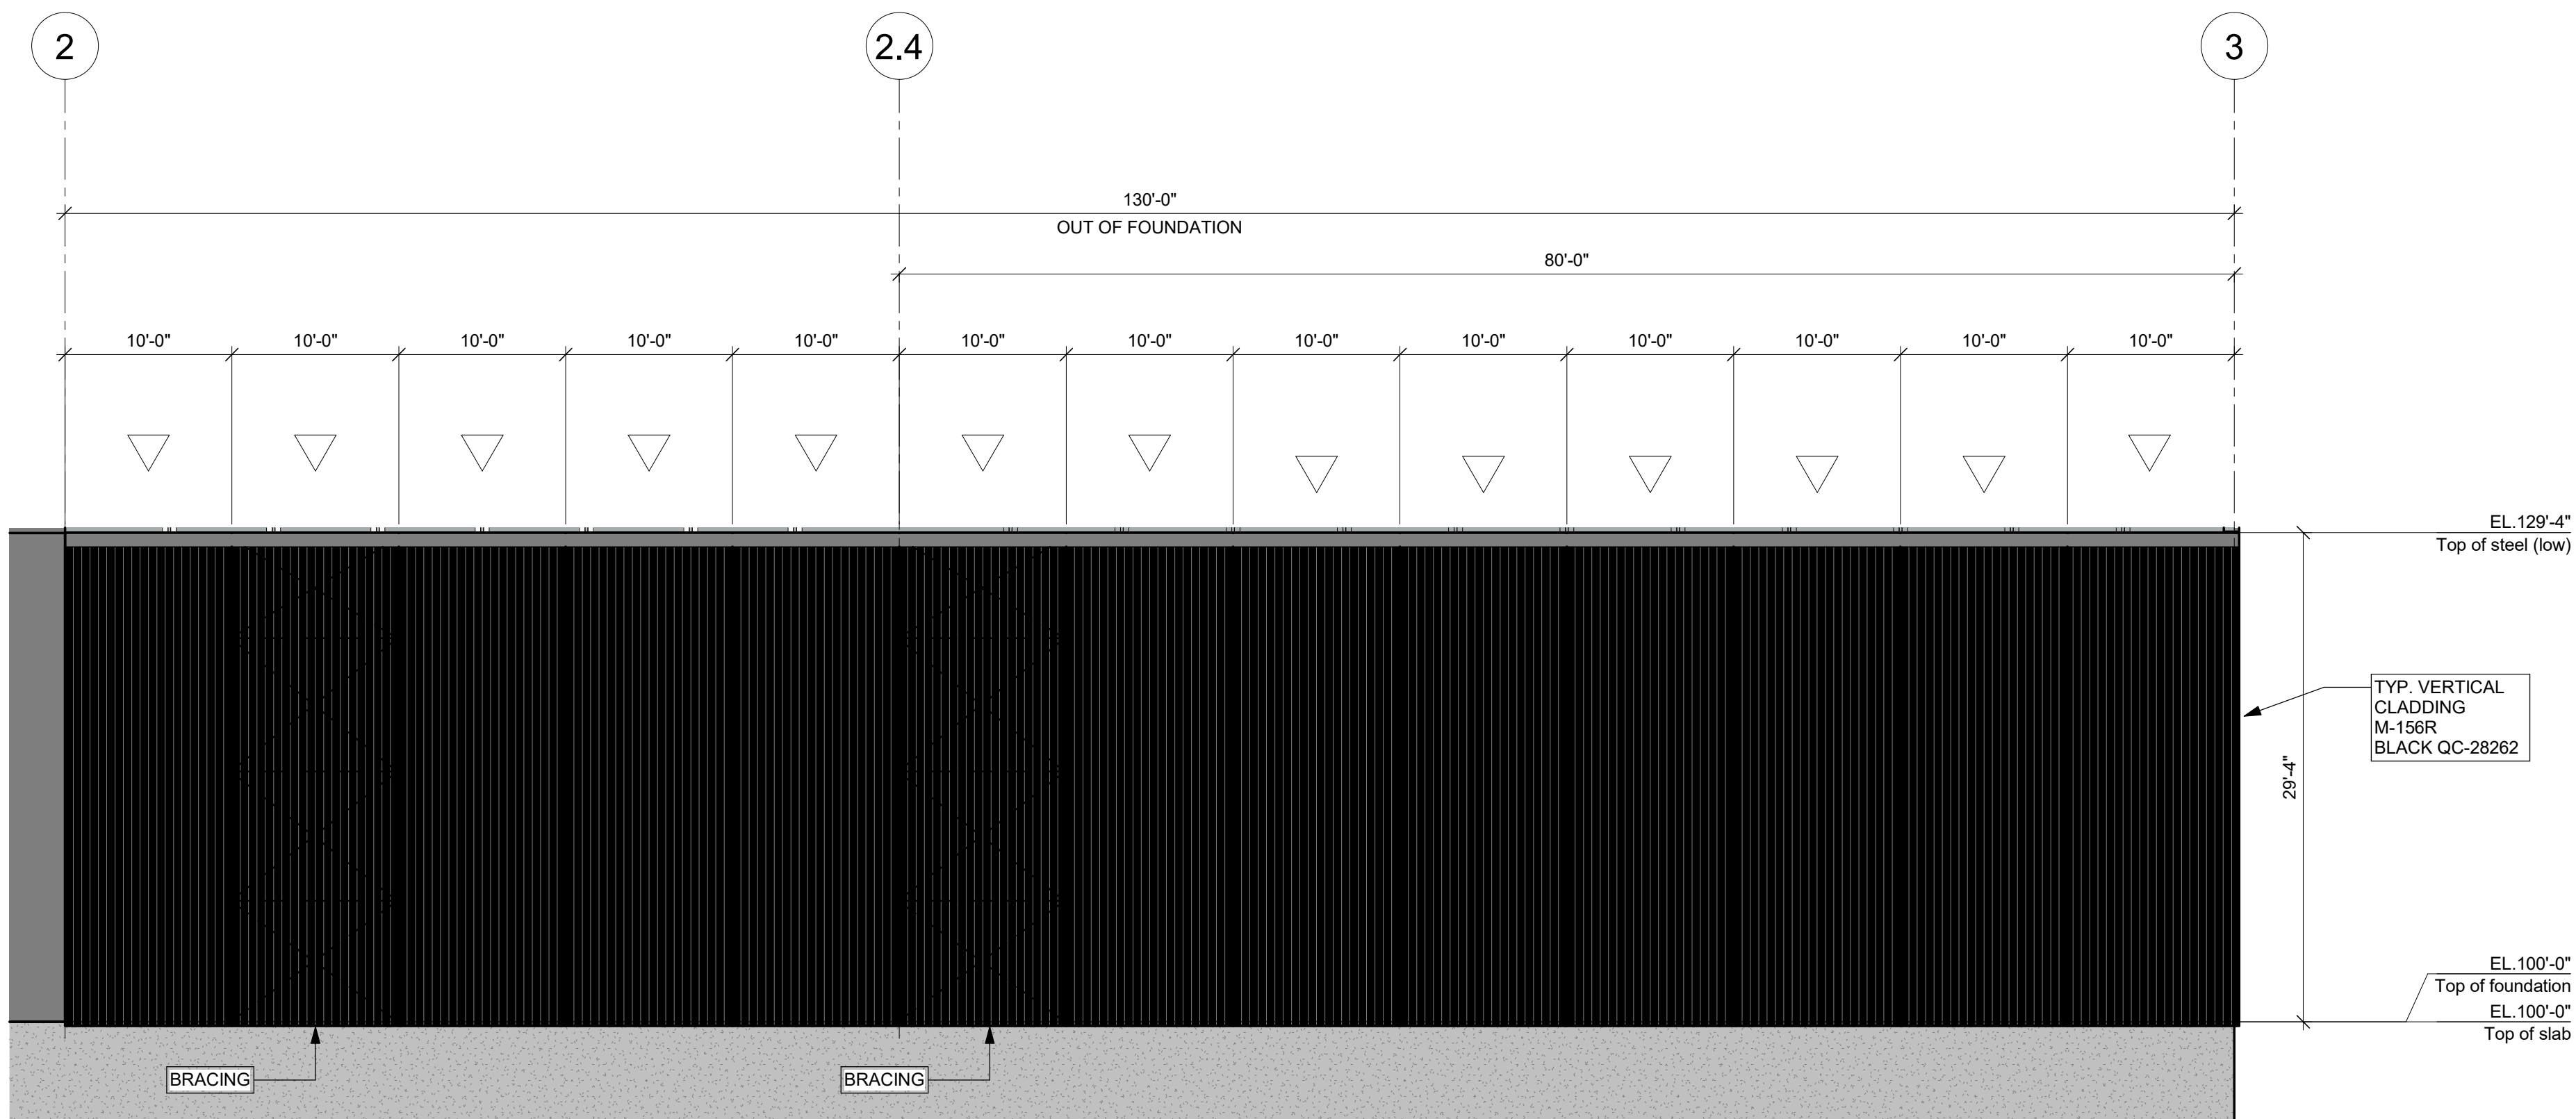

ELEVATION LINE A (NORTH)
1/8" = 1'-0"

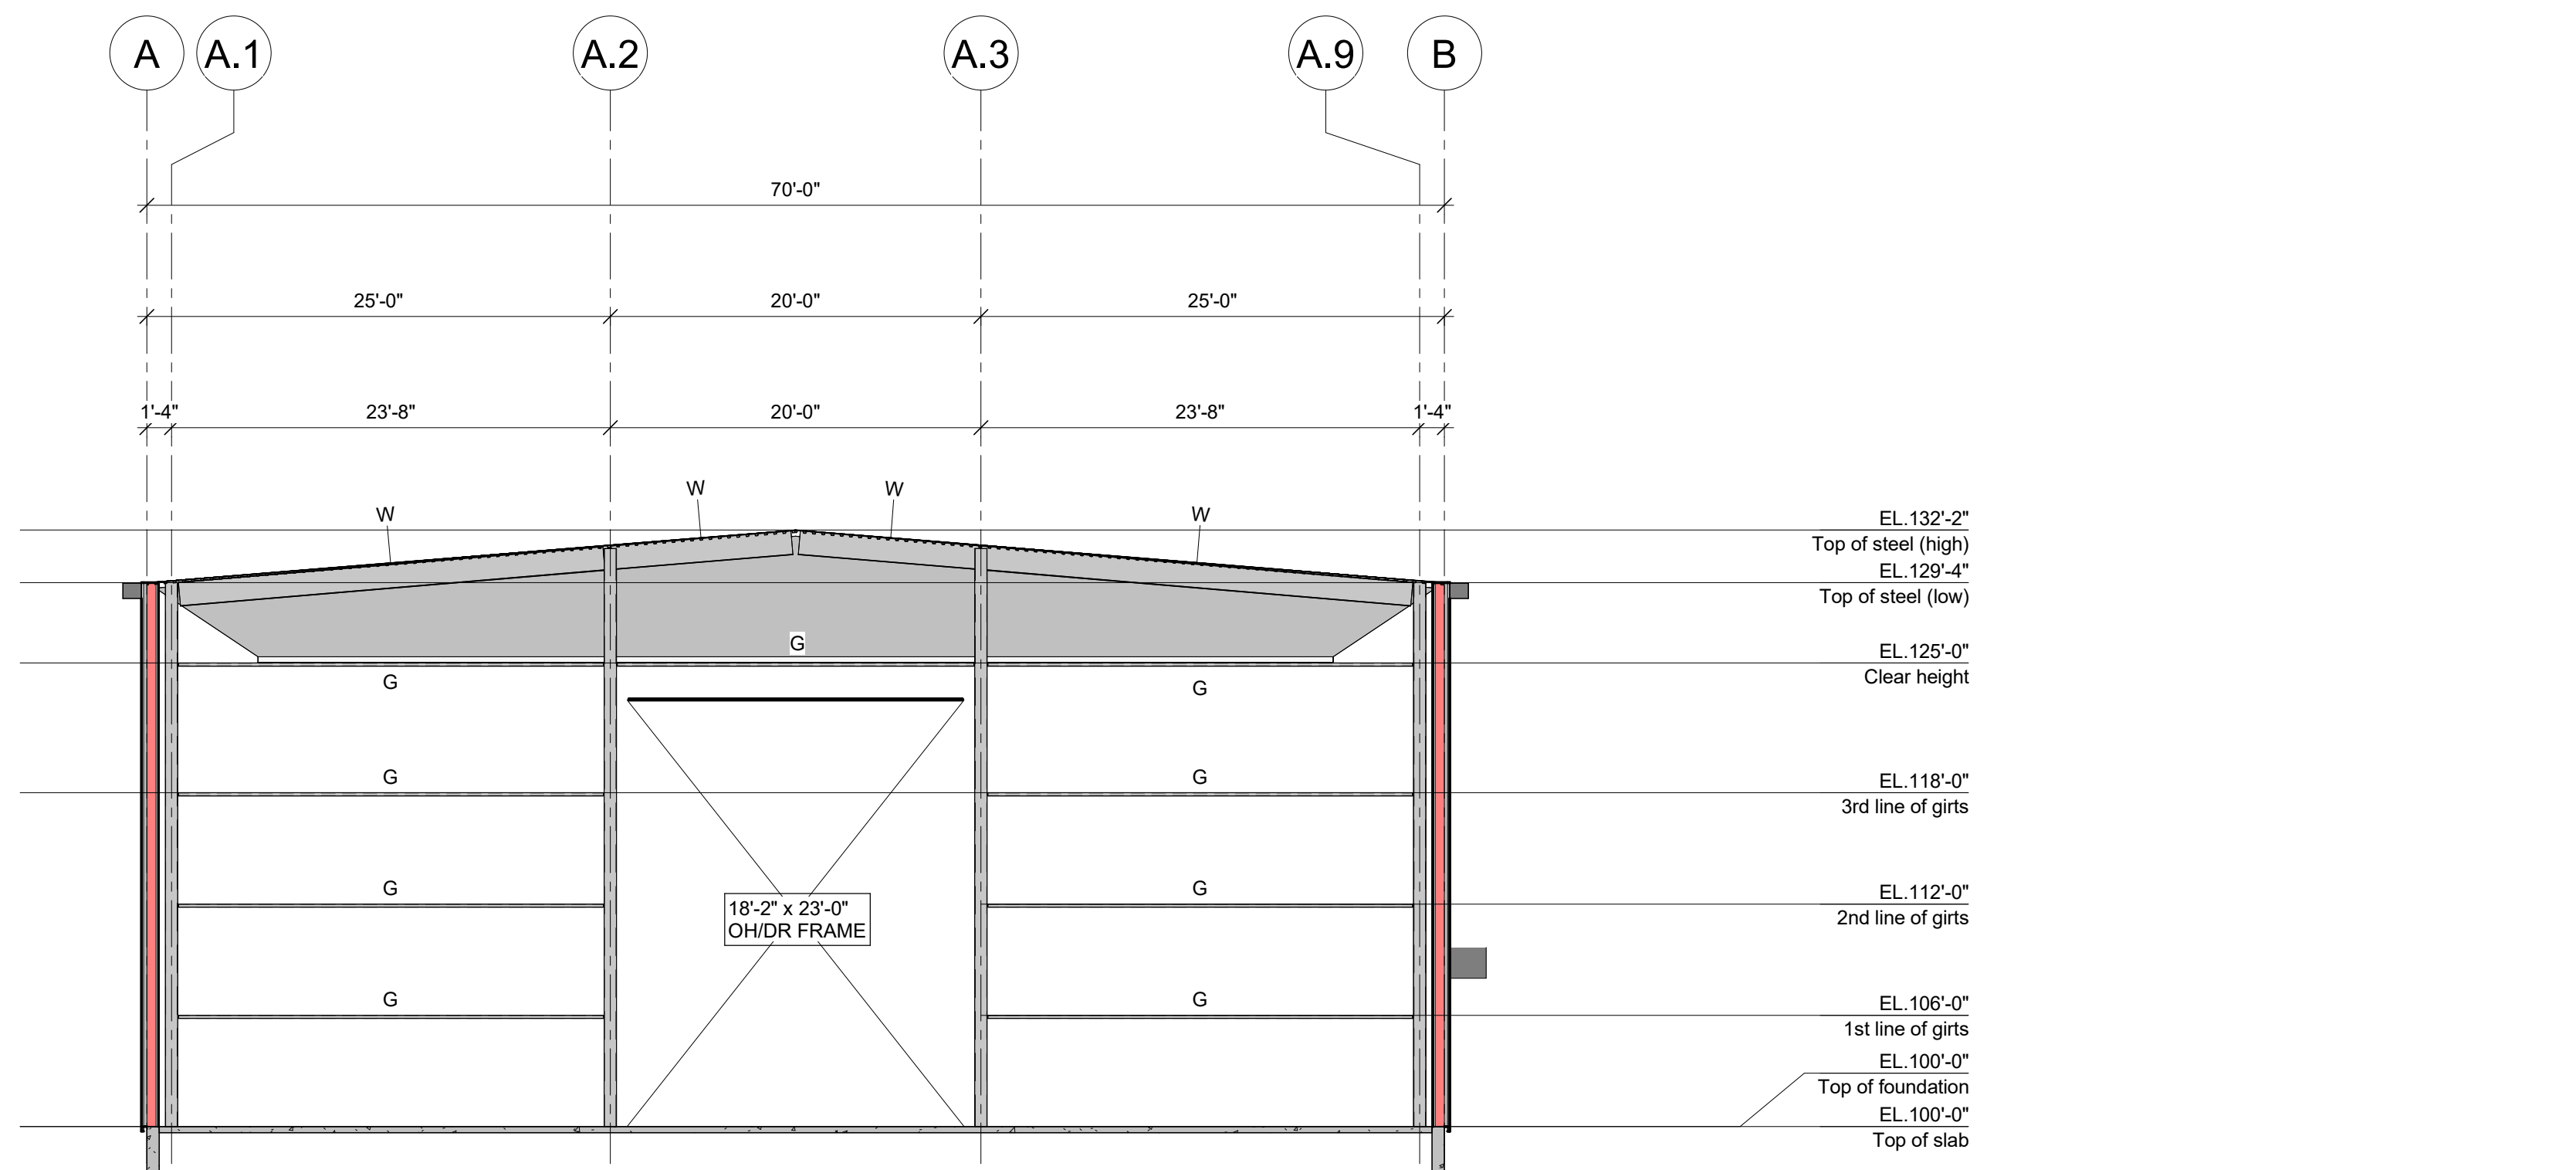

ELEVATION LINE 2.4 (WEST)(STRUCTURE)
1/8" = 1'-0"