


DOOR SCHEDULE			
Identity	Qty.	Door 18 ga.	Remarks
D1	2	36" x 84"	
D2	3	18'-2" x 23'	

Supplier's standard hardware:

- Hinges : Stanley FBB175 4 5" x 4"
- Exit device : Von Dorn 22 x 688 with outside trim 230L
- Permanent cylinder : Schlage 2000IC 626
- Door closure : LCN 1591 659
- Head and jamb seal : Unique 1650
- Bottom seal : Unique D34
- Threshold : See the remarks in "Door schedule"


SUPPLIER'S STD HARDWARE

1/2" = 1'-0"

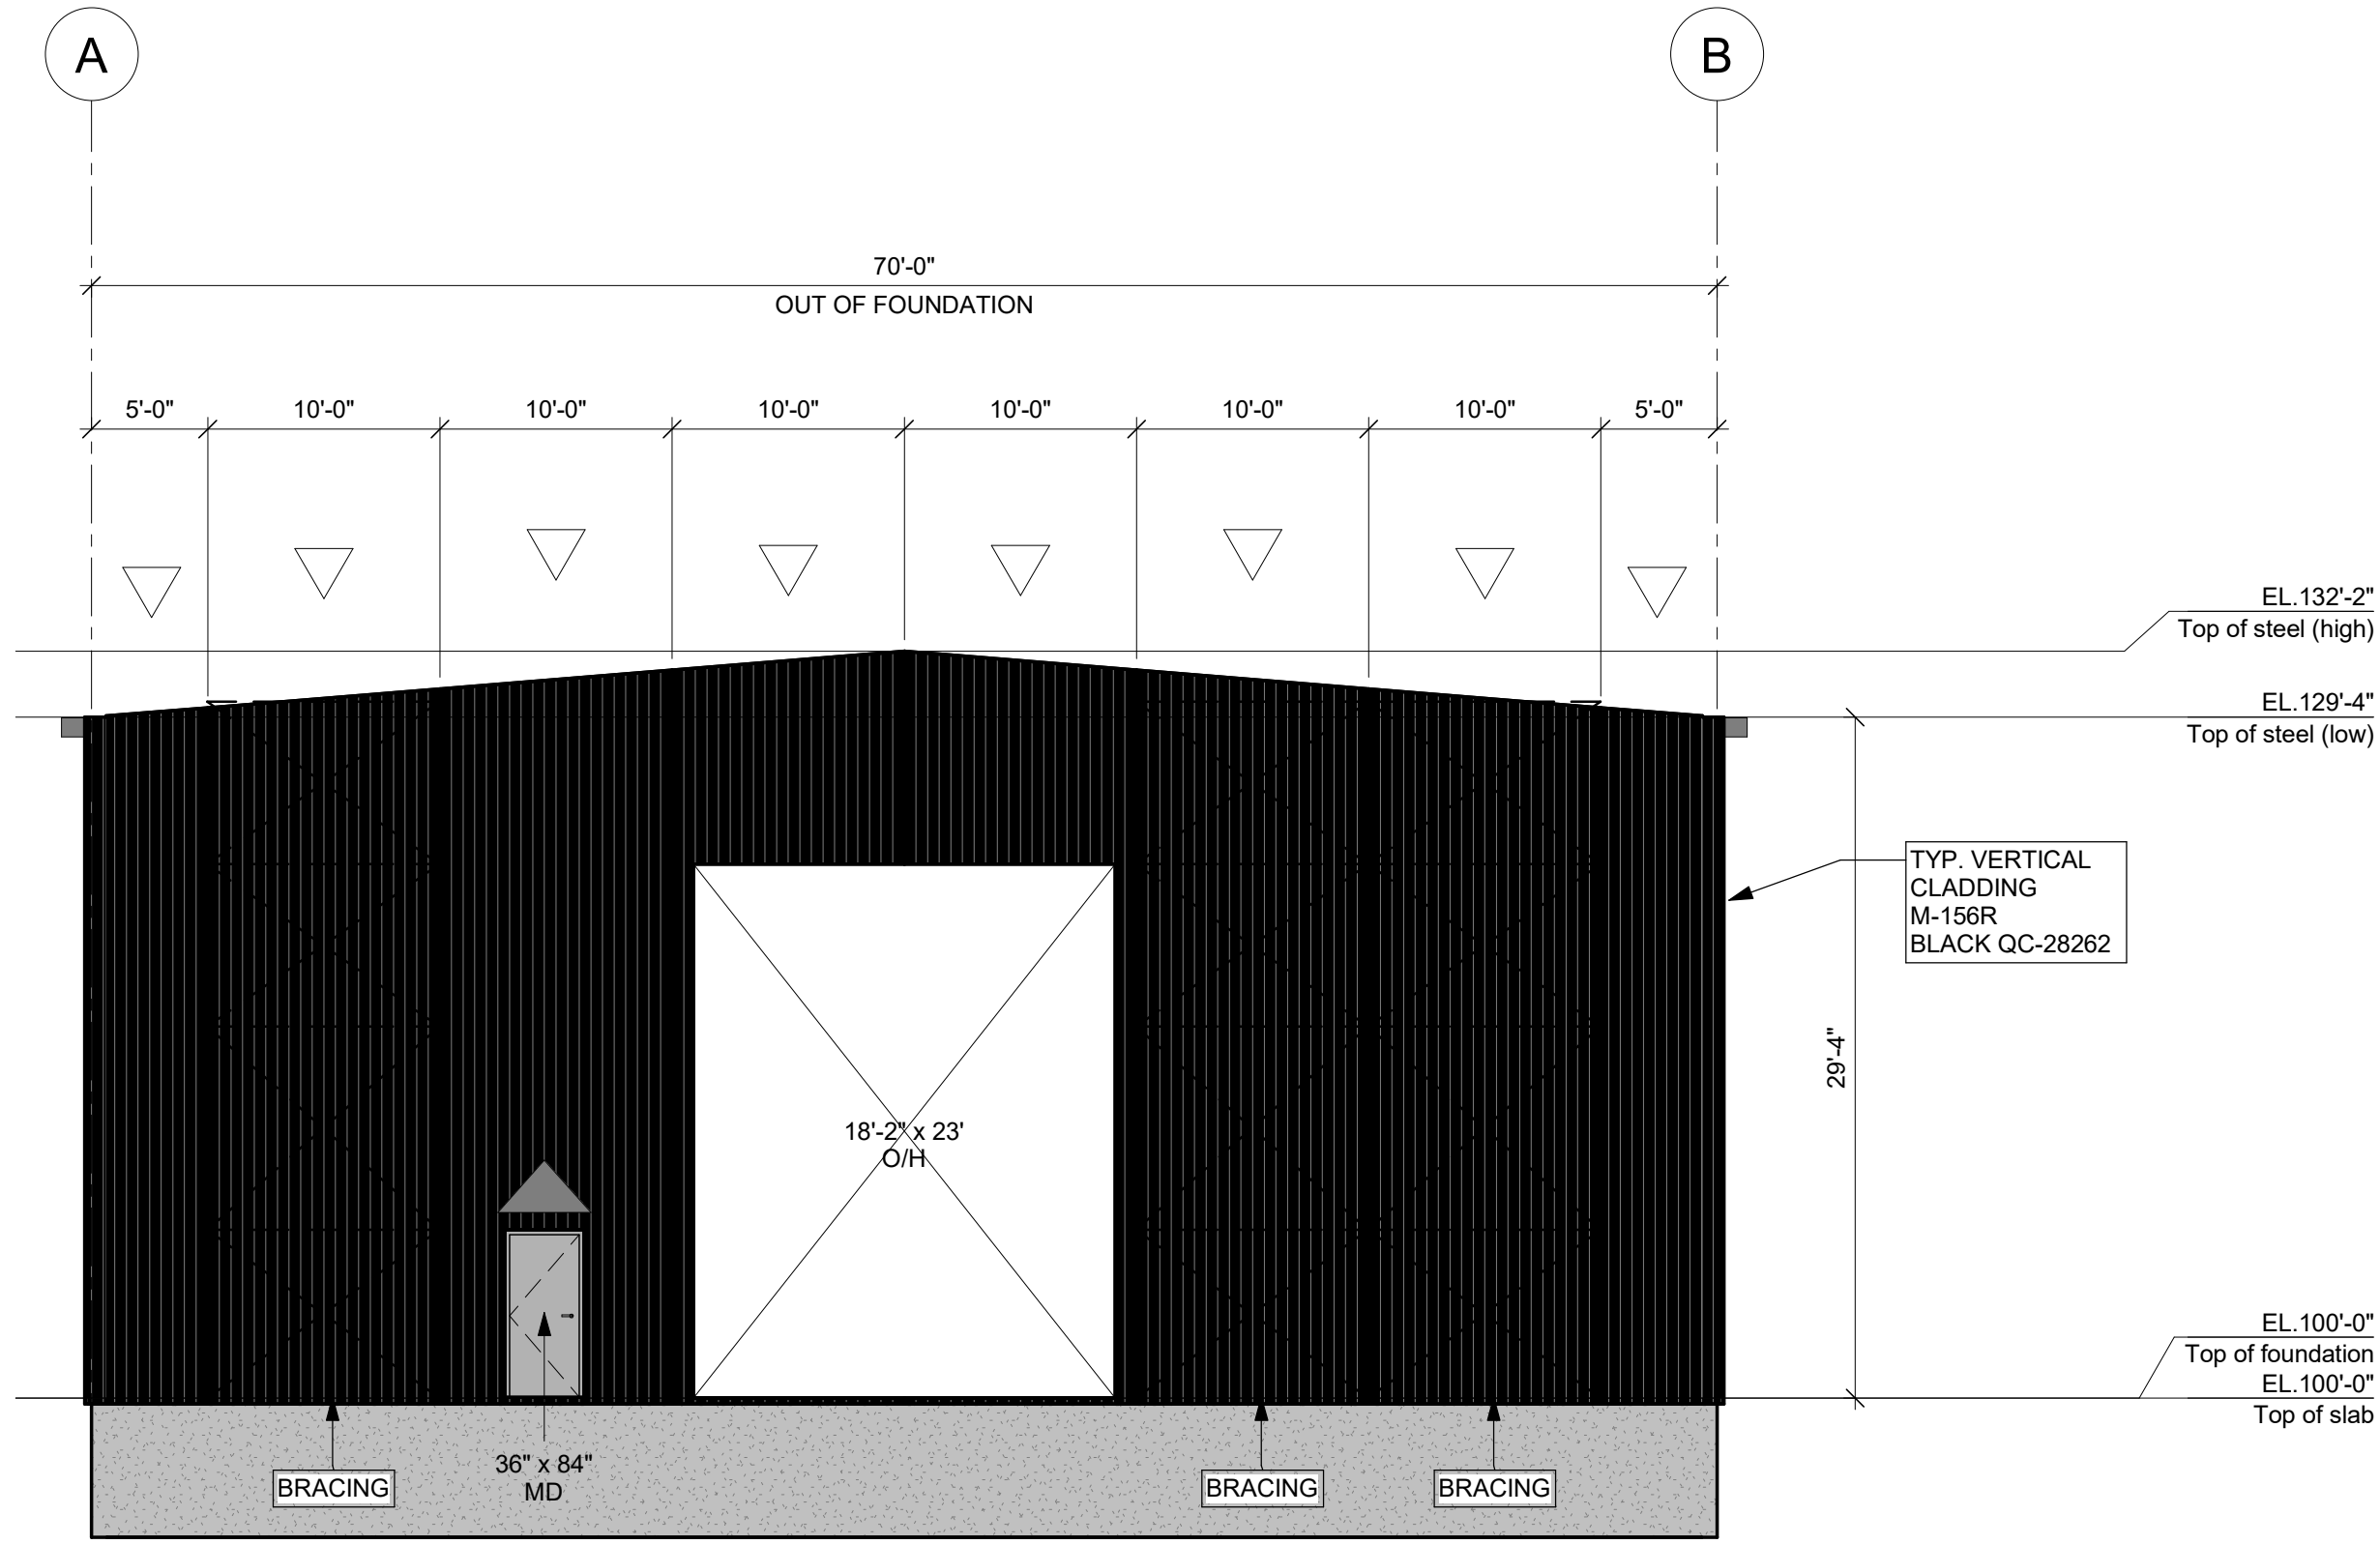


ELEVATION LINE 3 (WEST)

1/8" = 1'-0"

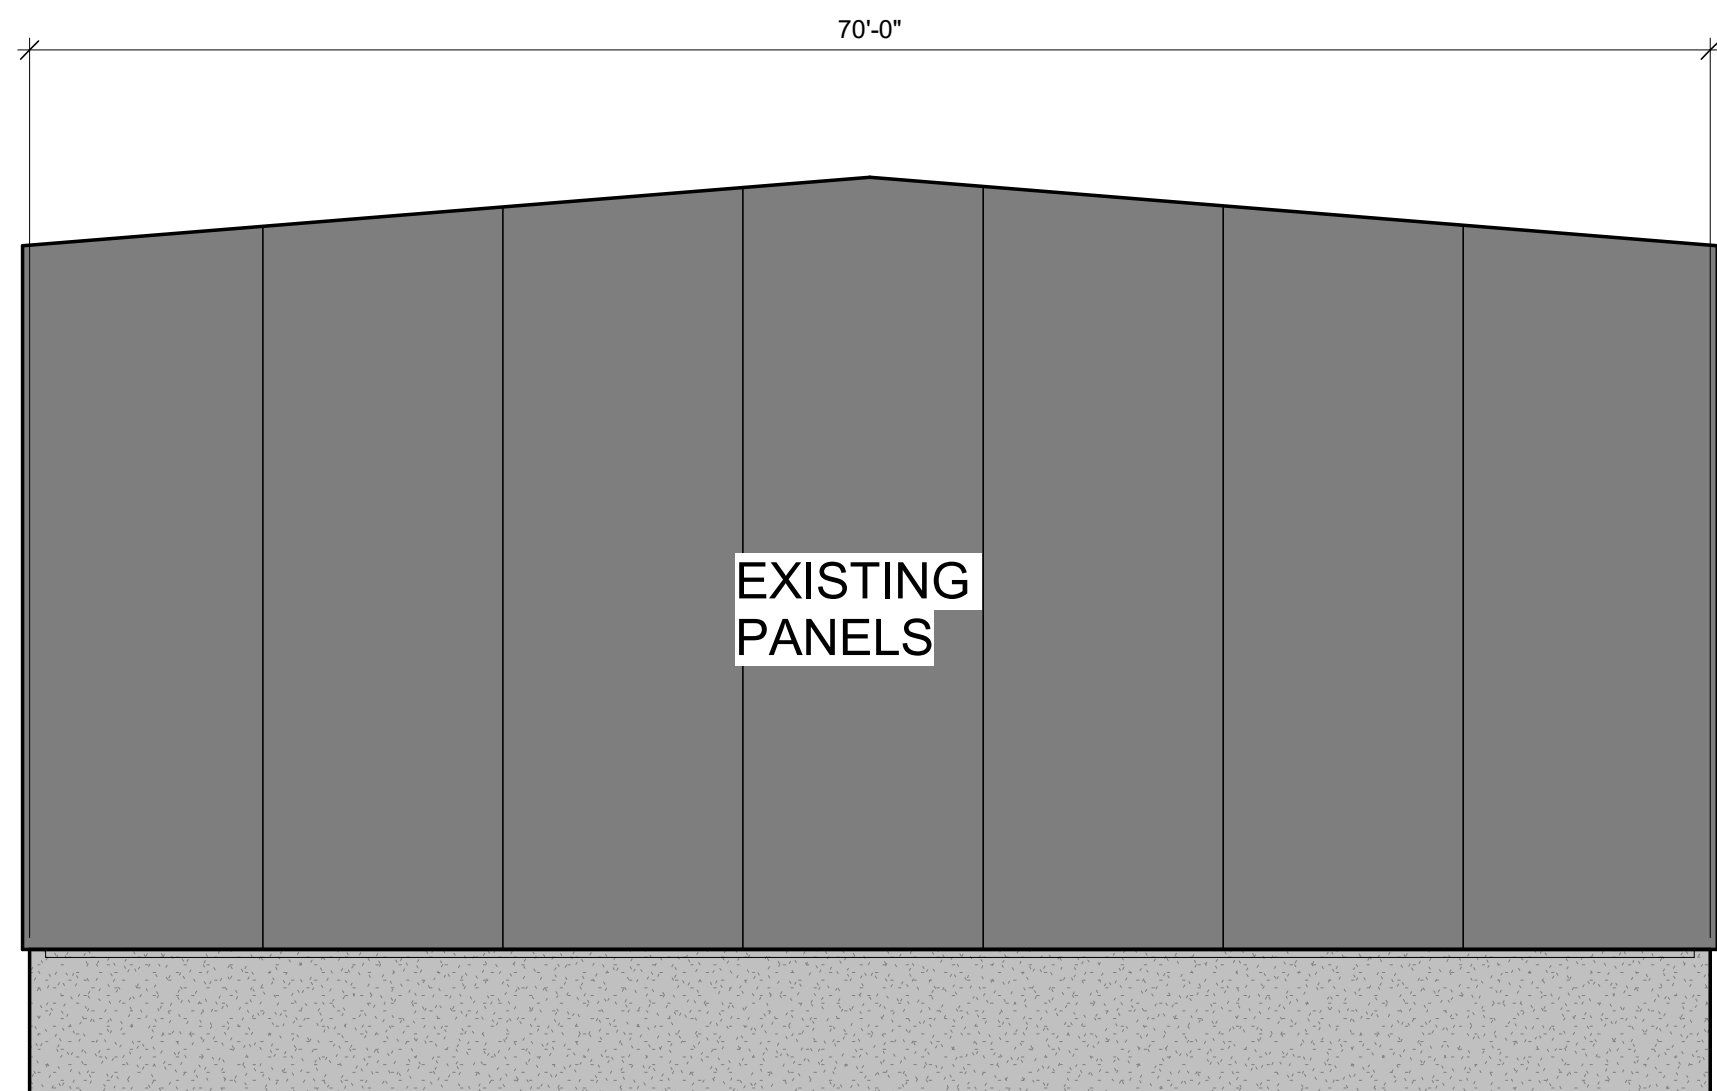


ELEVATION LINE 2 (EAST)(EXISTING)

1/8" = 1'-0"

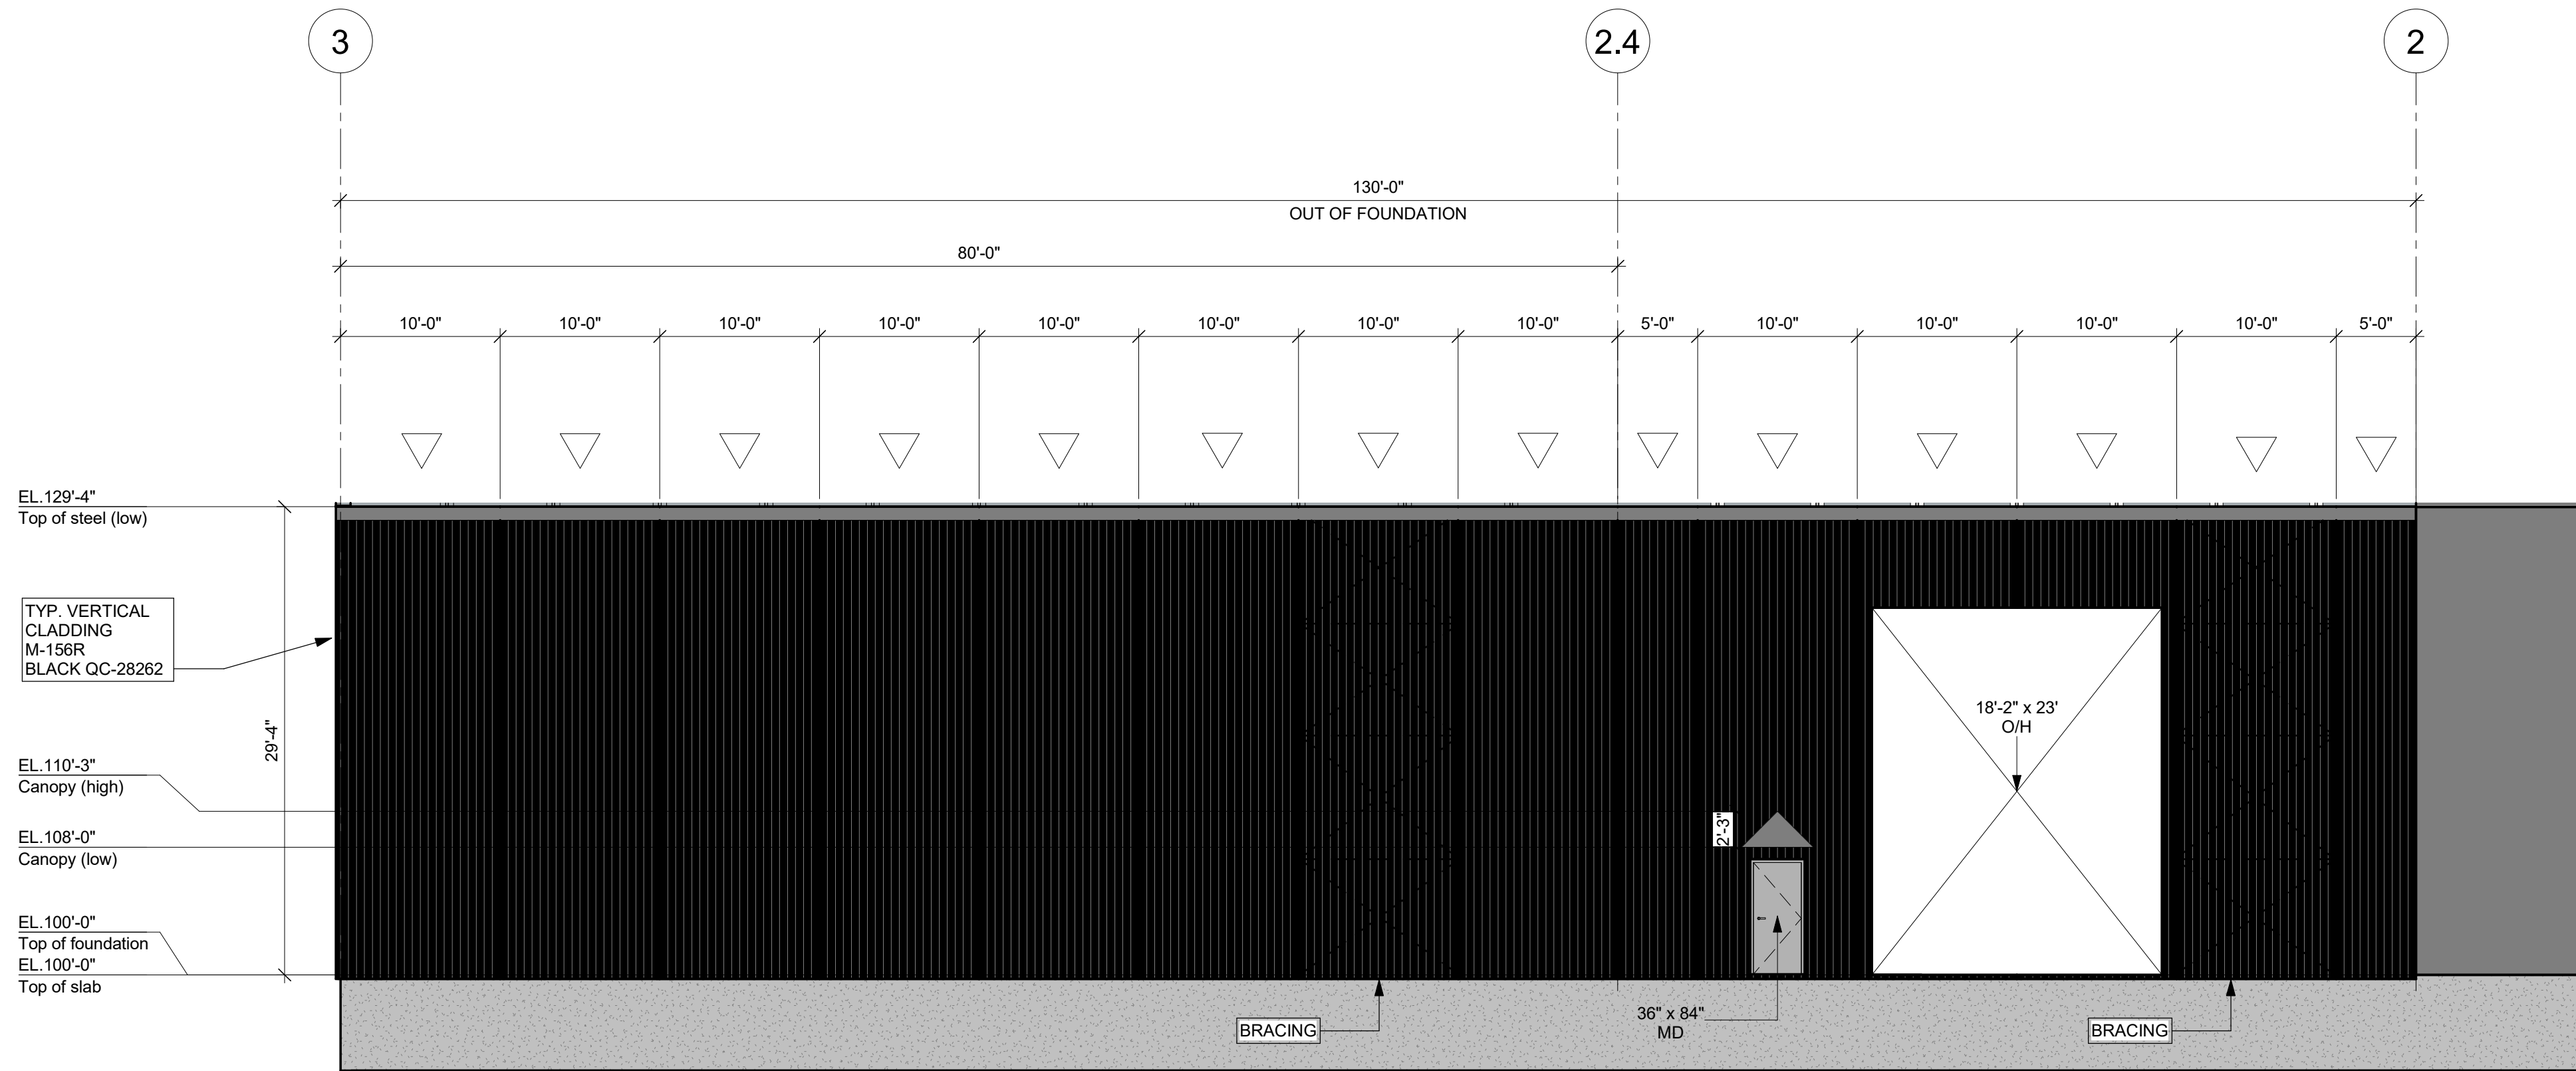


ELEVATION LINE B (SOUTH)

1/8" = 1'-0"

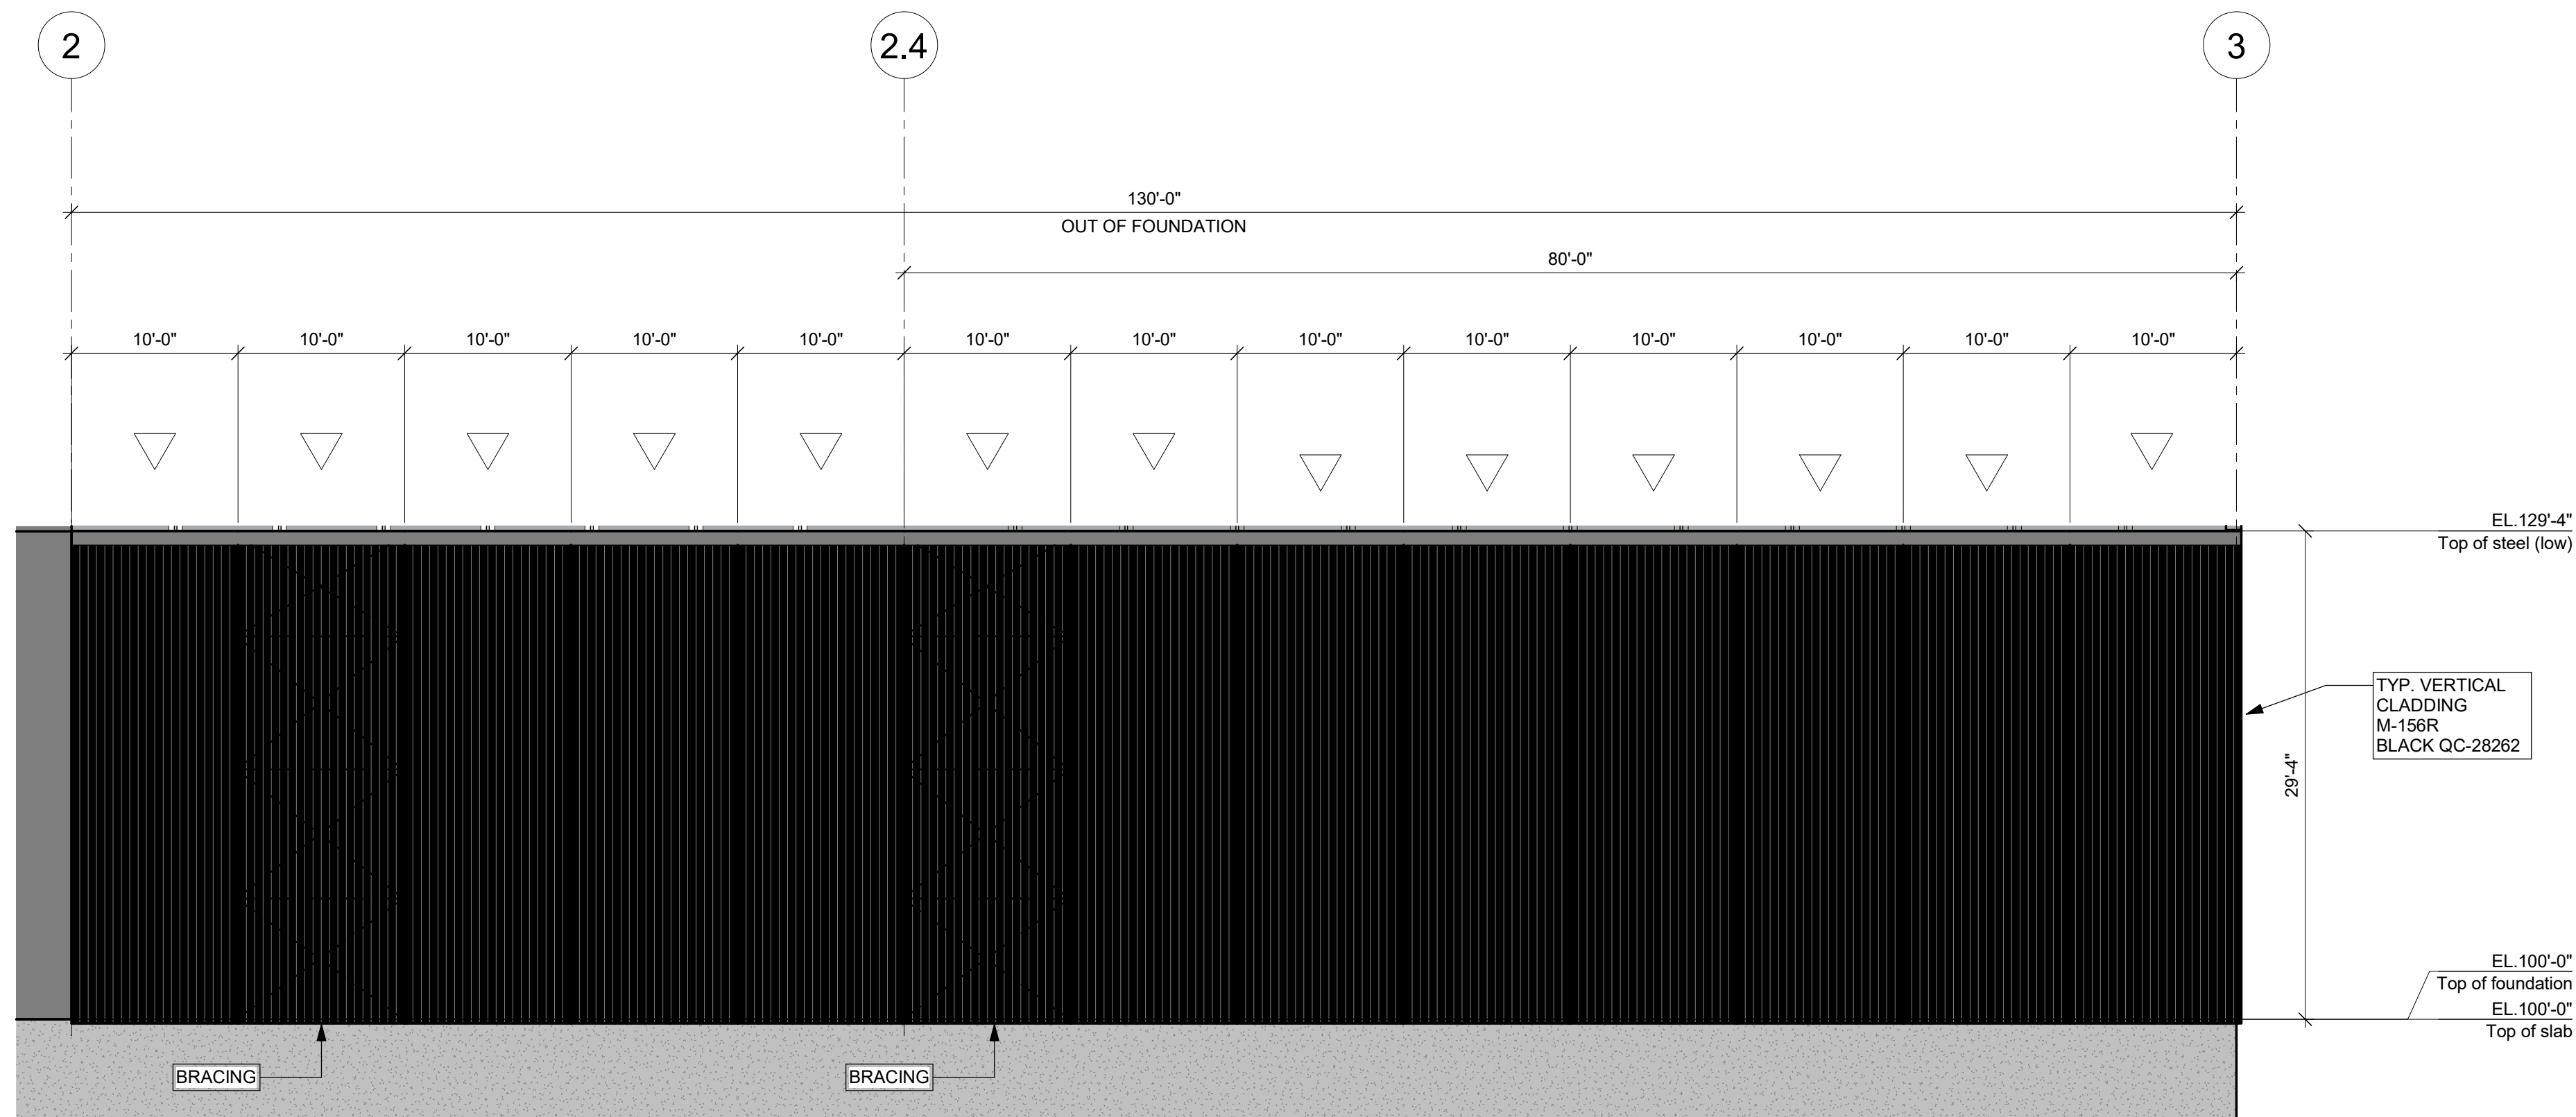

ELEVATION LINE A (NORTH)

1/8" = 1'-0"

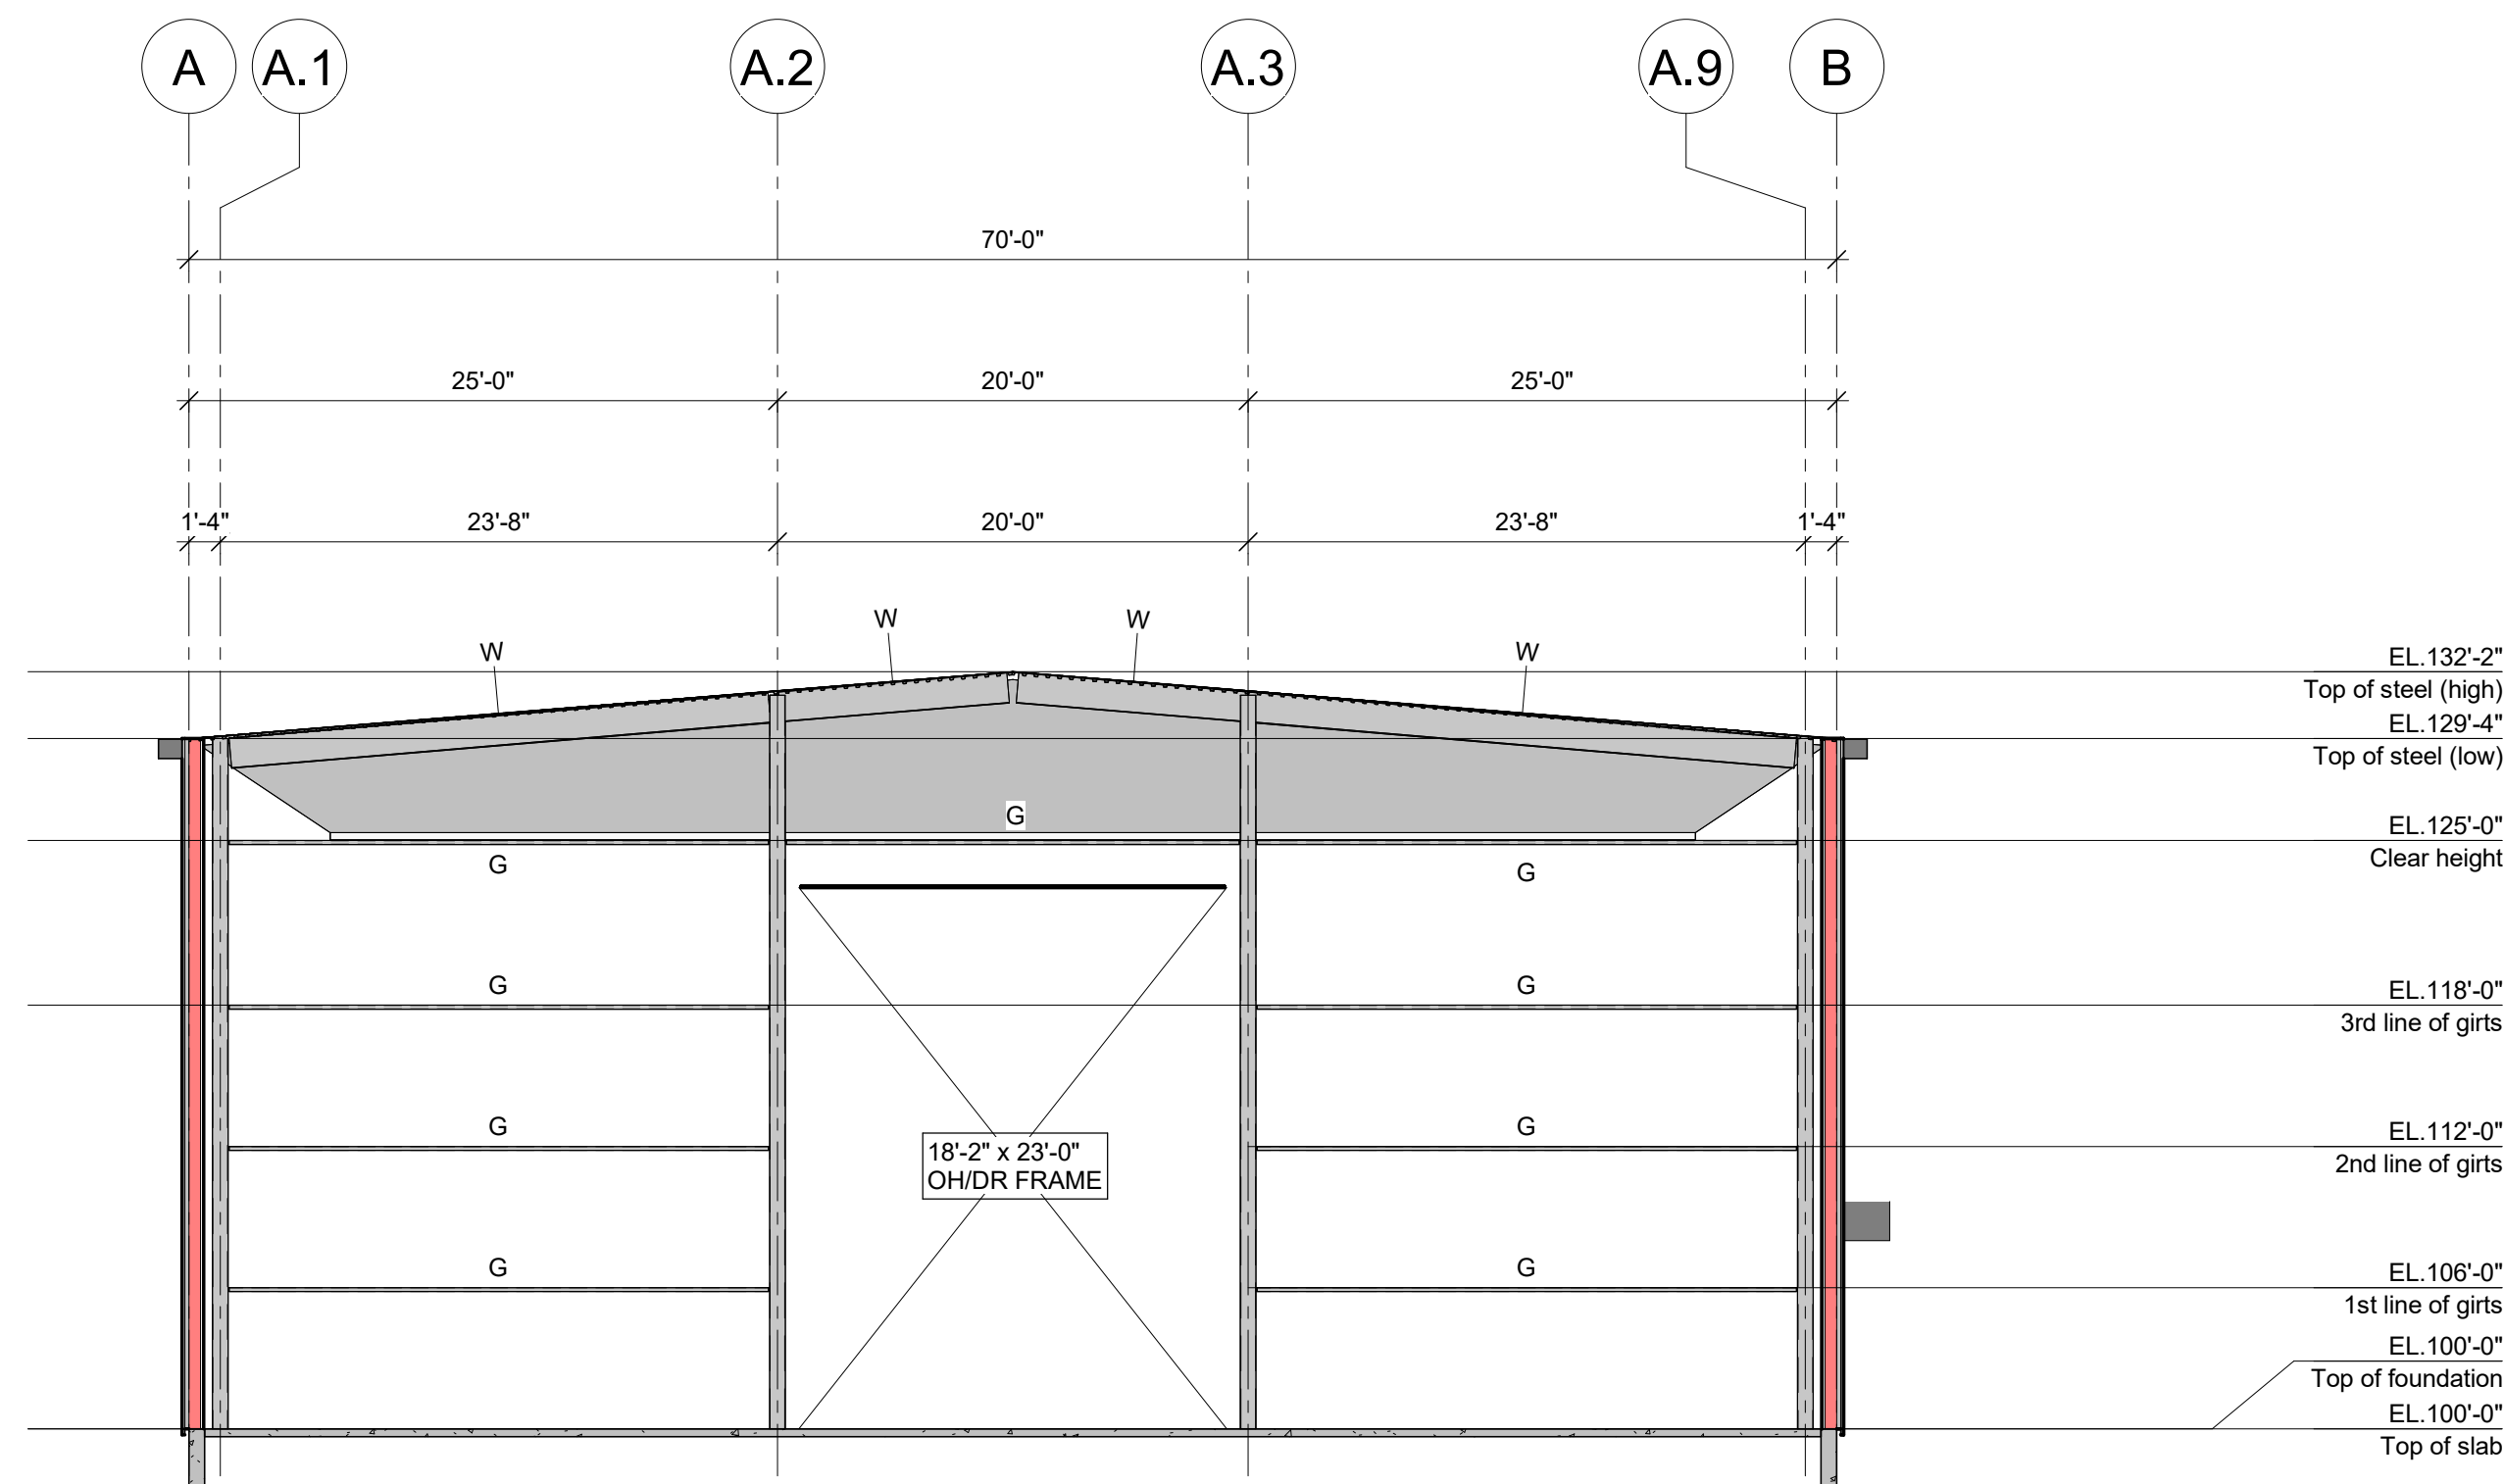

ELEVATION LINE 2.4 (WEST)(STRUCTURE)

1/8" = 1'-0"

CONTRACTOR/RECTOR NOTE:

IT IS PROHIBITED TO MODIFY, COPY, REPRODUCE OR OTHERWISE DISTRIBUTE THIS DRAWING OR ANY REPRESENTATION OF THIS DRAWING OR ANY MEDIA, INCLUDING ELECTRONIC, WITHOUT THE PRIOR WRITTEN APPROVAL OF CANAM GROUP INC.

PRELIMINARY

NOT TO BE USED FOR CONSTRUCTION

1	05/04/2025	Revised bdy dimensions, door and OH/OR quantities	SL	USR
---	------------	---	----	-----

REVISION	DATE	DESCRIPTION	BY	APP
----------	------	-------------	----	-----

PROJECT MANAGER				
-----------------	--	--	--	--

DRAFTING				
----------	--	--	--	--

DRAWN	DESIGNED	PROJECT ENGINEER	SCALE:
-------	----------	------------------	--------

INITIALE			Comme indiqu�
----------	--	--	---------------

CHECKED	CONSULTING ENGINEERS / ARCHITECTS	DATE (yyyy/mm/dd)
---------	-----------------------------------	-------------------

CUSTOMER:	
-----------	--

CANAM

11505, 1re Avenue, bureau 500, Saint-Georges Beauce
Chabot, Canada, G5Y 7G3
Phone : (418) 228-8031
Toll free : (877) 499-6049
www.canam.com

PROFESSIONAL SEAL	
-------------------	--

PROJECT	
---------	--

ESTEVAN, SASKATCHEWAN

DRAWING TITLE	
---------------	--

PRELIMINARY SKETCH - ELEVATIONS

CONTRACT NUMBER	DRAWING NUMBER	DIVISION	REVISION
-----------------	----------------	----------	----------

P2025-079	EsMx501		1
-----------	---------	--	---