



Scale

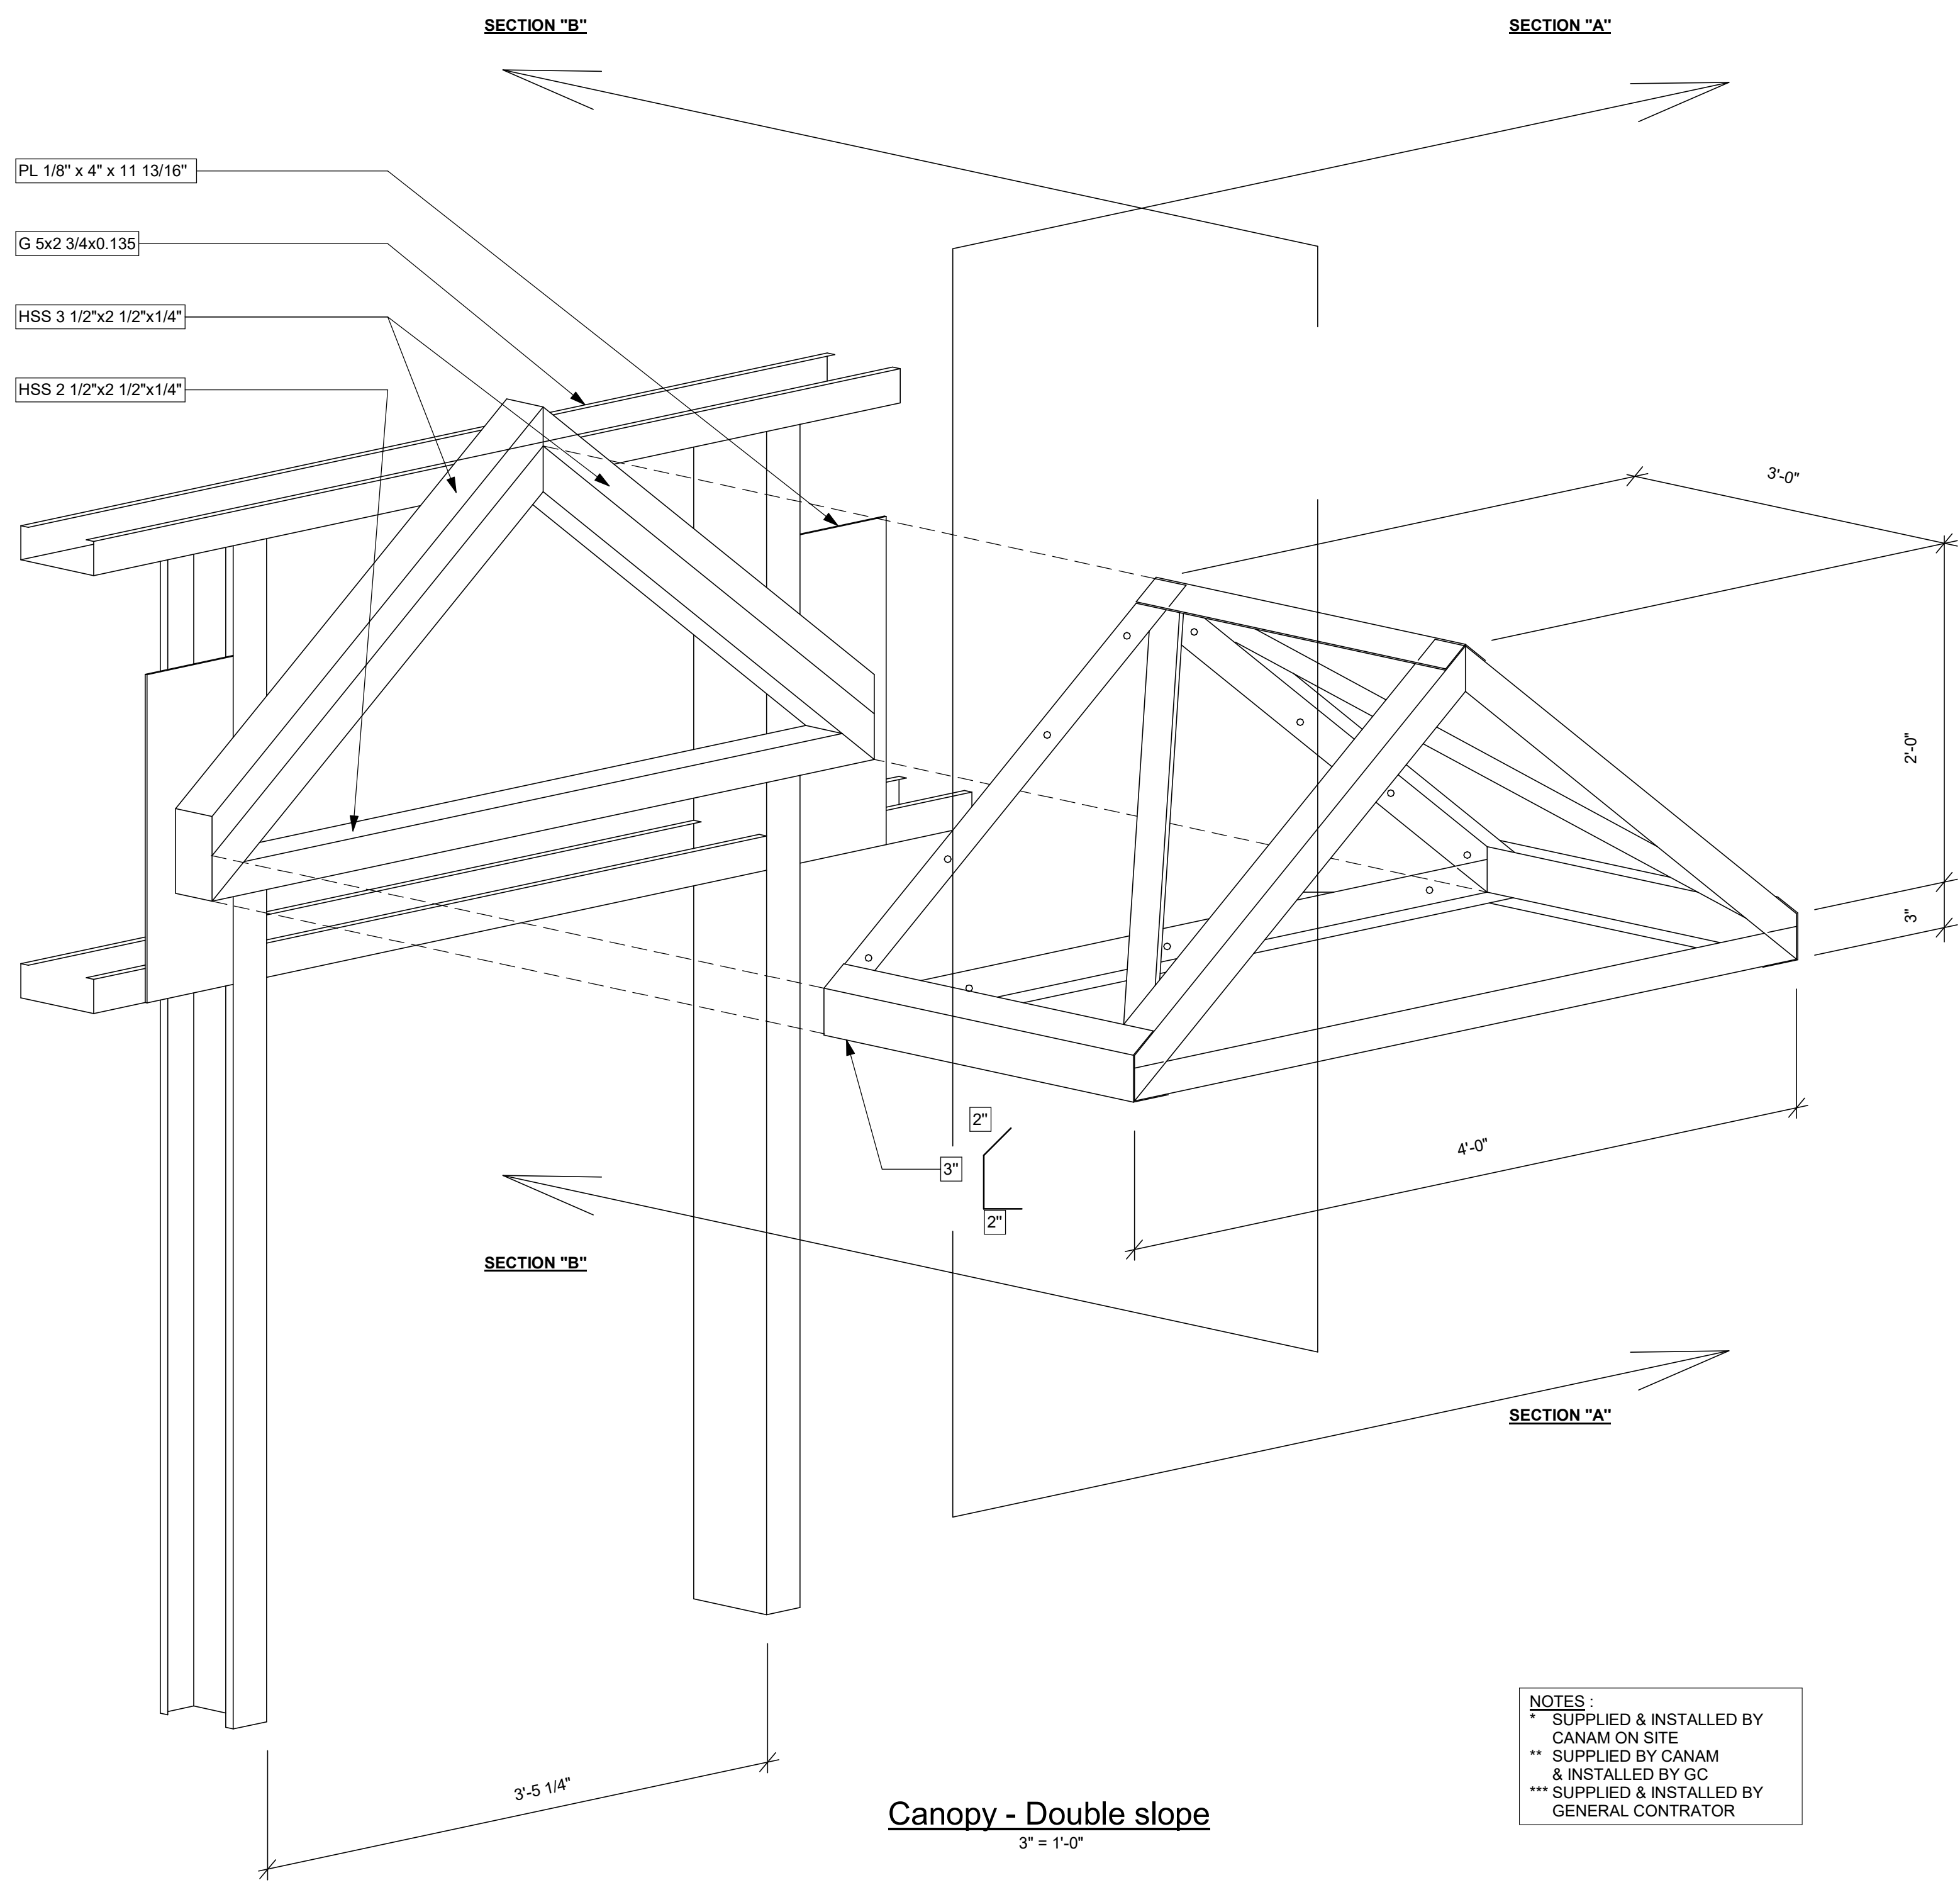


Canopy - Double slope
3" = 1'-0"


NOTES:
** SUPPLIED & INSTALLED BY CANAM ON SITE
** SUPPLIED BY CANAM & INSTALLED BY GC
*** SUPPLIED & INSTALLED BY GENERAL CONTRATOR

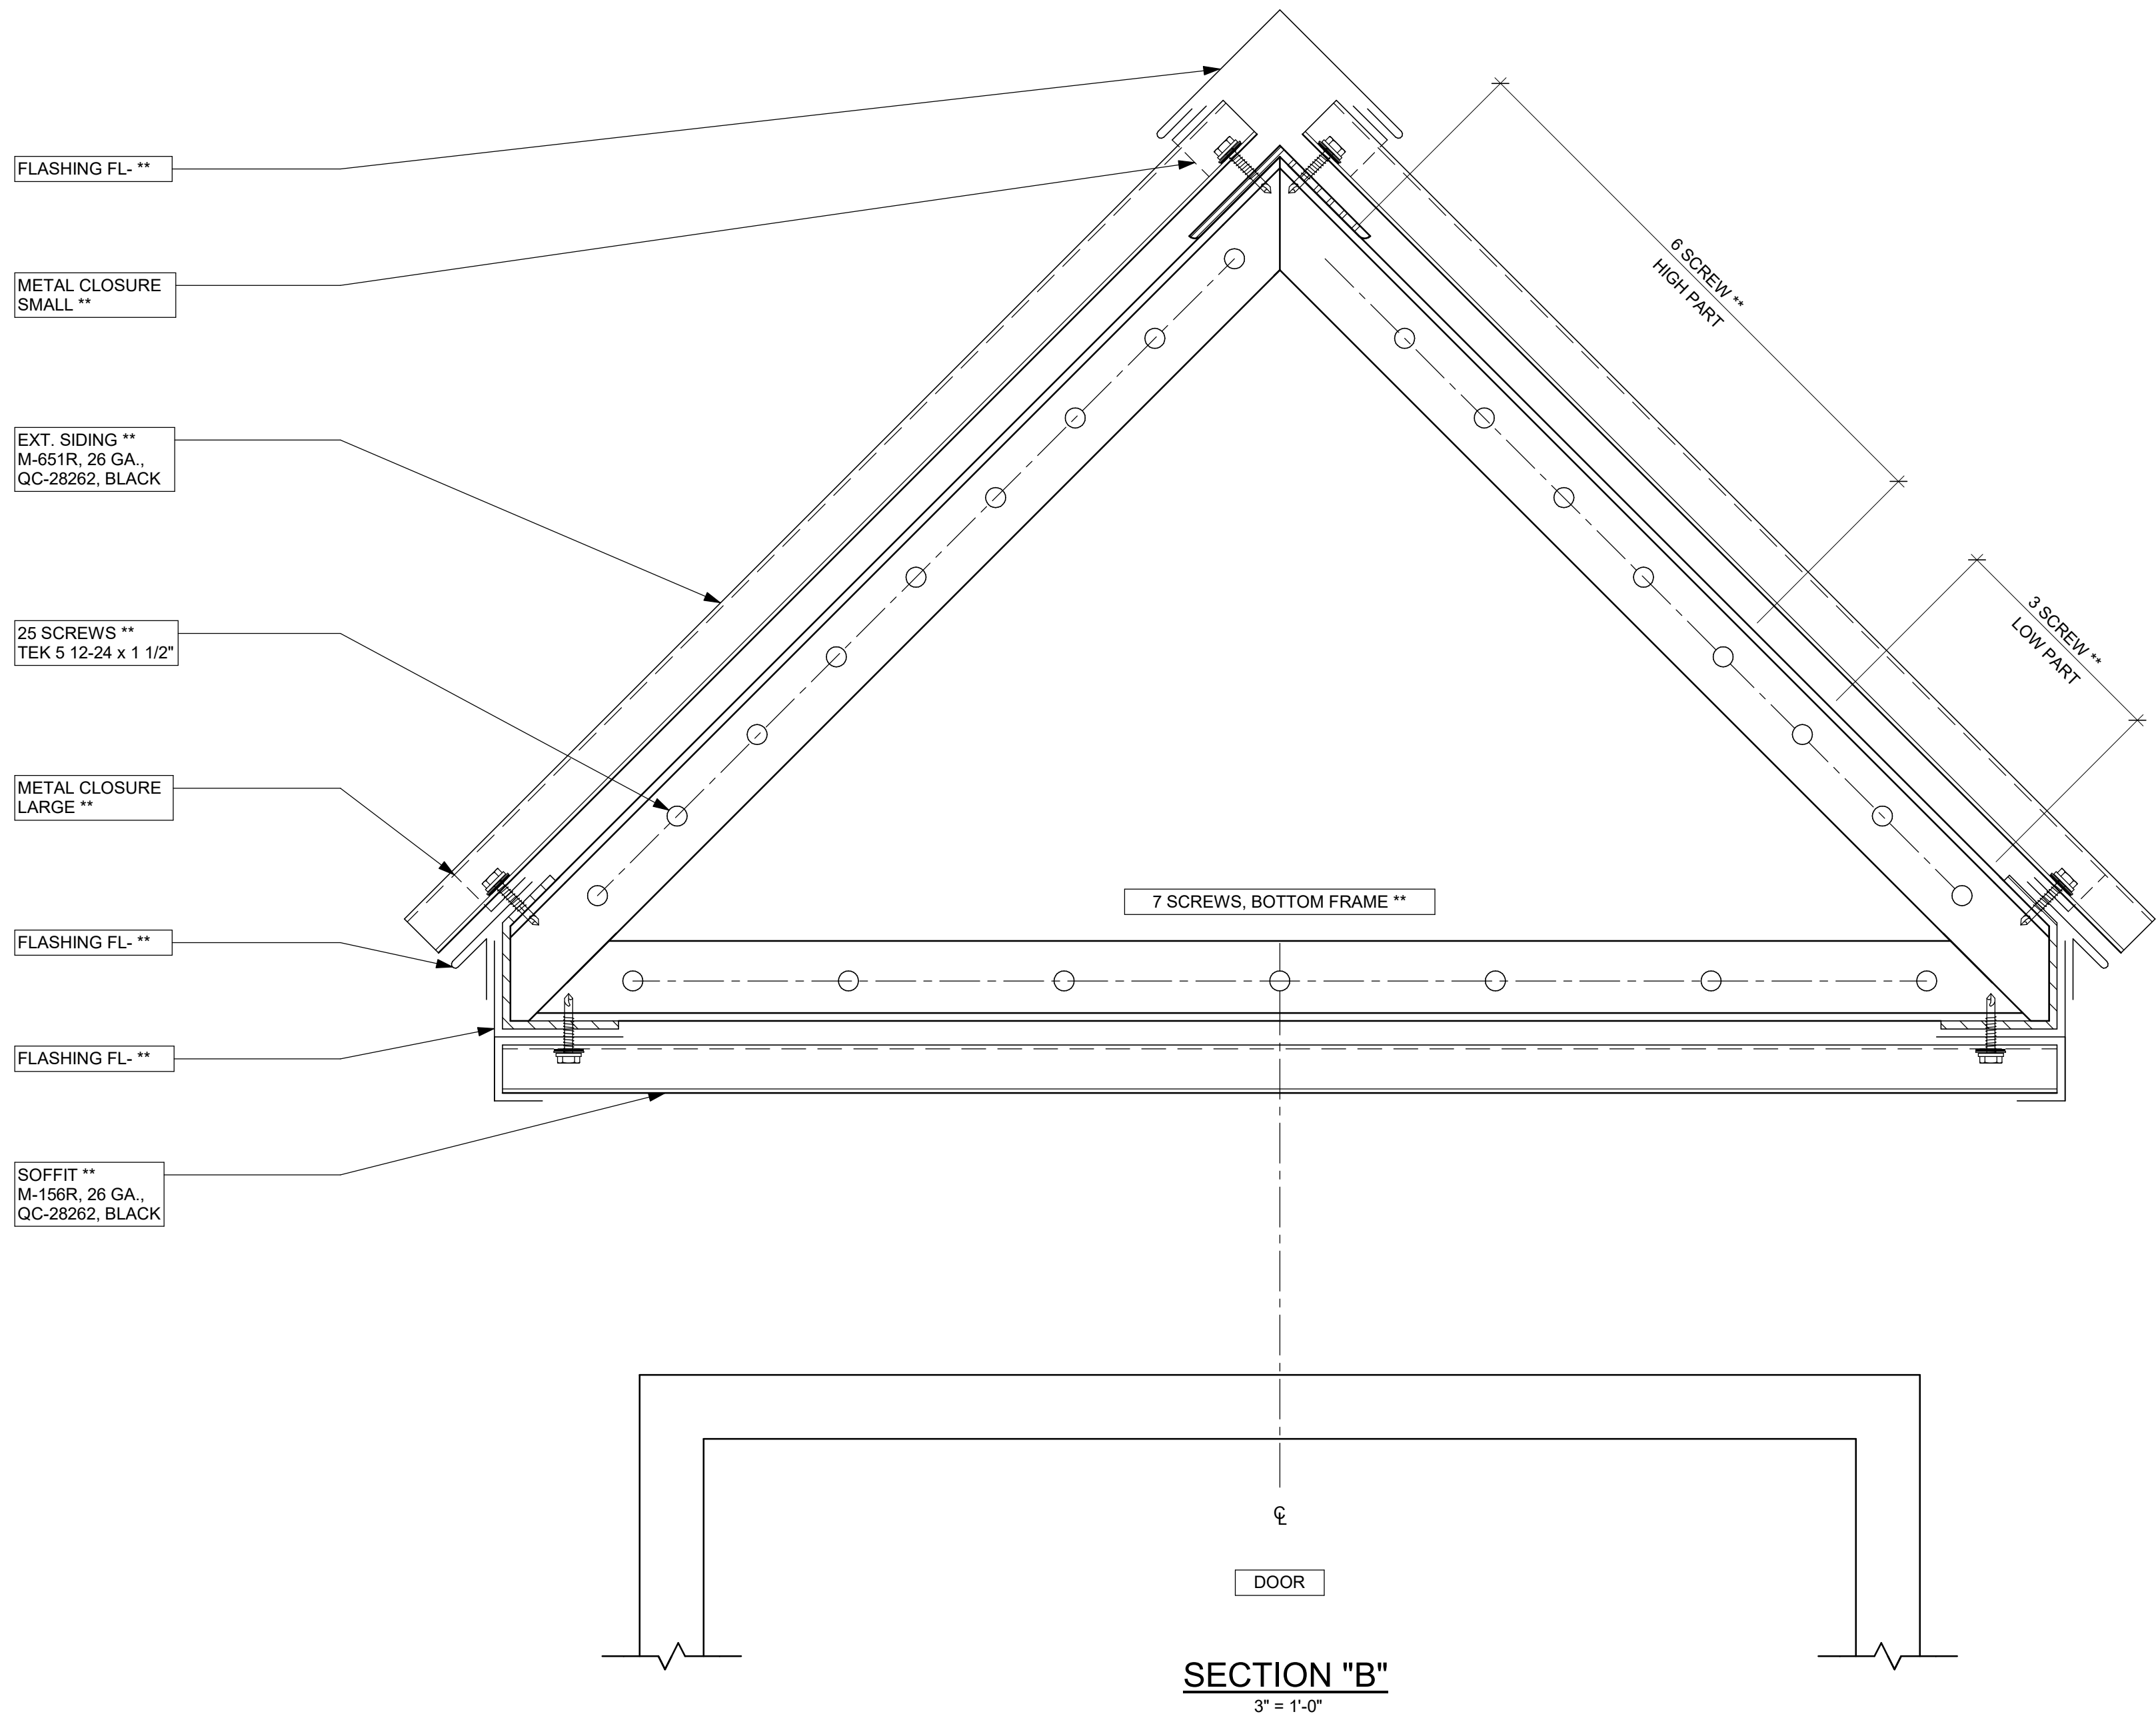

SECTION "B"
3" = 1'-0"

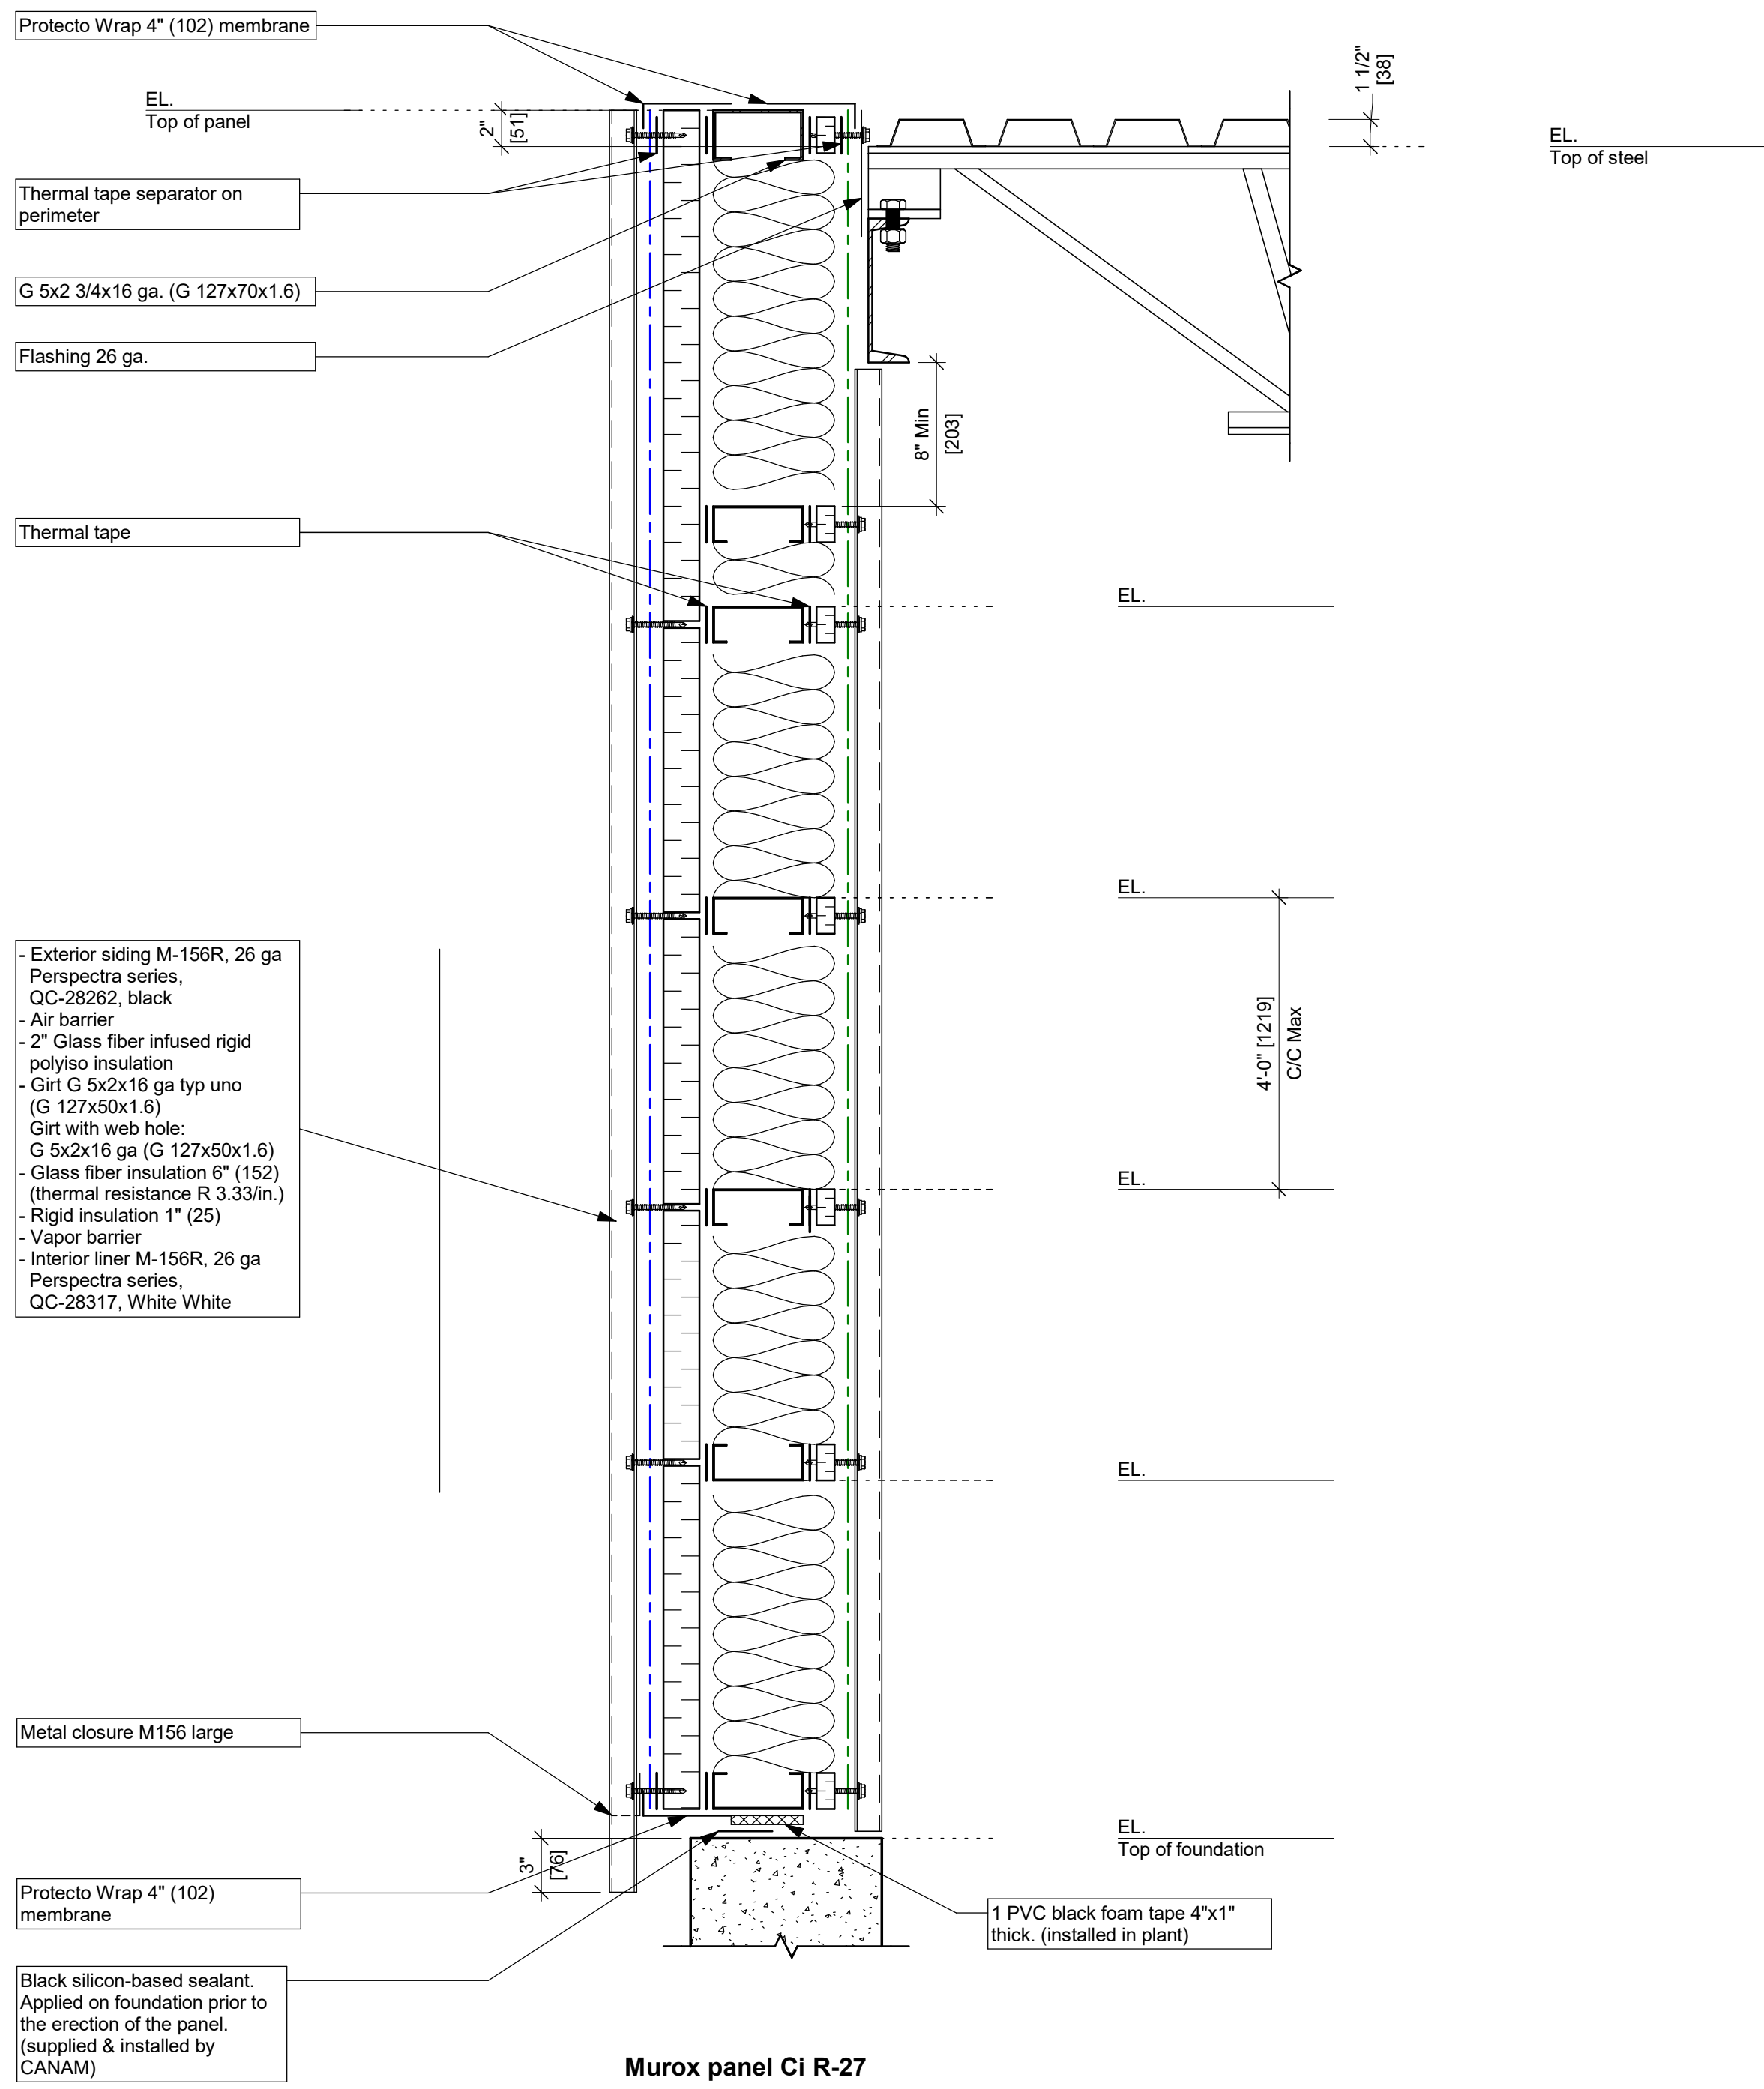

Murox panel CI R-27

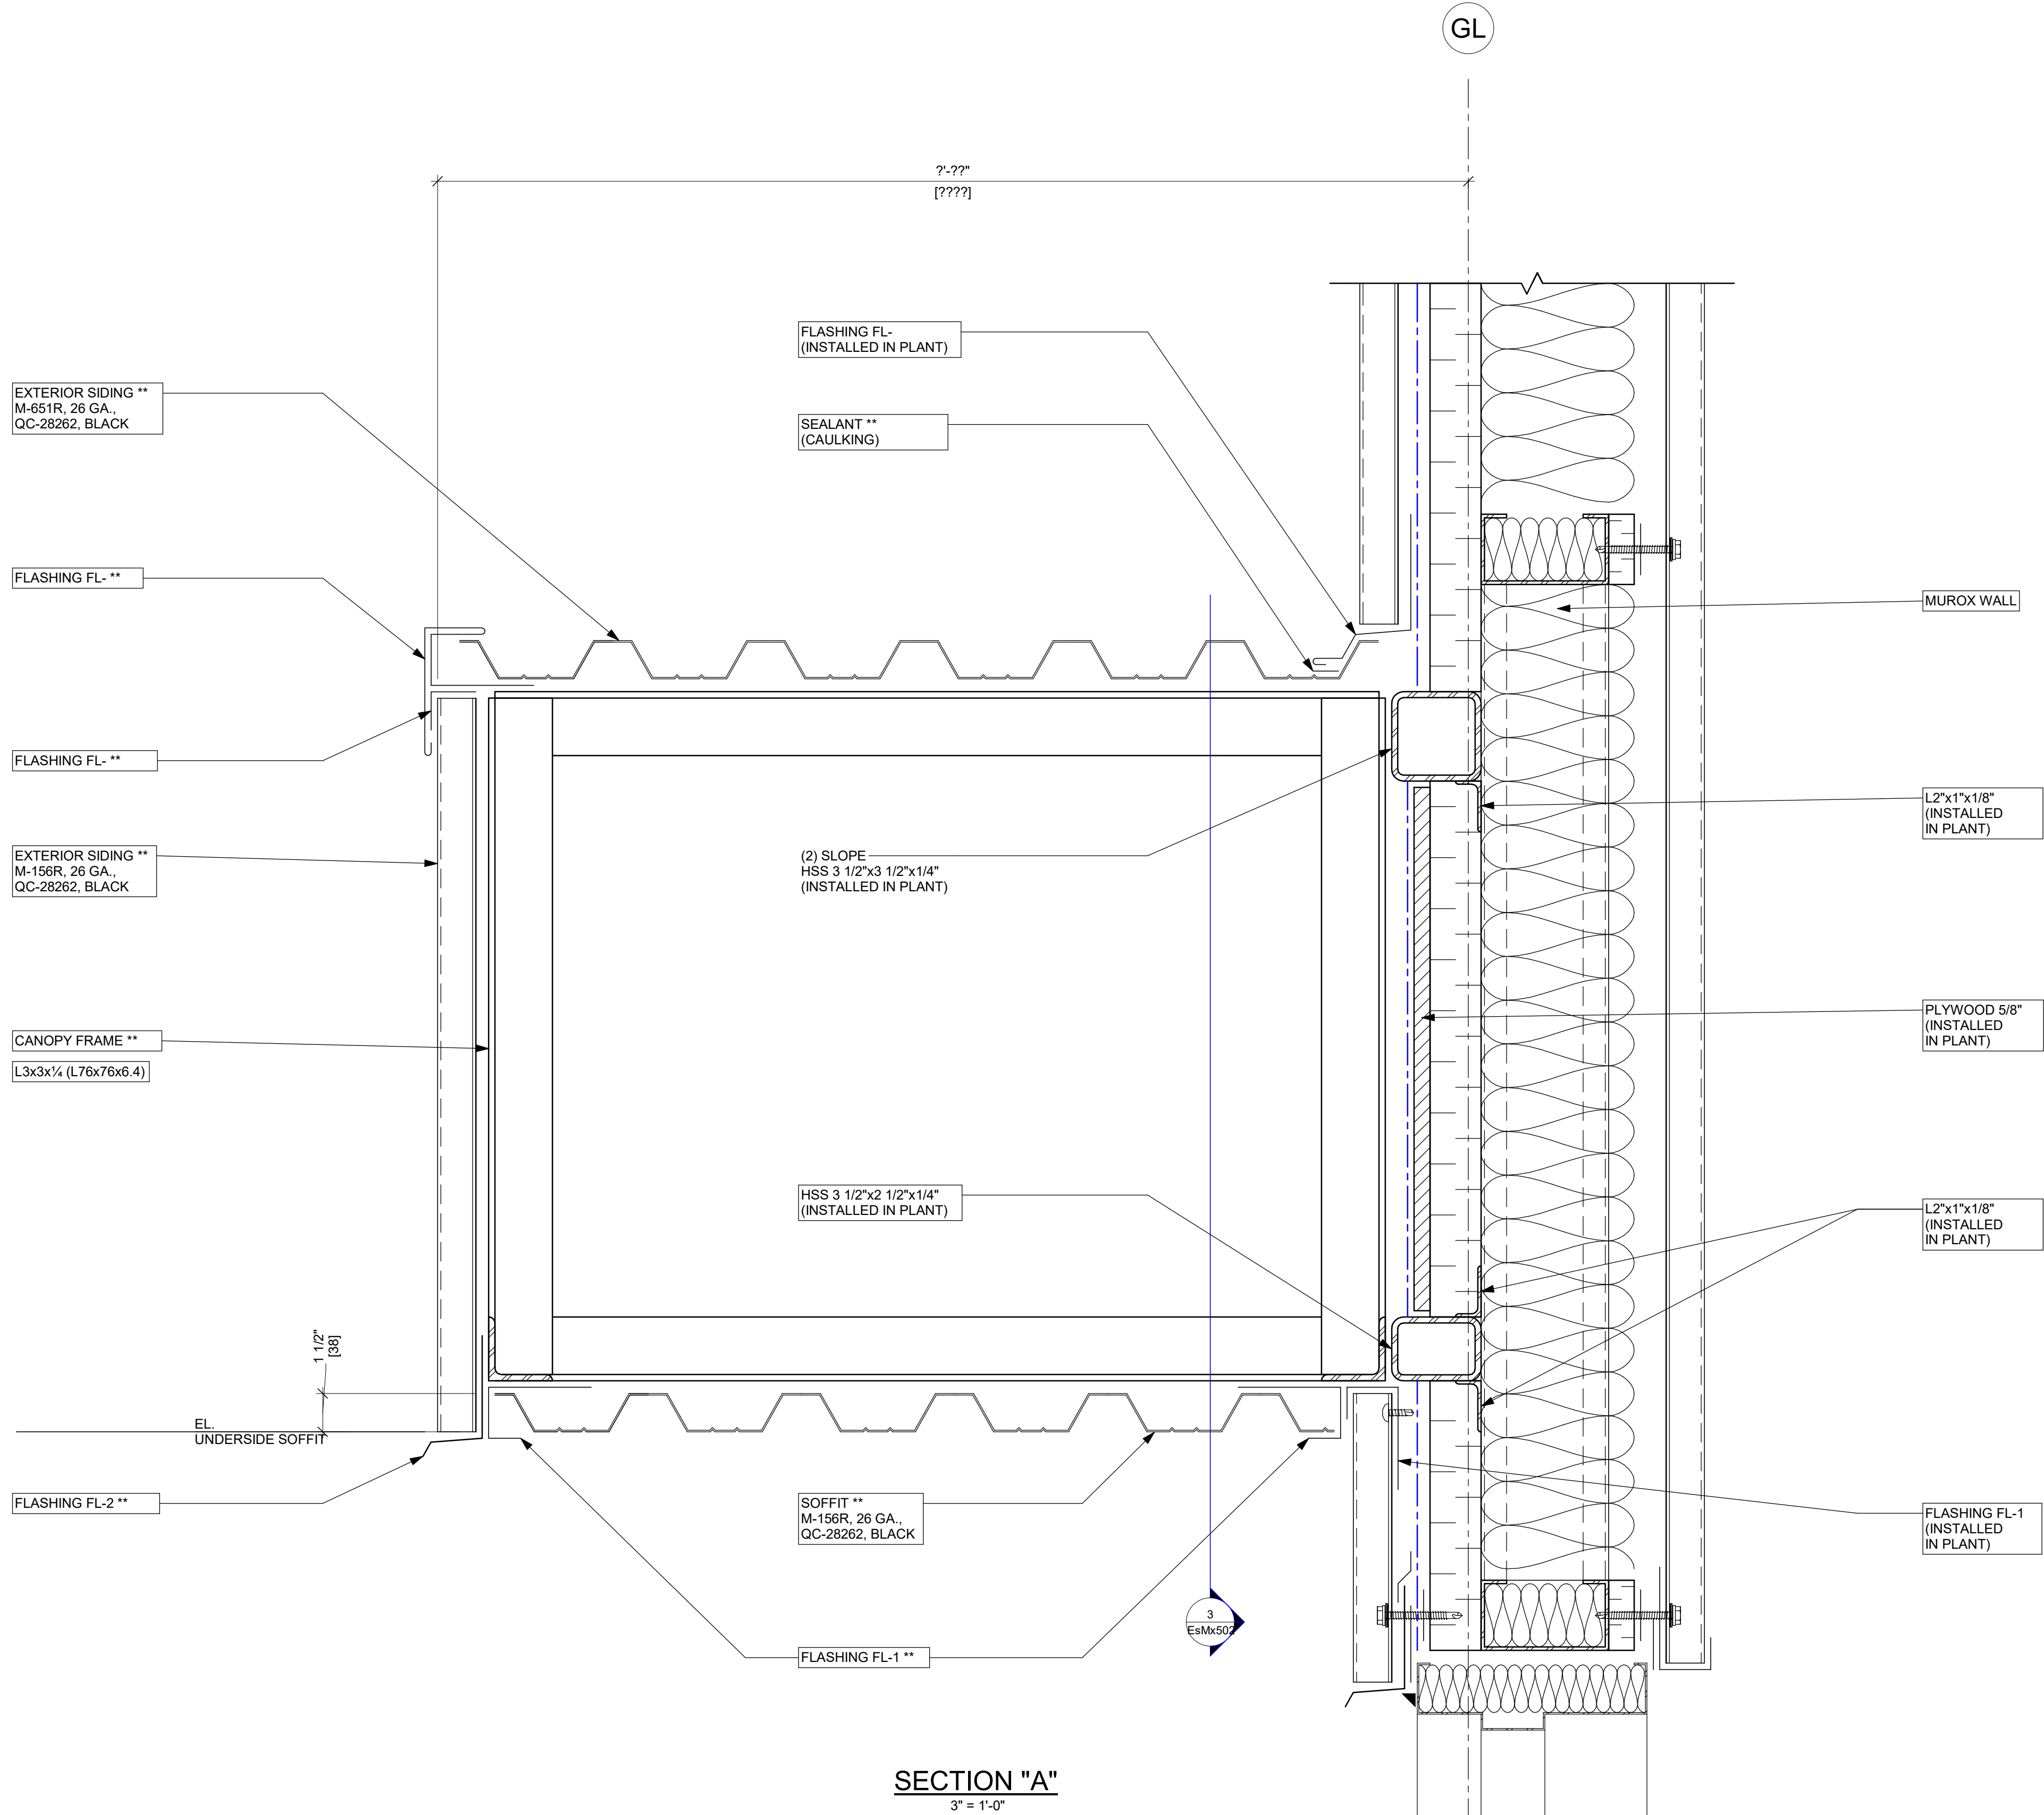

SECTION "A"
3" = 1'-0"

CONTRACTOR/RECTOR NOTE:
IT IS PROHIBITED TO MODIFY, COPY, REPRODUCE OR OTHERWISE DISTRIBUTE THIS DRAWING OR ANY REPRESENTATION OF THIS DRAWING OR ANY MEDIA, INCLUDING ELECTRONIC, WITHOUT THE PRIOR WRITTEN APPROVAL OF CANAM GROUP INC.

PRELIMINARY

NOT TO BE USED FOR CONSTRUCTION

REVISION	DATE	DESCRIPTION	ISSUE	VER
PROJECT MANAGER				
DRAFTING				
DESIGNED				
PROJECT ENGINEER				
SCALE				
INITIALE				
CHECKED				
CONSULTING ENGINEERS ARCHITECTS				
DATE (yyyy/mm/dd)				
2028/04/20				

CUSTOMER:
CANAM
11505, 1re Avenue, bureau 500, Saint-Georges Beauce
Quebec, Canada, G5V 7G3
Phone : (418) 228-8031
Toll free : (877) 499-6049
www.canam.com

PROFESSIONAL SEAL
PROJECT
ESTEVAN, SASKATCHEWAN

DRAWING TITLE
PRELIMINARY SKETCH - ELEVATION,
WALL SECTION AND SCHEDULES

CONTRACT NUMBER	DRAWING NUMBER	DIVISION	REVISION
P2026-079	EsMx502		