



9/8/2023 6:11:26 PM Autodesk Docs://1230237 Port Wentworth Fire Station/1230237_Port Wentworth FS_ARCH_V23.rvt


D
C
B
A

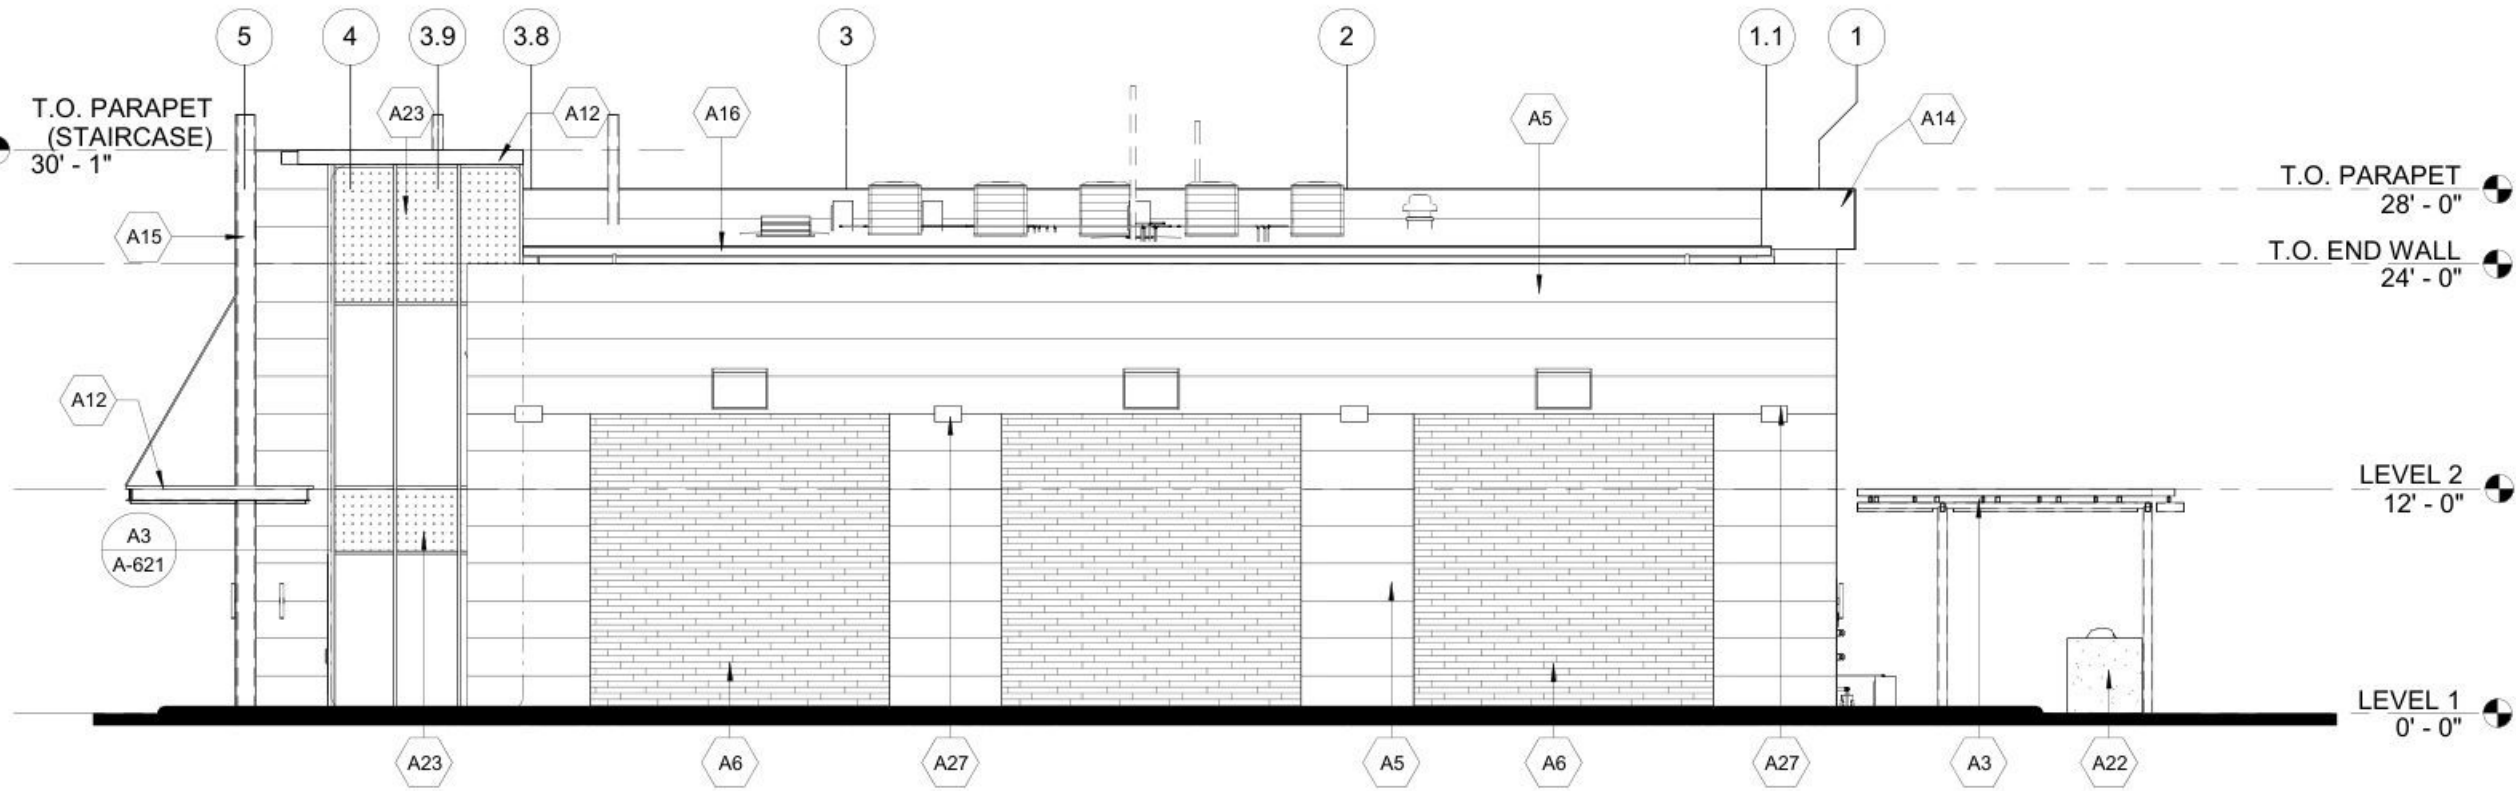

C1 EAST ELEVATION
SCALE: 1/8" = 1'-0"

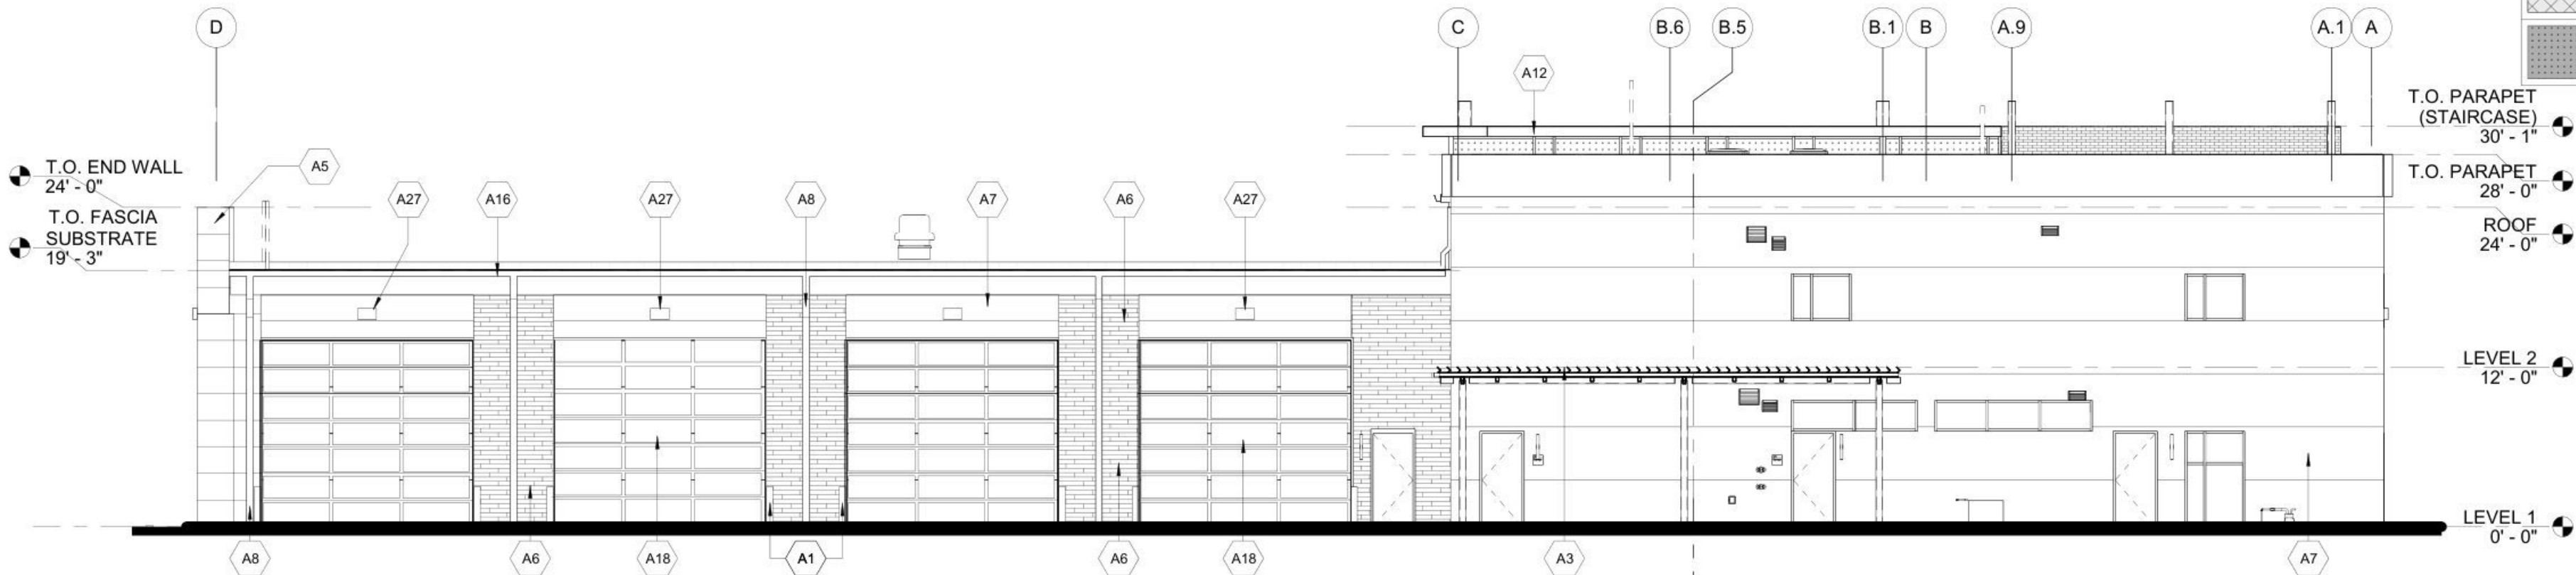

A1 NORTH ELEVATION
SCALE: 1/8" = 1'-0"

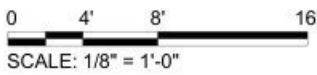

SHEET NOTES

- SEE SHEET A-001 FOR GENERAL NOTES
- SEE SHEET A-601 FOR DOOR SCHEDULE AND TYPES.
- SEE SHEET A-621 STOREFRONT ELEVATIONS.
- SEE CIVIL, STRUCTURAL, MECHANICAL, PLUMBING, AND ELECTRICAL DRAWINGS FOR MORE INFORMATION.
- ELEVATIONS GIVEN ARE RELATIVE TO GROUND LEVEL T.O. SLAB (0'-0"). SEE CIVIL FOR ABOVE MEAN SEA LEVEL.
- SEE PLANS AND WALL SECTIONS FOR ROUGH OPENING LOCATIONS, WINDOW & STOREFRONT TYPES.
- EXTERIOR STOREFRONT GLAZING TO BE INSULATED <GL-1>, UNLESS NOTED OTHERWISE.
- VERIFY WITH AHJ FOR SITE REQUIREMENTS FOR TEMPERED INSULATED GLAZING BEFORE IMPLEMENTING.
- FIXED INSULATED GLAZING SHALL BE CERTIFIED & LABELED WITH ITS MAX U-FACTOR & SOLAR HEAT GAIN COEFFICIENT BY AN INDEPENDENT AGENCY LICENSED BY THE NFRC (NATIONAL FENESTRATION RATING COUNCIL), IN COMPLIANCE WITH THE VALUES LISTED IN THE DESIGN CRITERIA.
- VERTICAL DIMENSIONS ARE FROM FINISHED FLOOR (T.O. SLAB), UNLESS NOTED OTHERWISE.

KEYNOTES

- A1 BOLLARDS
- A3 PERGOLA
- A5 FIBER CEMENT BOARD PLANKS
- A6 SPLIT-FACE CMU VENEER
- A7 METAL SIDING WALL PANELS
- A8 DOWNSPOUT 6x4
- A12 METAL SUNSCREEN
- A14 FASCIA
- A15 SUNSCREEN STEEL FRAME
- A16 GUTTER 8x8
- A18 APPARATUS BAY DOOR
- A22 LOW WALL
- A23 SPANDREL GLAZING
- A27 LIGHTING FIXTURE

LEGEND

MARK	DESCRIPTION	BASIS OF DESIGN
AS-1	ALUMINUM STOREFRONT SYSTEM	CLEAR ANODIZED
AS-2	ALUMINUM STOREFRONT SYSTEM - FLUOROPOLYMER COATING	FIRE ENGINE RED / #ce2029 HEX COLOR CODE
B-1	FIBER CEMENT BOARD PLANK	MAROON/ BURGUNDY - TYP
B-2	METAL SIDING WALL PANELS	DARK GRAY/ ROCK GRAY/ SLATE/ KHAKI
PRE-1	SPLIT-FACE CMU VENEER	BEIGE/ TAN/ PEARL/ OYSTER - TYP
	SPANDREL GLAZING	SEMI-OPAQUE BLUE-GRAY WITH PATTERN

POND

3500 Parkway Lane
Suite 500
Peachtree Corners
Georgia 30092

Copyright © 2023 by Pond & Company. All rights reserved. No copying or duplication of these documents is allowed without the expressed written agreement of Pond & Company.

EOR/AOR SEAL

100% DESIGN
SUBMITTAL - NOT FOR
CONSTRUCTION

CLIENT INFORMATION

City of Port
Wentworth Fire
Rescue

PROJECT NAME

PORT
WENTWORTH
FIRE STATION



DRAWING ISSUE

DATE

DESCRIPTION

MARK

DESIGNED BY: C.L
DRAWN BY: C.L
CHECKED BY: I.P
SUBMITTED BY: M.M
DATE: 9/08/2023
PROJECT #: 1230237

SHEET TITLE

EXTERIOR
ELEVATIONS

SHEET NUMBER

A-201

ORIGINAL SHEET SIZE:
22" X 34"

100% DESIGN SUBMITTAL - NOT FOR CONSTRUCTION