


9/8/2023 12:55:19 PM Autodesks Docs/1230237 Port Wentworth Fire Station/1230237_Port Wentworth FS_STRC_v23.rvt

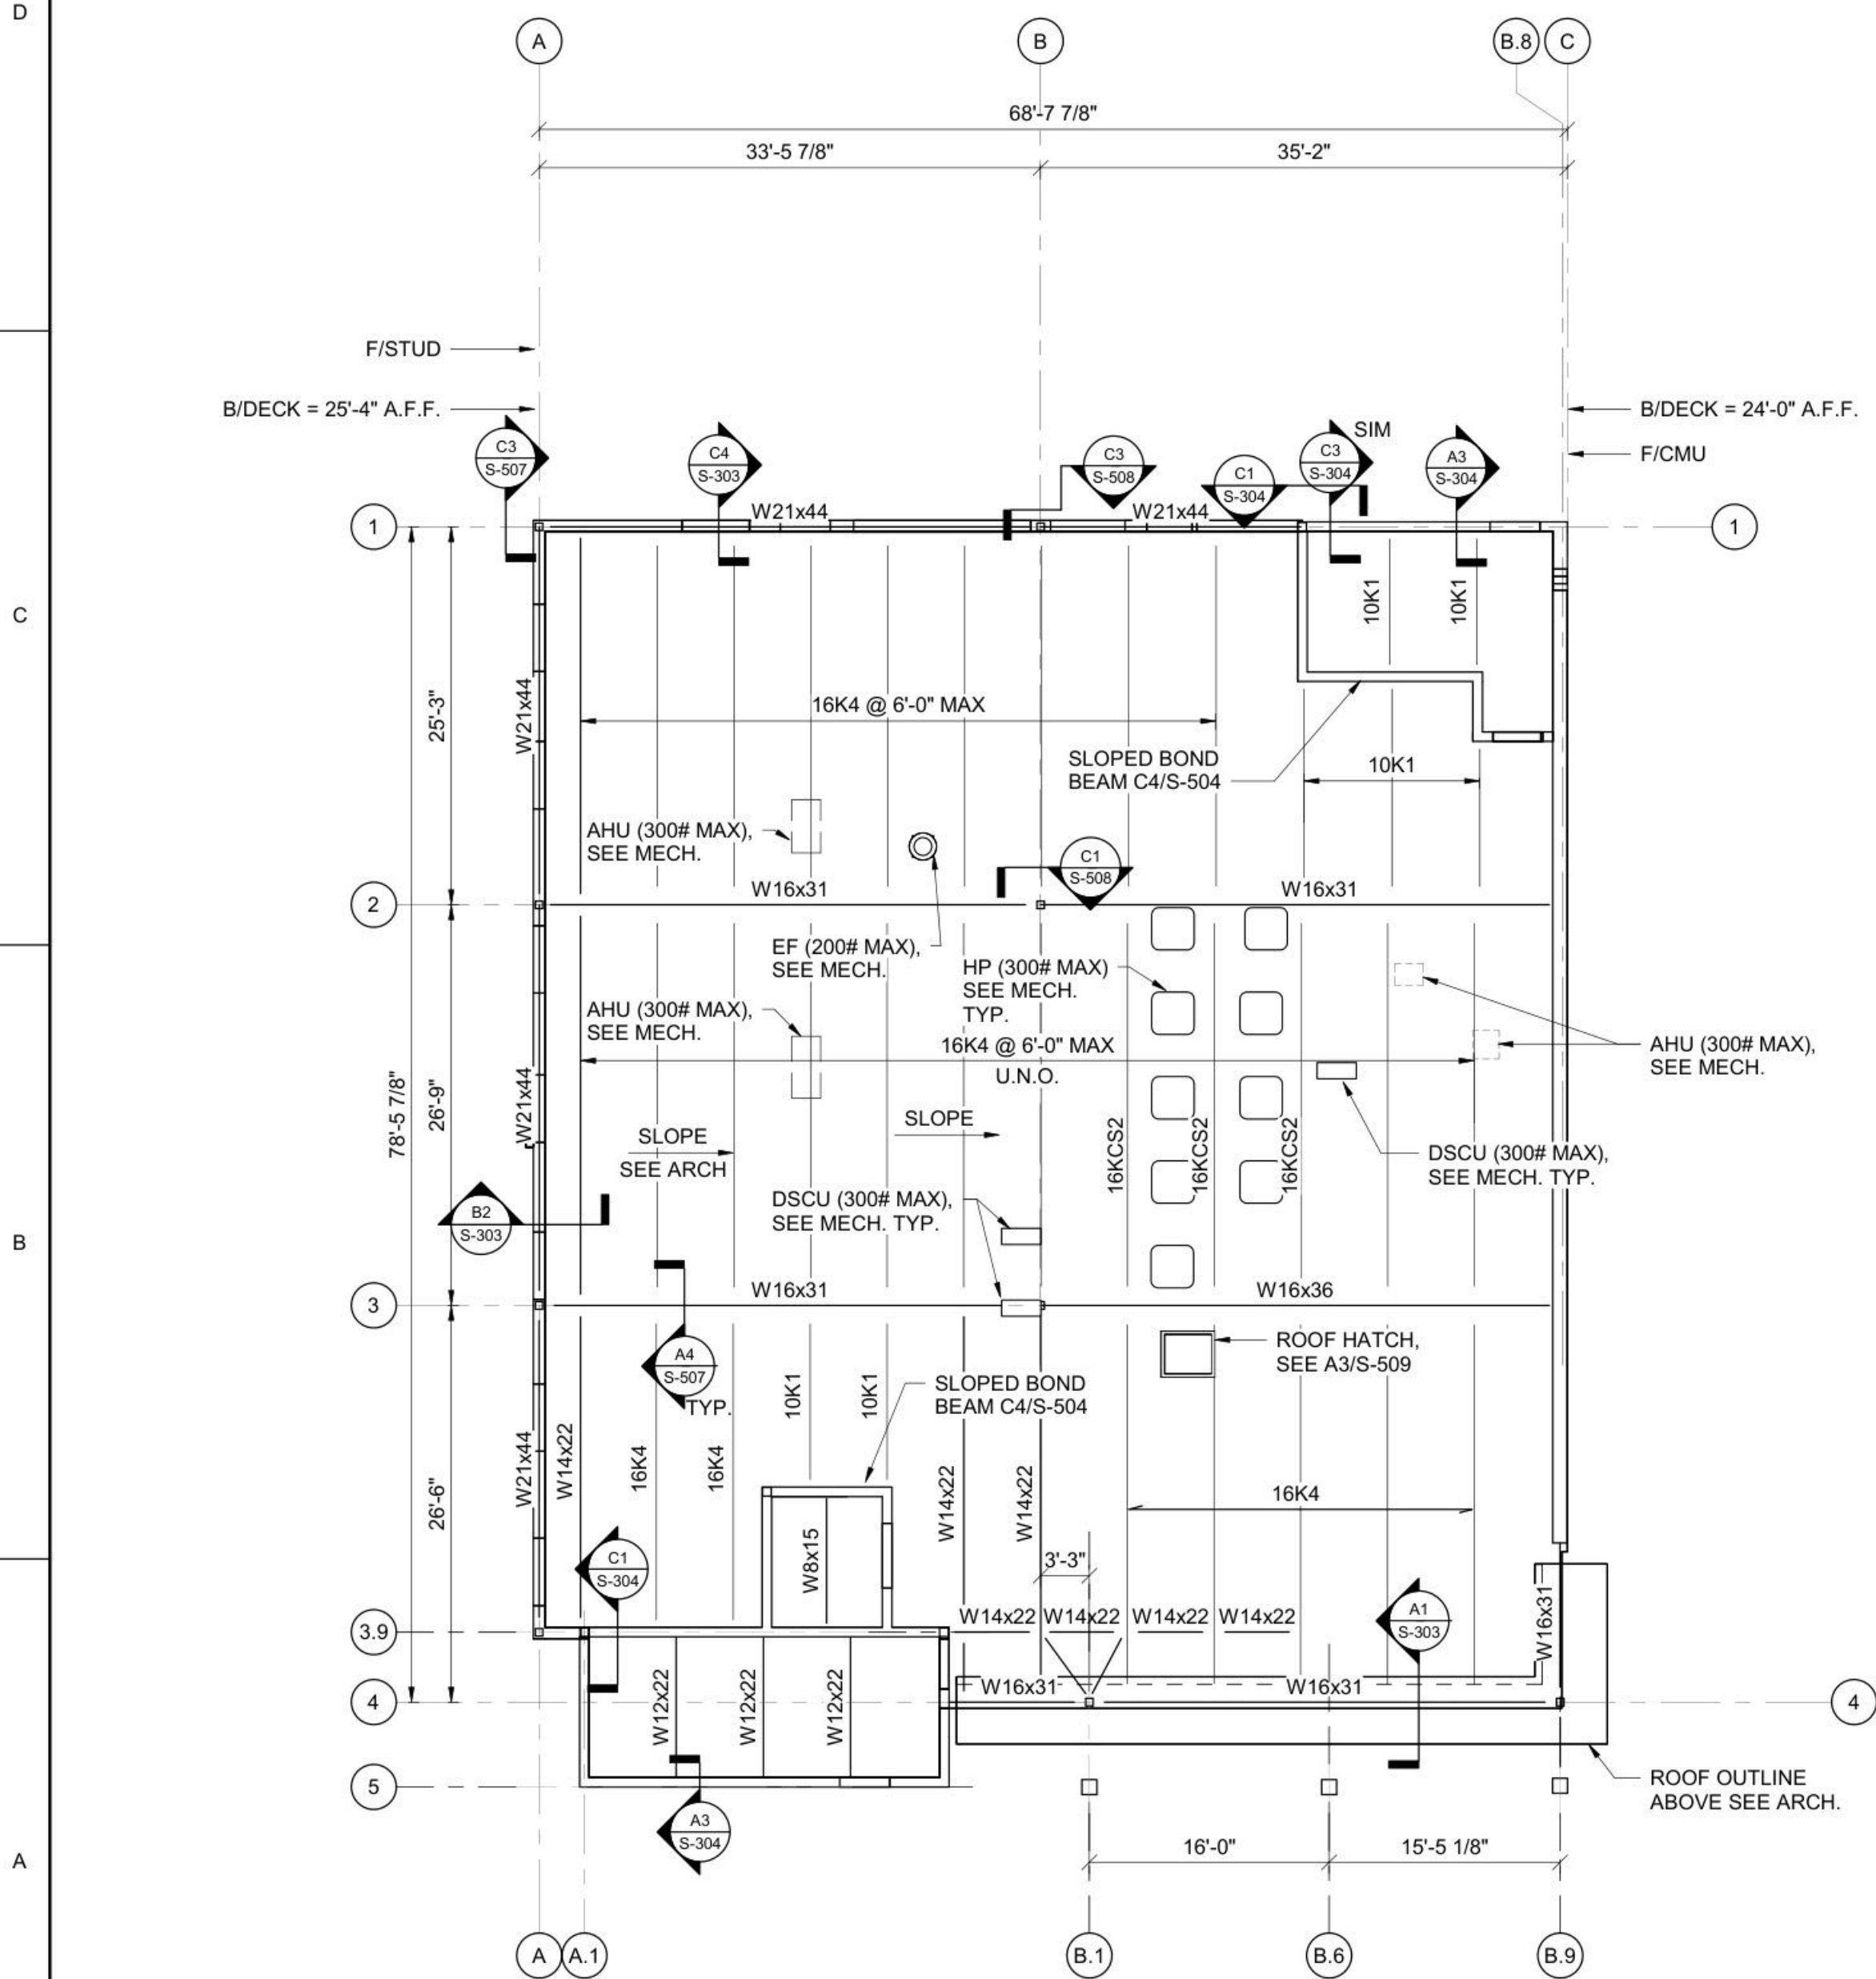


A1 ROOF FRAMING PLAN
SCALE: 1/8" = 1'-0"

ROOF FRAMING PLAN NOTES:

- SEE SHEETS S-001 AND S-002 FOR GENERAL STRUCTURAL NOTES, BEAM LEGEND, AND ABBREVIATION KEY.
- SEE SHEET S-507, S-508 & S-509 FOR TYPICAL STEEL DETAILS.
- SEE NOTE D ON S-001 FOR DELEGATED CONNECTION DESIGN REQUIREMENTS.
- ALL CONNECTION DESIGN LOADS ARE SERVICE (ASD) LOADS.
- ROOF DECK AND ATTACHMENT SHALL BE OF THE TYPE SPECIFIED IN GENERAL NOTE H ON SHEET S-002 AND DETAIL D1/S-505.
- ROOF BEAMS AND ROOF JOISTS SHALL BE EQUALLY SPACED BETWEEN COLUMN LINES, UNLESS NOTED OTHERWISE.
- PROVIDE JOIST BRIDGING IN ACCORDANCE WITH ALL SJI STANDARDS INCLUDING WIND UPLIFT BRIDGING.
- ROOF JOISTS SHALL HAVE 2 1/2" MIN. DEEP SEATS, UNLESS NOTED OTHERWISE.
- MECHANICAL DUCTWORK SHALL BE SUPPORTED BY ROOF STRUCTURE ABOVE PER DETAILS A1/S-508 & A2/S-508. JOISTS SHALL BE REINFORCED PER A4/S-508 UNLESS SUPPORT POINTS ARE LOCATED WITHIN 4" OF PANEL POINTS. MAXIMUM SPACING OF DUCT SUPPORTS SHALL BE LESSER OF 10'-0" O.C. OR MAXIMUM SPANS PERMITTED BY MECH. AND/OR SMACNA DUCT CONSTRUCTION STANDARDS.
- MAXIMUM OPERATING WEIGHT OF THE SELECTED EQUIPMENT SHALL BE VERIFIED AND COORDINATED W/ THE DESIGN WEIGHTS INDICATED ON PLAN BY THE CONSTRUCTION PROFESSIONAL. THIS SHALL BE COMPLETED BEFORE THE PROCUREMENT OF ANY MATERIALS AND EQUIPMENT AND THE DEVELOPMENT OF ANY SHOP DRAWINGS OR SUBMITTALS.
- NOT ALL MECHANICAL EQUIPMENT IS SHOWN. ONLY LARGER EQUIPMENT WITH THE MAXIMUM OPERATING WEIGHTS USED FOR THE STRUCTURAL DESIGN IS INDICATED.

ROOF FRAMING PLAN LEGEND:

- | | |
|------------|---|
| A = # K | AXIAL LOAD IN BEAM FOR CONNECTION DESIGN |
| M = # K-FT | MOMENT LOAD IN BEAM FOR CONNECTION DESIGN |
| | MOMENT CONNECTION |
| --- | BOTTOM CHORD BRACE, SEE DETAIL ###/S-521 |
| ##K#SP | SPECIAL JOIST, SEE DETAIL A1/S-003B |
| → | DIRECTION OF DECK SPAN |
| ↘ | ROOF SLOPE DOWN DIRECTION |
| EOD | EDGE OF DECK |
| ⊠ | ROOF DECK OPENING, SEE DETAIL ###/S-521 |
| ⊠ | CMU WALL |

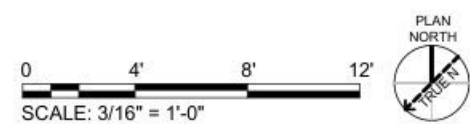

POND
3500 Parkway Lane
Suite 500
Peachtree Corners
Georgia 30092
Copyright © 2023 by Pond & Company. All rights reserved. No copying or duplication of these documents is allowed without the expressed written agreement of Pond & Company.

EOR/AOR SEAL

100% DESIGN
SUBMITTAL - NOT FOR
CONSTRUCTION

CLIENT INFORMATION

CITY OF PORT
WENTWORTH

PROJECT NAME

PORT
WENTWORTH
FIRESTATION



DRAWING ISSUE

DATE

DESCRIPTION

MARK

DESIGNED BY: MJF
DRAWN BY: MJF
CHECKED BY: RGN
SUBMITTED BY: MM
DATE: 9/08/2023
PROJECT #: 1230237

SHEET TITLE

ROOF FRAMING
PLAN

SHEET NUMBER

S-151

ORIGINAL SHEET SIZE:
22" X 34"

100% DESIGN SUBMITTAL - NOT FOR CONSTRUCTION