


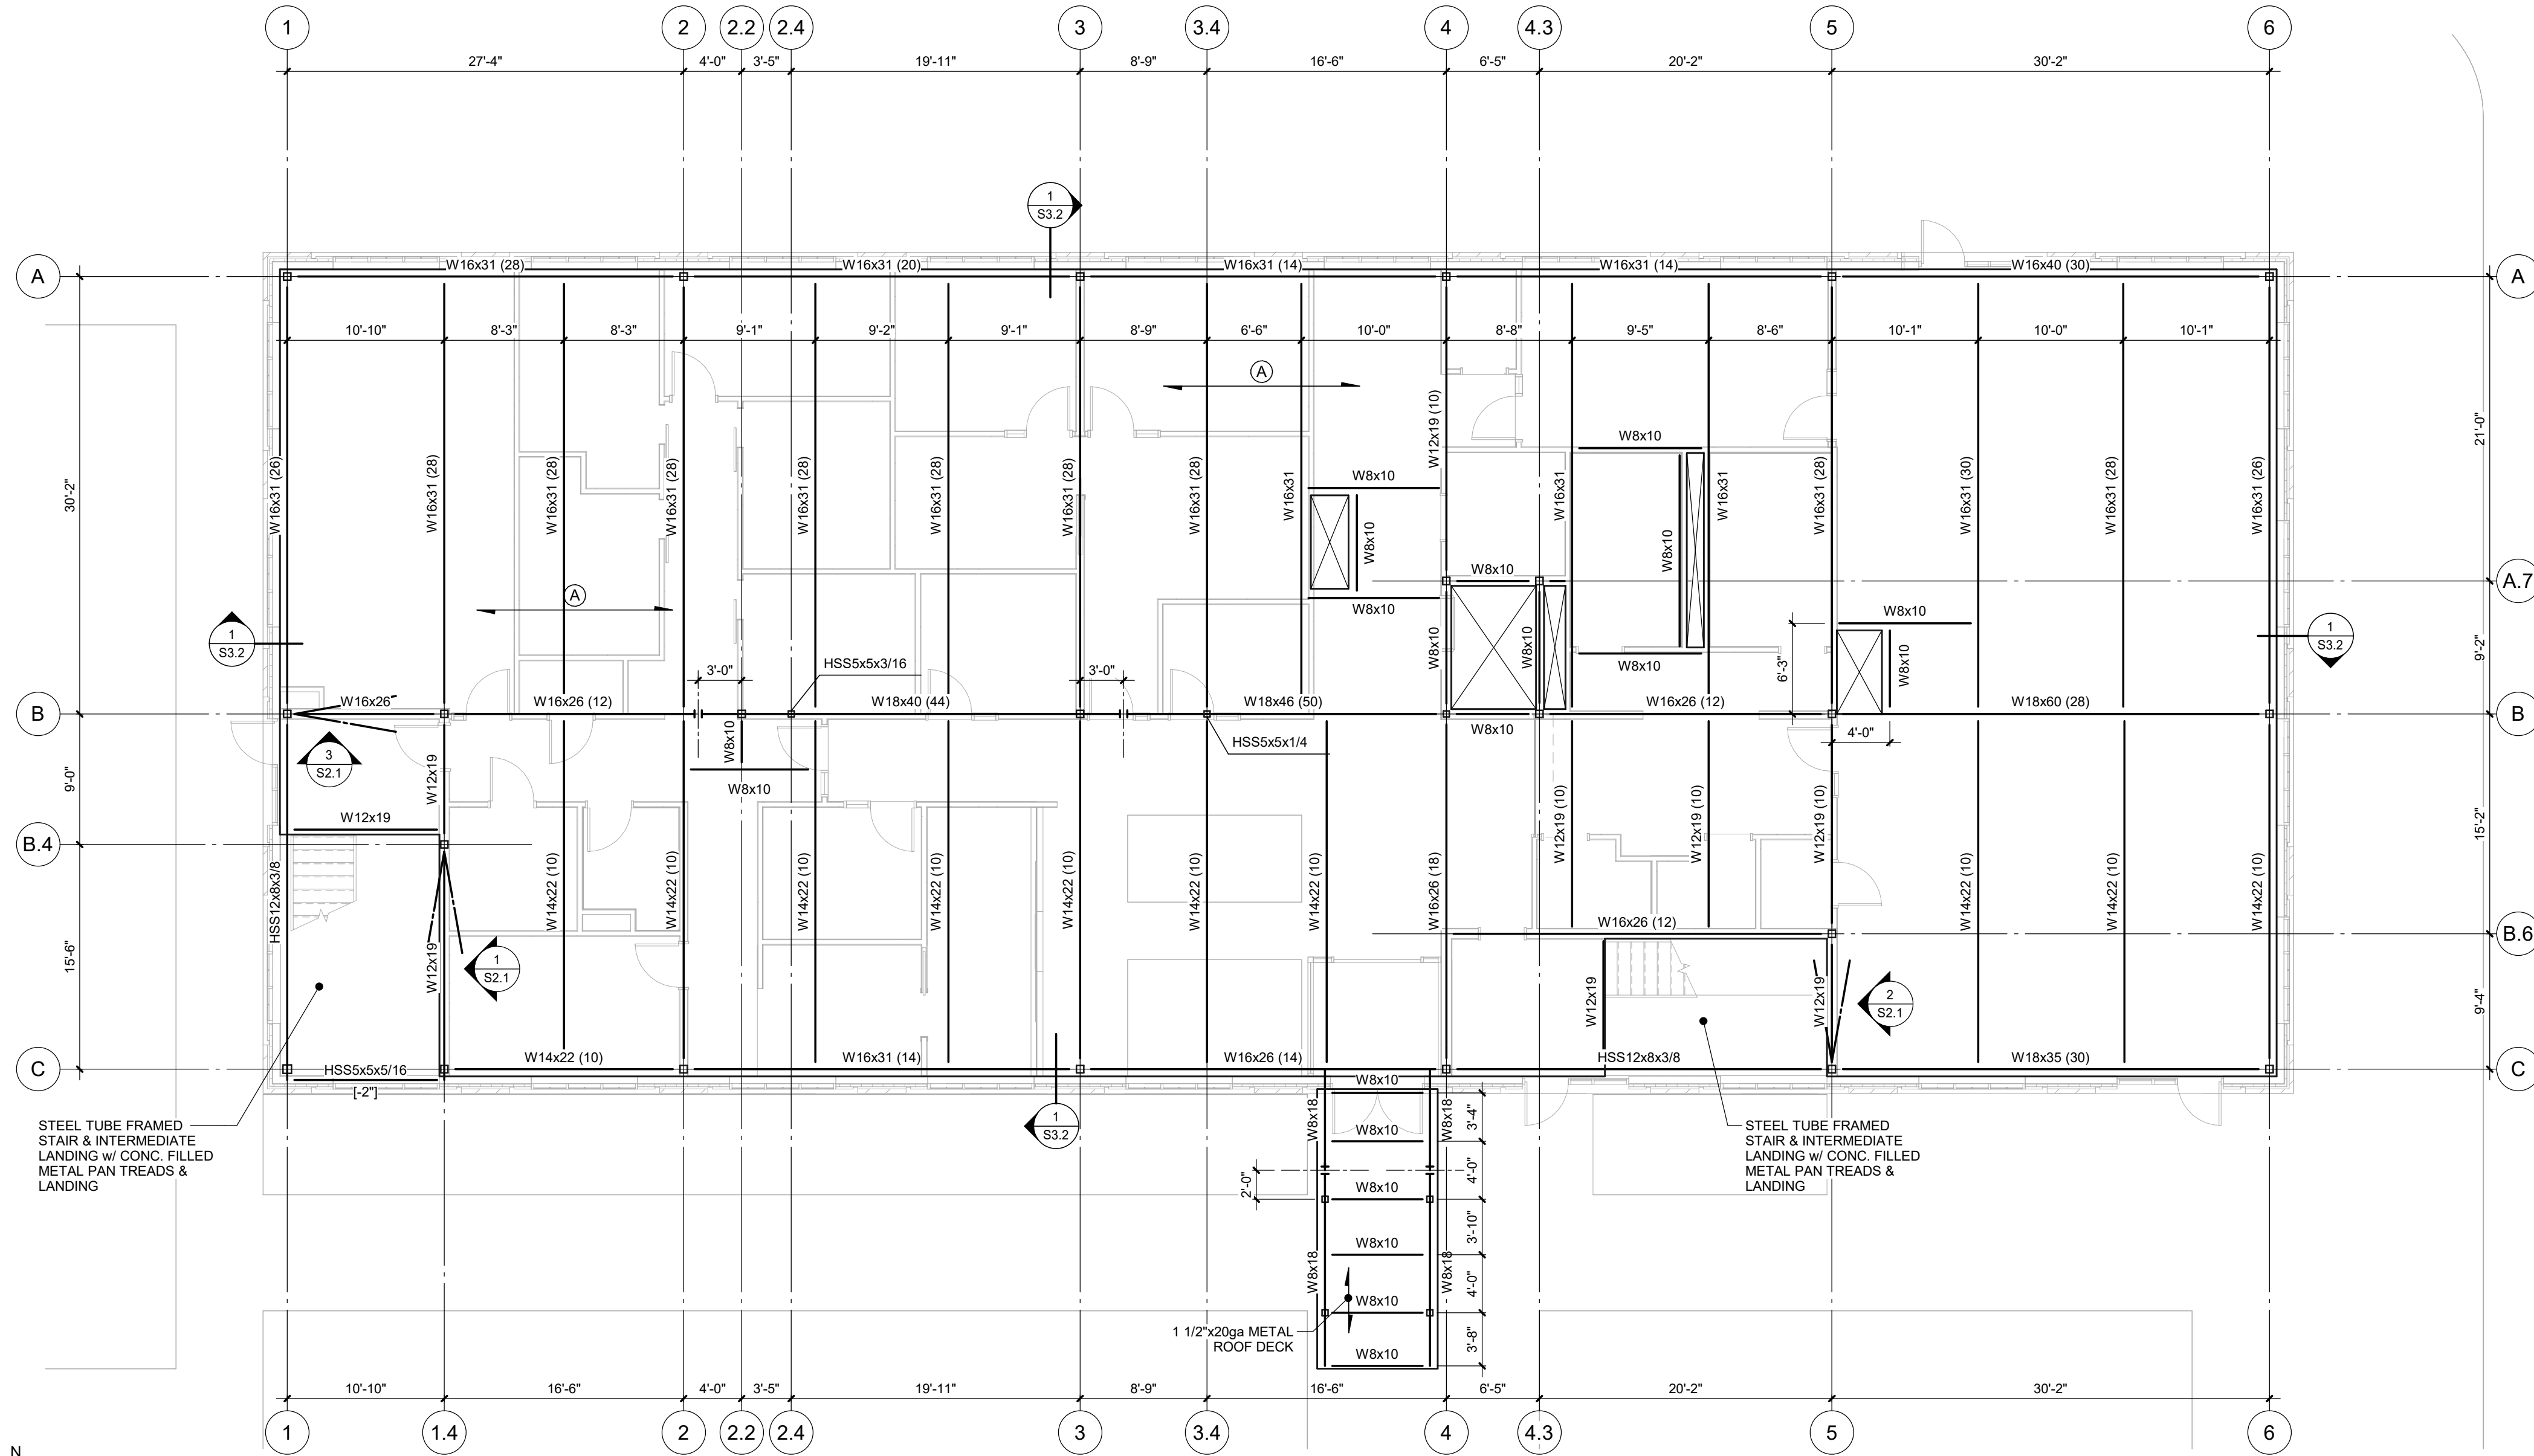

SECOND FLOOR FRAMING PLAN

- SECTION FLOOR FRAMING NOTES:
- SEE STRUCTURAL NOTES ON SHEET S0.0.
 - COORDINATE AND VERIFY ALL DIMENSIONS WITH ARCHITECTURAL DRAWINGS AND EXIST. CONDITIONS.
 - TOP OF STEEL ELEVATION = 114'-2 1/2" UNLESS NOTED OTHERWISE AS SPECIFIC ELEVATIONS THUS:
A. MEMBERS INDICATED AS 14'-x-x" AFTER THE BEAM MARK DESIGNATES A DIFFERENTIAL TOP OF STEEL ELEVATION, OR MEMBERS ARE NOTED THUS: (T.O.S. = x'-xx").
 - INDICATES SPAN DIRECTION OF 2 1/2" CONCRETE SLAB ON 3"-18ga. VULCRAFT "3VL" GALVANIZED COMPOSITE METAL DECK (5 1/2" TOTAL THICKNESS).
REINFORCE SLAB-ON-METAL DECK WITH 8x6 - W4.0 x W4.0 W.W.F. CHAISED 1" CLEAR ABOVE THE TOP OF METAL DECK. AT SPICES, W.W.F. SHALL BE LAPPED (2) MESH SPACES.
W.W.F. SHALL BE SECURED IN CORRECT LOCATION PRIOR TO CONCRETE SLAB PLACEMENT.
- PROVIDE 44% 4'-0" LONG AT 24% c.c. CENTERED OVER STEEL GIRDERS PER ____ TYP.
- SEE PLAN FOR LOCATIONS WHERE ADDITIONAL REBAR IS REQUIRED.
- AT OPENINGS THRU THE SLAB-ON-DECK, REINFORCE THE SLAB PER DETAIL ____.
 - HEADED STUD (H.S.) REQUIREMENTS:
A. STUD SIZE: 3/4"x4" x 4' 3/4" LONG
B. SEE THE BEAM MARK FOR THE NUMBER or SPACING OF HEADED STUDS REQUIRED ON THE BEAM.
C. INSTALL HEADED STUDS AT A UNIFORM SPACING ALONG THE BEAM, TYPICAL.
- AT BEAMS PERPENDICULAR TO THE DECK SPAN, WHERE THE NUMBER OF STUDS DOES NOT ALLOW FOR UNIFORM SPACING IN THE DECK FLUTES, START BY INSTALLING STUDS AT A UNIFORM SPACING ALONG THE ENTIRE BEAM, THEN INSTALL 1/2 OF THE REMAINING STUDS AT AN OVERALL 6" o.c. STUD SPACING AT EACH END OF THE BEAM.
D. SEE DETAIL ____ FOR HEADED STUD DETAILS.
 - STEEL BEAM-TO-BEAM FRAMING CONNECTIONS:
a) SEE ____ FOR BEAM-TO-BEAM SPICE CONNECTION, TYPICAL. BEAM SPICES ARE INDICATED: ____
b) SEE ____ FOR BEAM-TO-BEAM FRAMED CONNECTIONS, TYPICAL UNLESS NOTED OTHERWISE.
c) SEE ____ FOR BEAM-TO-BEAM CONNECTION WHERE LOCATED AT OR NEAR A STEEL COLUMN, TYPICAL.
 - STEEL BEAM-TO-COLUMN FRAMING CONNECTIONS:
a) SEE ____ WHERE BEAM IS FRAMING OVER THE TOP OF A TUBE COLUMN, TYPICAL.
b) SEE ____ WHERE BEAM IS FRAMING INTO THE SIDE OF A TUBE COLUMN, TYPICAL.

AGENCY APPROVAL

ALLEY POYNER
MACCHIETTO
ARCHITECTURE

DESIGN DEVELOPMENT

REVISION	DATE
Project Number:	21064
Date:	March 10, 2023
COPYRIGHT © 2022	

SECOND FLOOR FRAMING
PLAN



TD2 PROJECT # 748-749

S1.2

NOT FOR CONSTRUCTION