



ARCHITECTURE
ENGINEERING
1230 Oakley Street Drive, Suite 100
Clermont, Florida 34711
888.850.FFAE (3323)
www.forefront.com

AR102538-CA30900

ISSUE - REVISION LOG

MARK.	DATE	DESCRIPTION

MARK.	DATE	DESCRIPTION

MARK.	DATE	DESCRIPTION


MARK.	DATE	DESCRIPTION

HOUSING ASSISTANCE PROGRAM - WOODBURY RESIDENCE 826 N WEST 6TH AVE., OCALA, FL 34475	BUILDING SECTIONS
--	-------------------


ANY DISCREPANCY OR ERROR IN DIMENSIONS OR NOTES SHALL BE BROUGHT TO THE ATTENTION OF THE DESIGN PROFESSIONAL FOR CLARIFICATION PRIOR TO COMMENCEMENT OF CONSTRUCTION

JOB #:	25-14622
DATE:	
SHEET NUMBER	

A-301

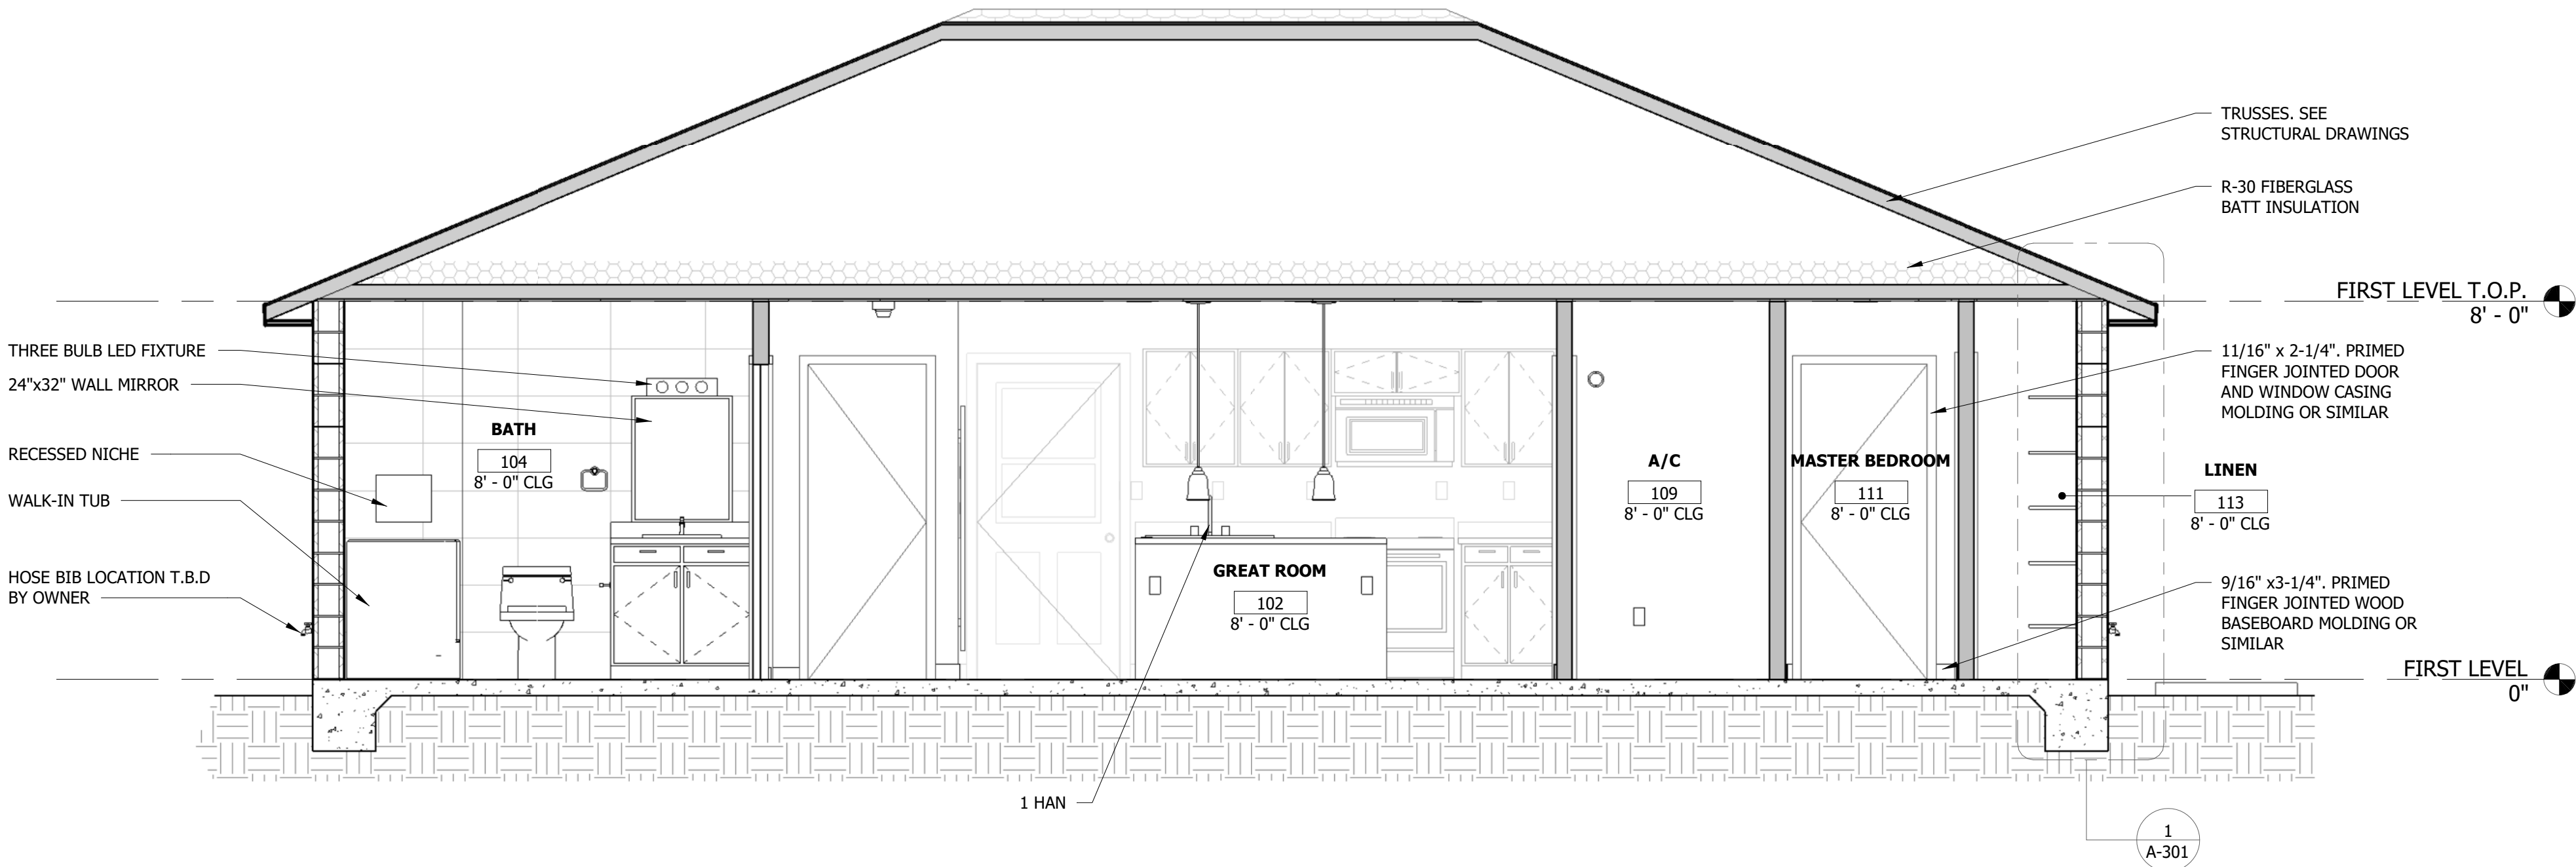

3 BUILDING SECTION B
3/8" = 1'-0"

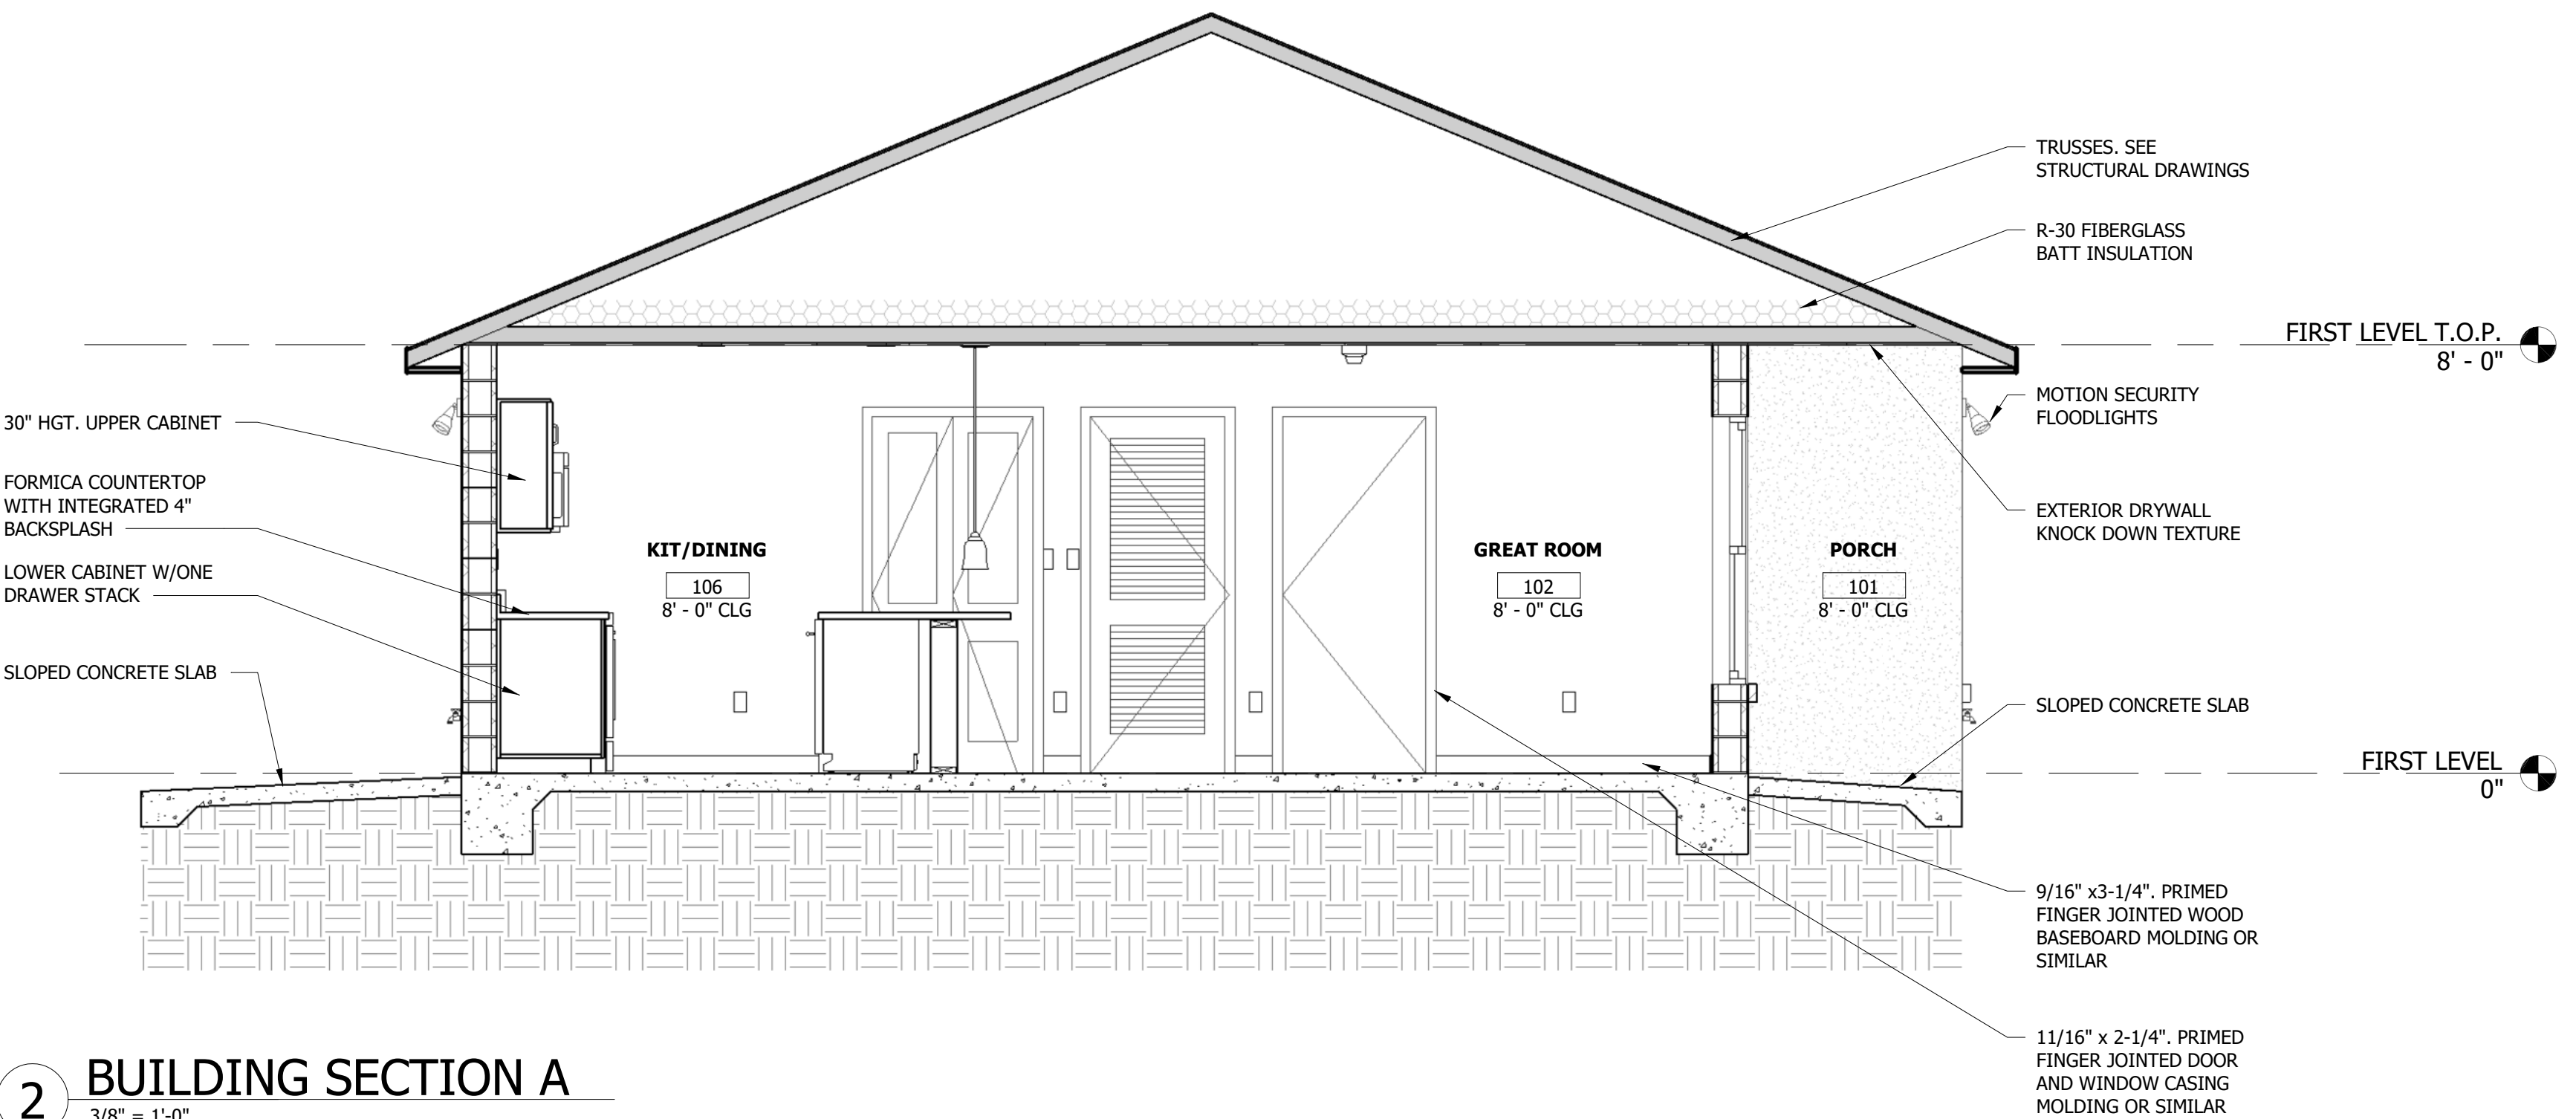

2 BUILDING SECTION A
3/8" = 1'-0"

