


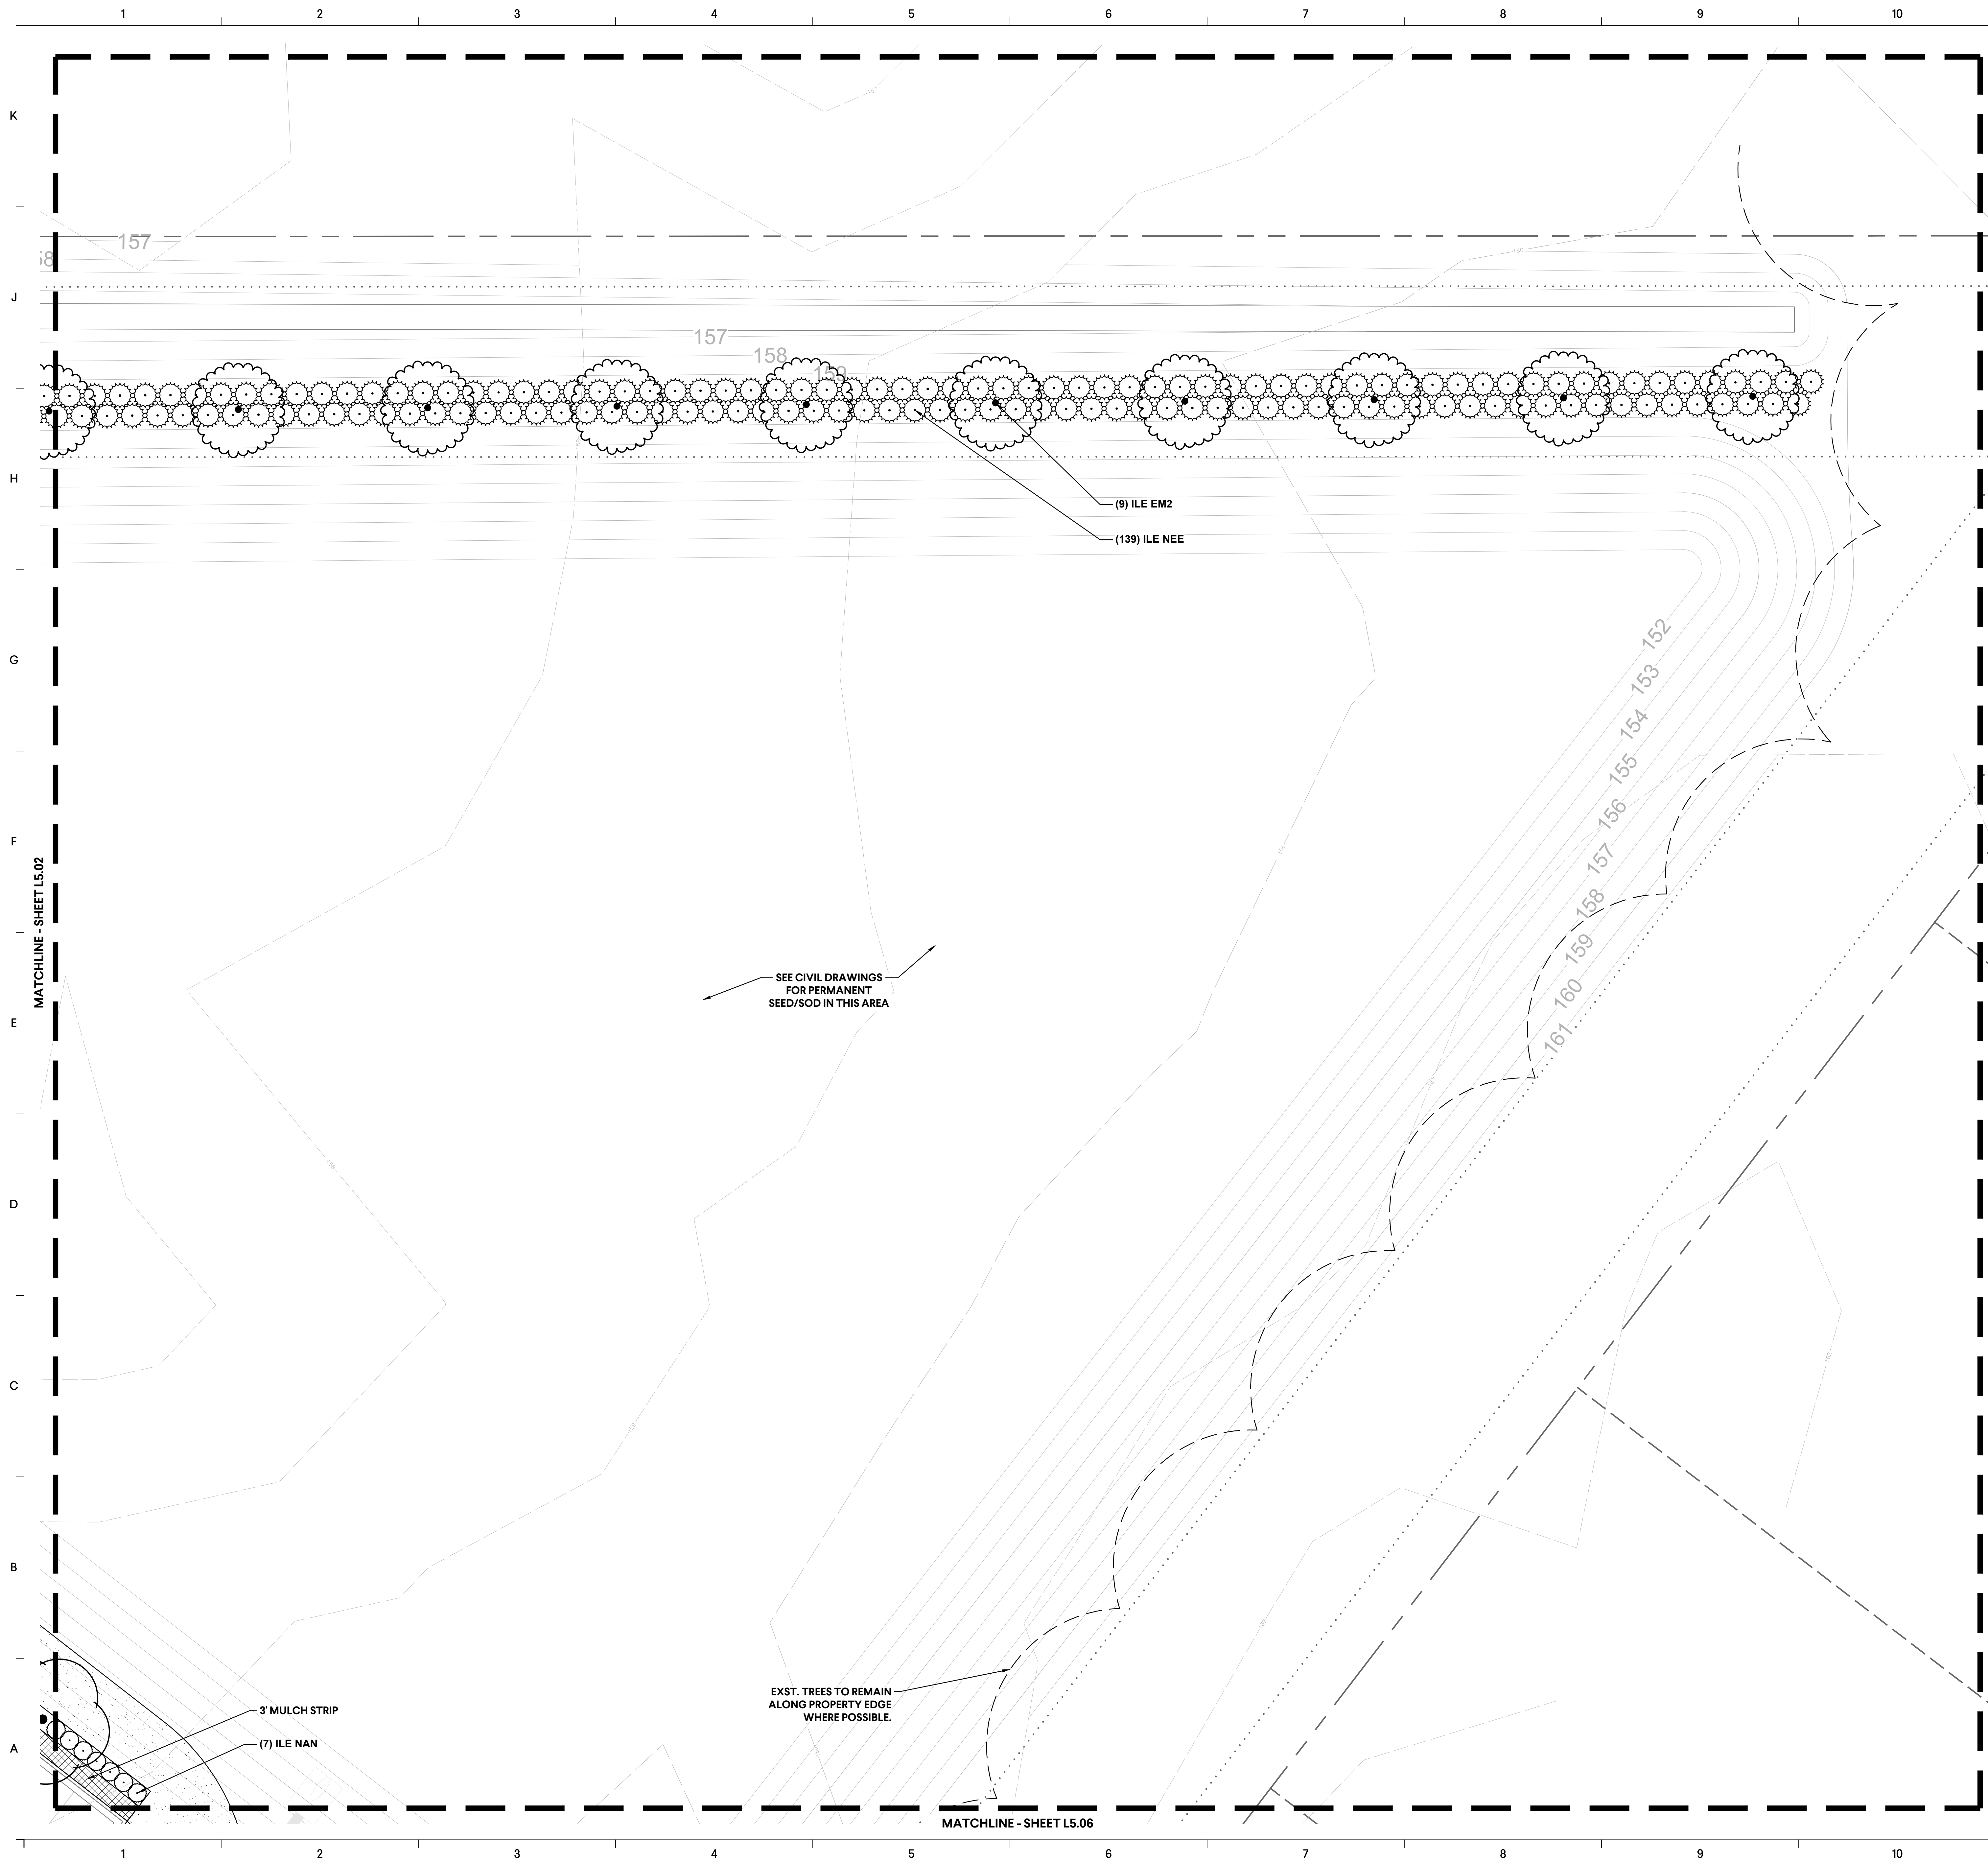

| PLANT SCHEDULE |                                                |                                     |
|----------------|------------------------------------------------|-------------------------------------|
| CODE           | BOTANICAL NAME                                 | COMMON NAME                         |
| TREES          |                                                |                                     |
| ILE LIB        | ILEX X 'CONTY'                                 | LIBERTY™ HOLLY                      |
| ILE EM2        | ILEX X 'EMILY BRUNER'                          | EMILY BRUNER HOLLY                  |
| LAG WHI        | LAGERSTROEMIA<br>INDICA X FAURIEI<br>'NATCHEZ' | NATCHEZ CRAPE MYRTLE<br>MULTI-TRUNK |
| LIR EMC        | LIRIODENDRON<br>TULIPIFERA 'JFS-OZ'            | EMERALD CITY® TULIP<br>POPLAR       |
| PIS CHI        | PISTACIA CHINENSIS                             | CHINESE PISTACHE                    |
| QOU NUT        | QUERCUS NUTTALLII                              | NUTTALL OAK                         |
| ULM PRI        | ULMUS AMERICANA<br>'PRINCETON'                 | PRINCETON AMERICAN ELM              |
| SHRUBS         |                                                |                                     |
| GAR FRO        | GARDENIA<br>JASMINOIDES<br>'FROSTPROOF'        | FROSTPROOF GARDENIA                 |
| ILE CRS        | ILEX CORNUTA<br>'CARISSA'                      | CARISSA CHINESE HOLLY               |
| ILE NEE        | ILEX CORNUTA<br>'NEEDLEPOINT'                  | NEEDLEPOINT CHINESE<br>HOLLY        |
| ILE SHA        | ILEX GLABRA<br>'SHAMROCK'                      | SHAMROCK INKBERRY<br>HOLLY          |
| ILE NAN        | ILEX VOMITORIA 'NANA'                          | DWARF YAUPON HOLLY                  |
| ROS CRL        | ROSA X 'CORAL DRIFT'                           | CORAL DRIFT ROSE                    |
| SHRUB AREAS    |                                                |                                     |
| MUH CAP        | MUHLENBERGIA<br>CAPILLARIS                     | WHITE AND PINK MUHLY<br>GRASS       |
| GROUND COVERS  |                                                |                                     |
| CYN TI3        | CYNODON DACTYLON<br>'TIF 419'                  | TIF 419 BERMUDA GRASS               |
| LIR SBL        | LIRIOPE MUSCARI<br>'SUPER BLUE'                | SUPER BLUE LILYTURF                 |
| MULCH          | PINE STRAW MULCH                               | PINE STRAW MULCH                    |

## NOTES

1. CONTRACTOR SHALL HAND WATER ALL PLANT MATERIAL AND SOD DURING CONSTRUCTION UNTIL SUBSTANTIAL COMPLETION HAS BEEN ACHIEVED.
2. CONTRACTOR IS TO PROVIDE ALL TREES WITH SLOW RELEASE WATER BAGS. WATER BAGS ARE TO BE CONSISTENTLY FILLED DURING CONSTRUCTION SO THAT THE TREES WILL HAVE WATER AT ALL TIMES. AT THE TIME OF SUBSTANTIAL COMPLETION, CONTRACTOR IS TO MEET ON SITE WITH OWNER OR OWNER'S MAINTENANCE REPRESENTATIVE TO REVIEW THE INSTRUCTIONS AND THE SCHEDULING OF REFILLING THE BAGS. CONTRACTOR SHALL REFILL ALL BAGS AT THE TIME OF THE MEETING.
3. ALL DISTURBED AREAS NOT COVERED BY PLANT MATERIAL OR SOD ARE TO BE SEEDED ACCORDING TO CIVIL DRAWINGS. SEE C-DRAWINGS FOR MORE INFORMATION.

**SITE FURNISHINGS:**

- (3) PETOSKEY TRASH RECEPTACLES BY LANDSCAPE FORMS OR APPROVED EQUAL. 1 TO BE PLACED AT FRONT DOOR, 1 AT SIDE DOOR AND 1 ON THE BACK PATIO.
- (4) LARCHMONT PICNIC TABLES BY COUNTRY CASUAL OR APPROVED EQUAL. ALL FOUR TABLES ARE TO BE LOCATED ON THE BACK PATIO.
- (5) 6' LONG WELLSPRING BENCHES BY LANDSCAPE FORMS OR APPROVED EQUAL. BOTH BENCHES ARE TO BE LOCATED ON THE BACK PATIO.
- SEE 02970 SITE FURNISHING SPECIFICATION FOR DETAILS. ALL SITE FURNISHING LOCATIONS TO BE APPROVED BY OWNER'S REPRESENTATIVE PRIOR TO INSTALLATION.

